





ተጽዕኖ ለግብረ ሰባት
 ተጽዕኖ ለግብረ ሰባት
 ለ ግብረ ሰባት ለ ግብረ ሰባት
 ተጽዕኖ ለግብረ ሰባት ለ ግብረ ሰባት
 ተጽዕኖ ለግብረ ሰባት ለ ግብረ ሰባት
 ተጽዕኖ ለግብረ ሰባት ለ ግብረ ሰባት




CONSULTATION ARCHITECTURALE ET SUIVI DES TRAVAUX DE CONSTRUCTION DE LYCEE QUALIFIANT IBN ROCHD A LA CT ZAIDA RELEVANT DE LA DIRECTION PROVINCIALE DE L'AREF - DT DE MIDELT






المملكة المغربية
 وزارة التربية الوطنية
 والتعليم الأولي والرياضة
 الأكاديمية الجهوية للتربية والتكوين
 جهة تافيلالت
 المديرية الإقليمية بميدلت

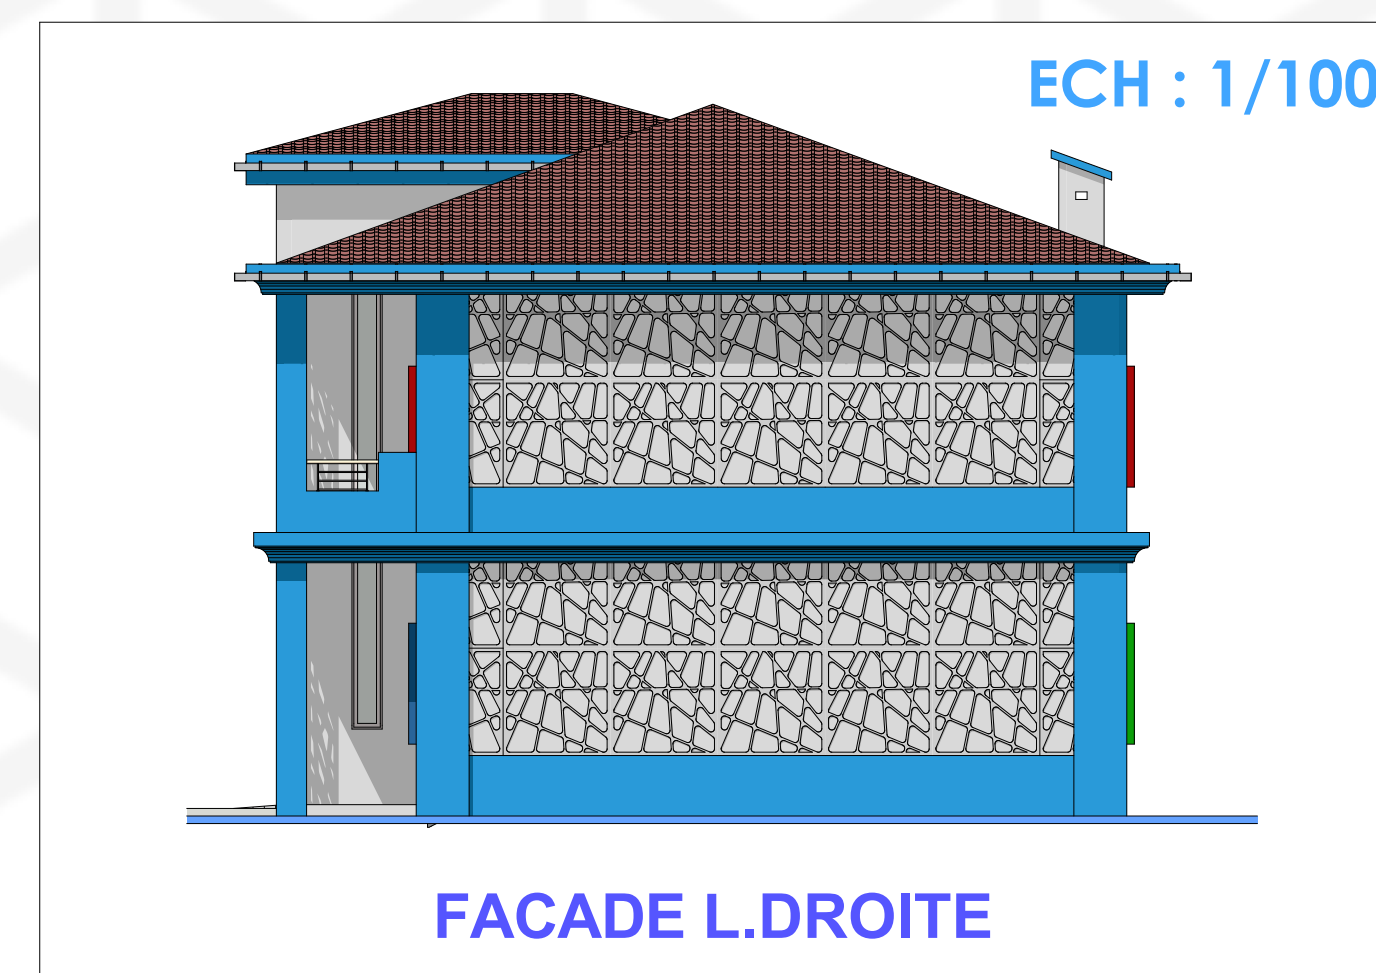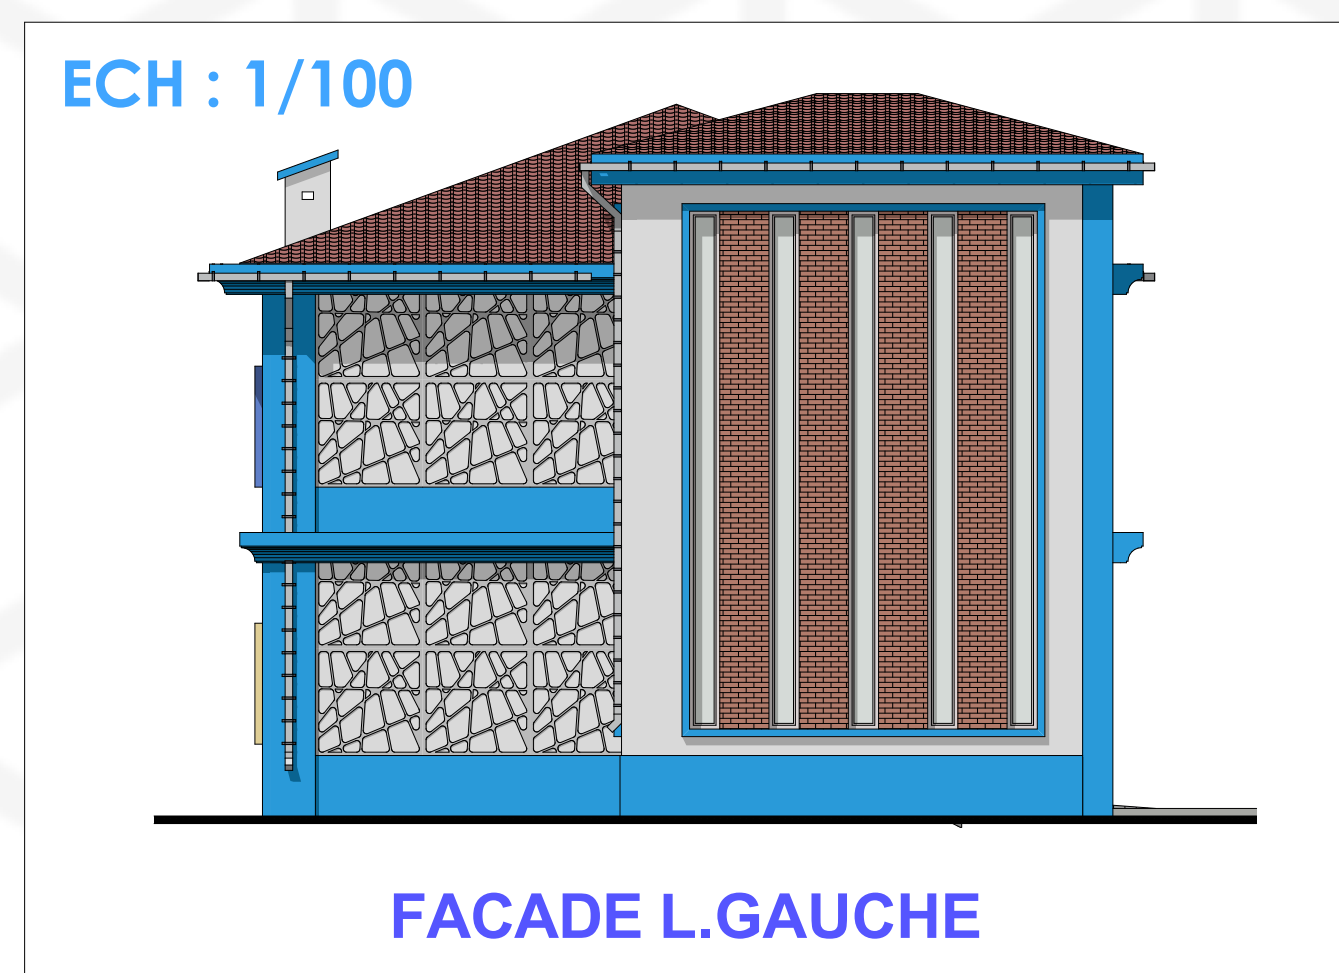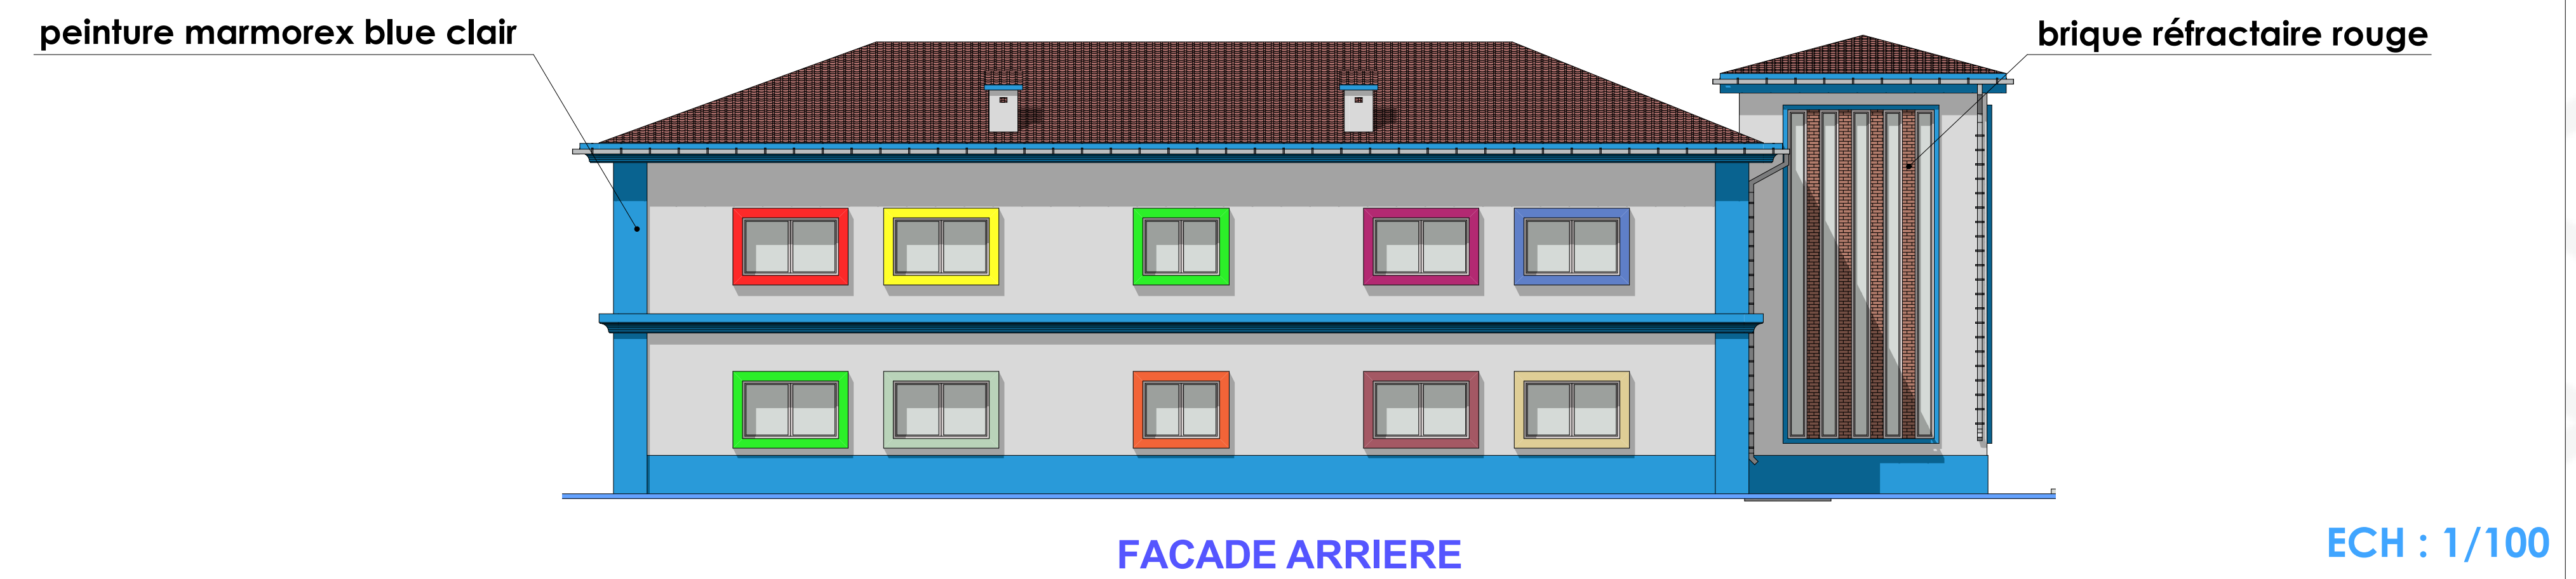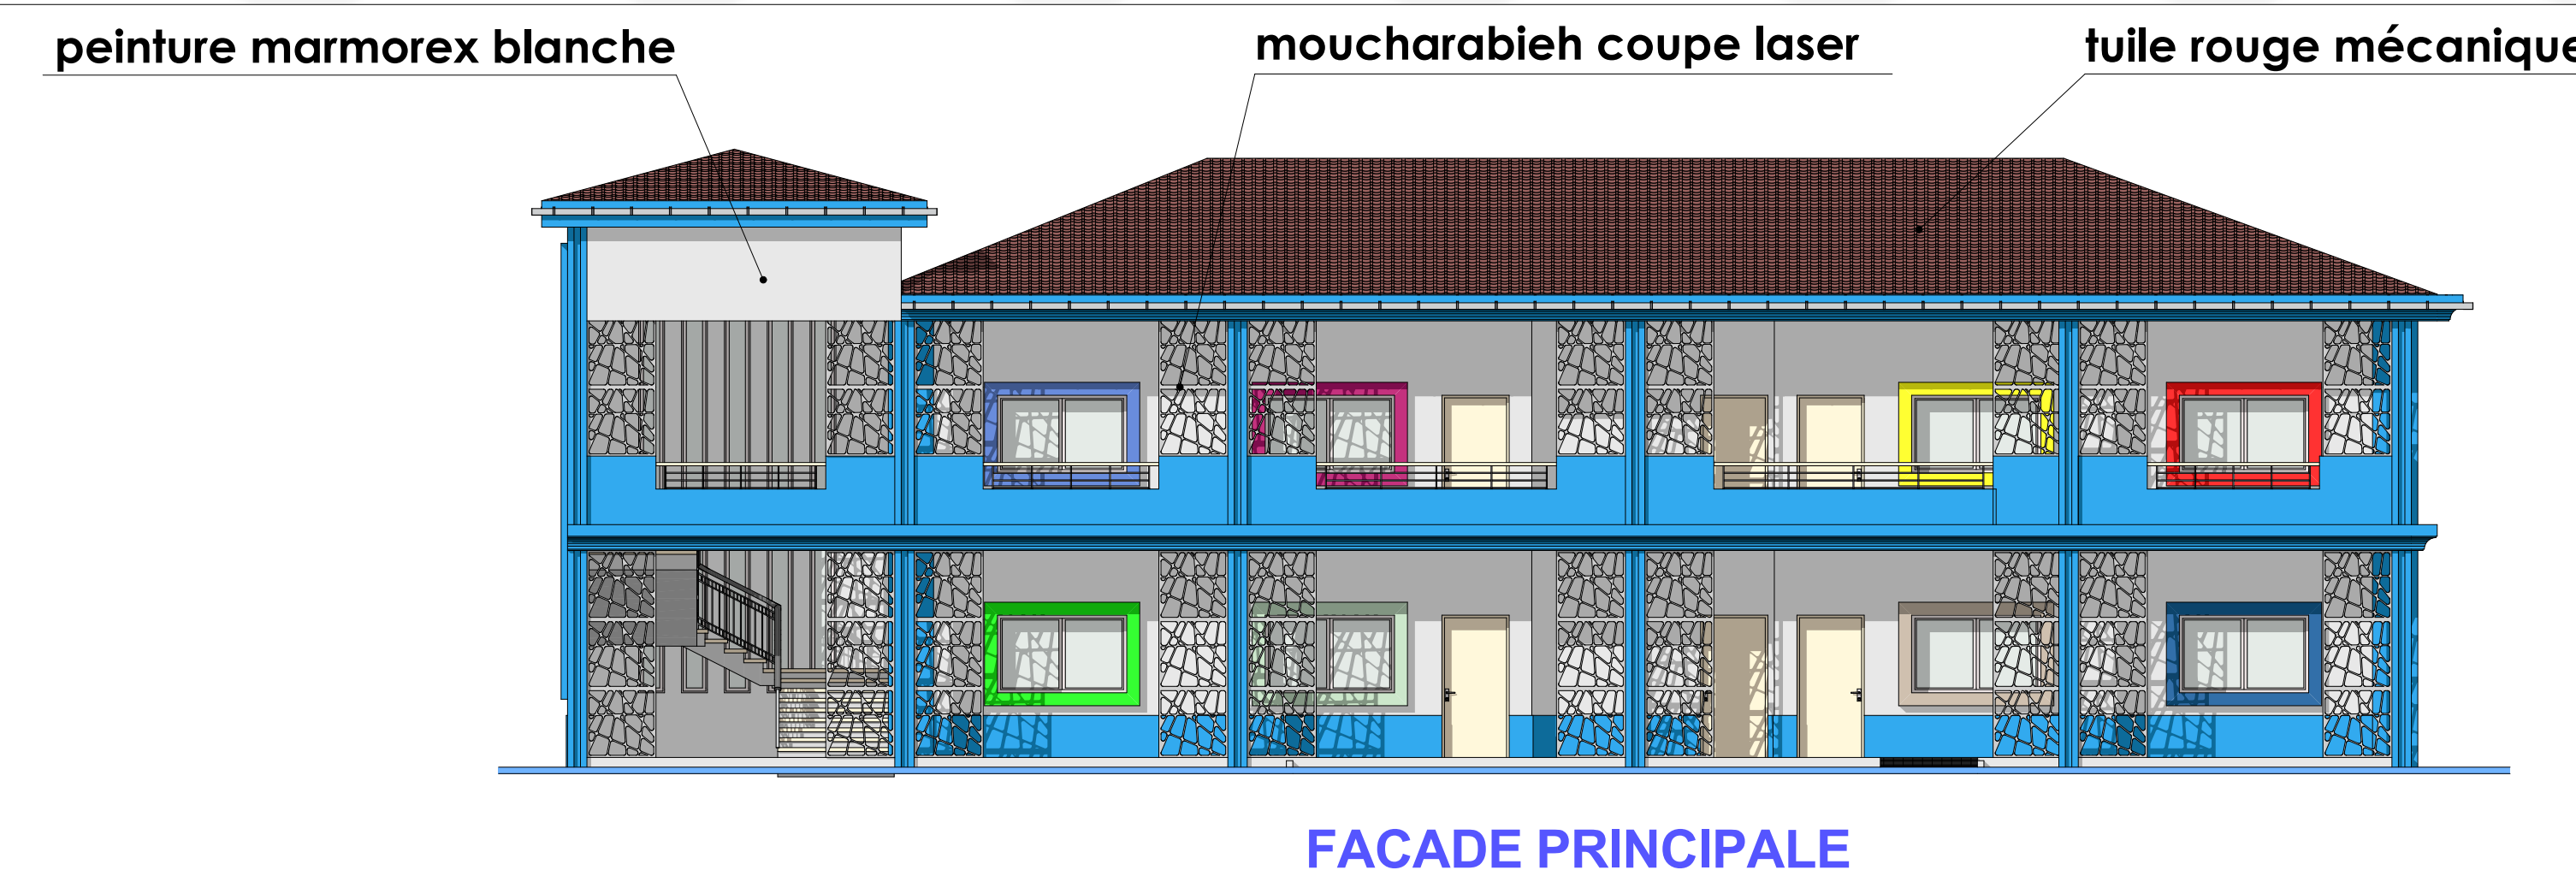

VUES D'AMBIANCES

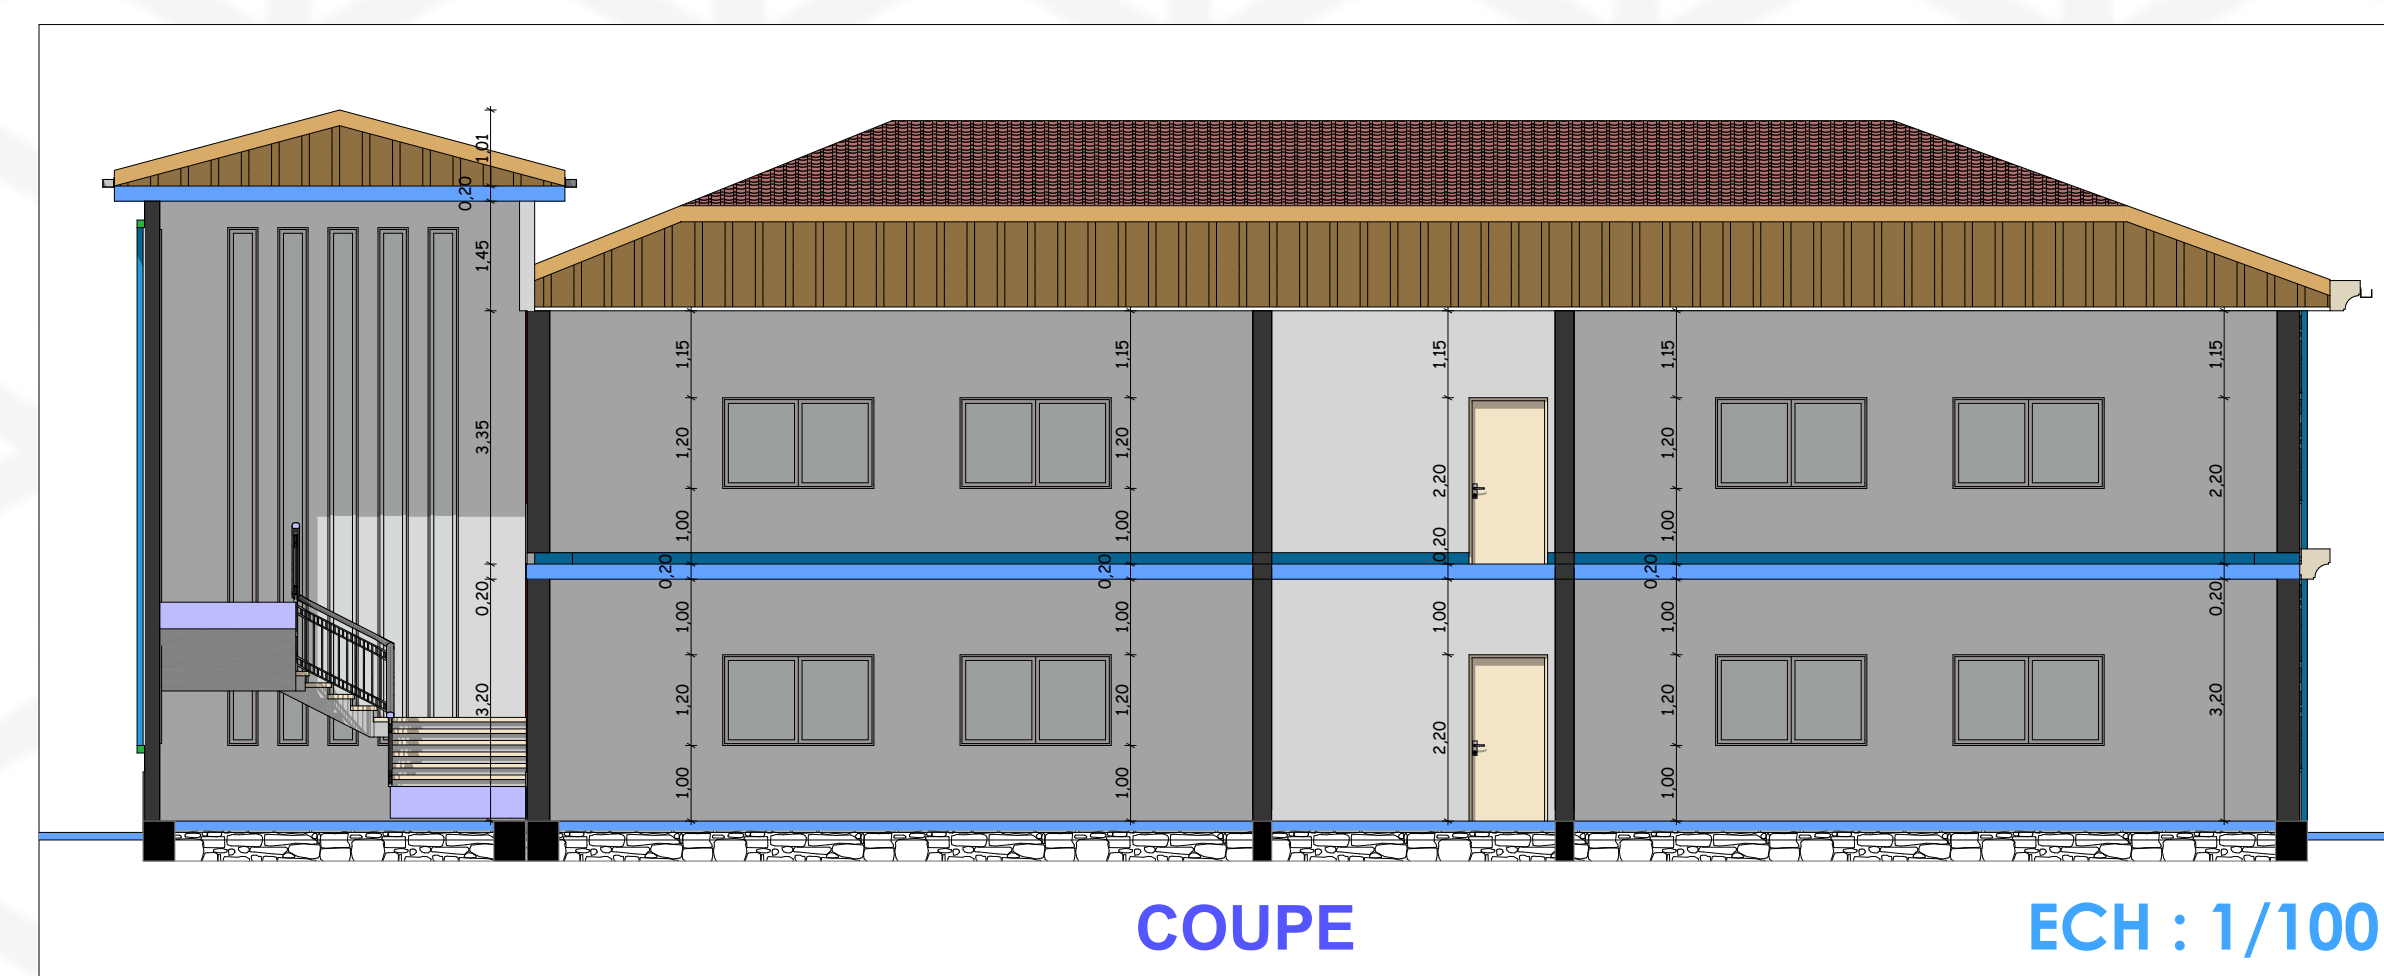

PLAN MASSE - SITUATION

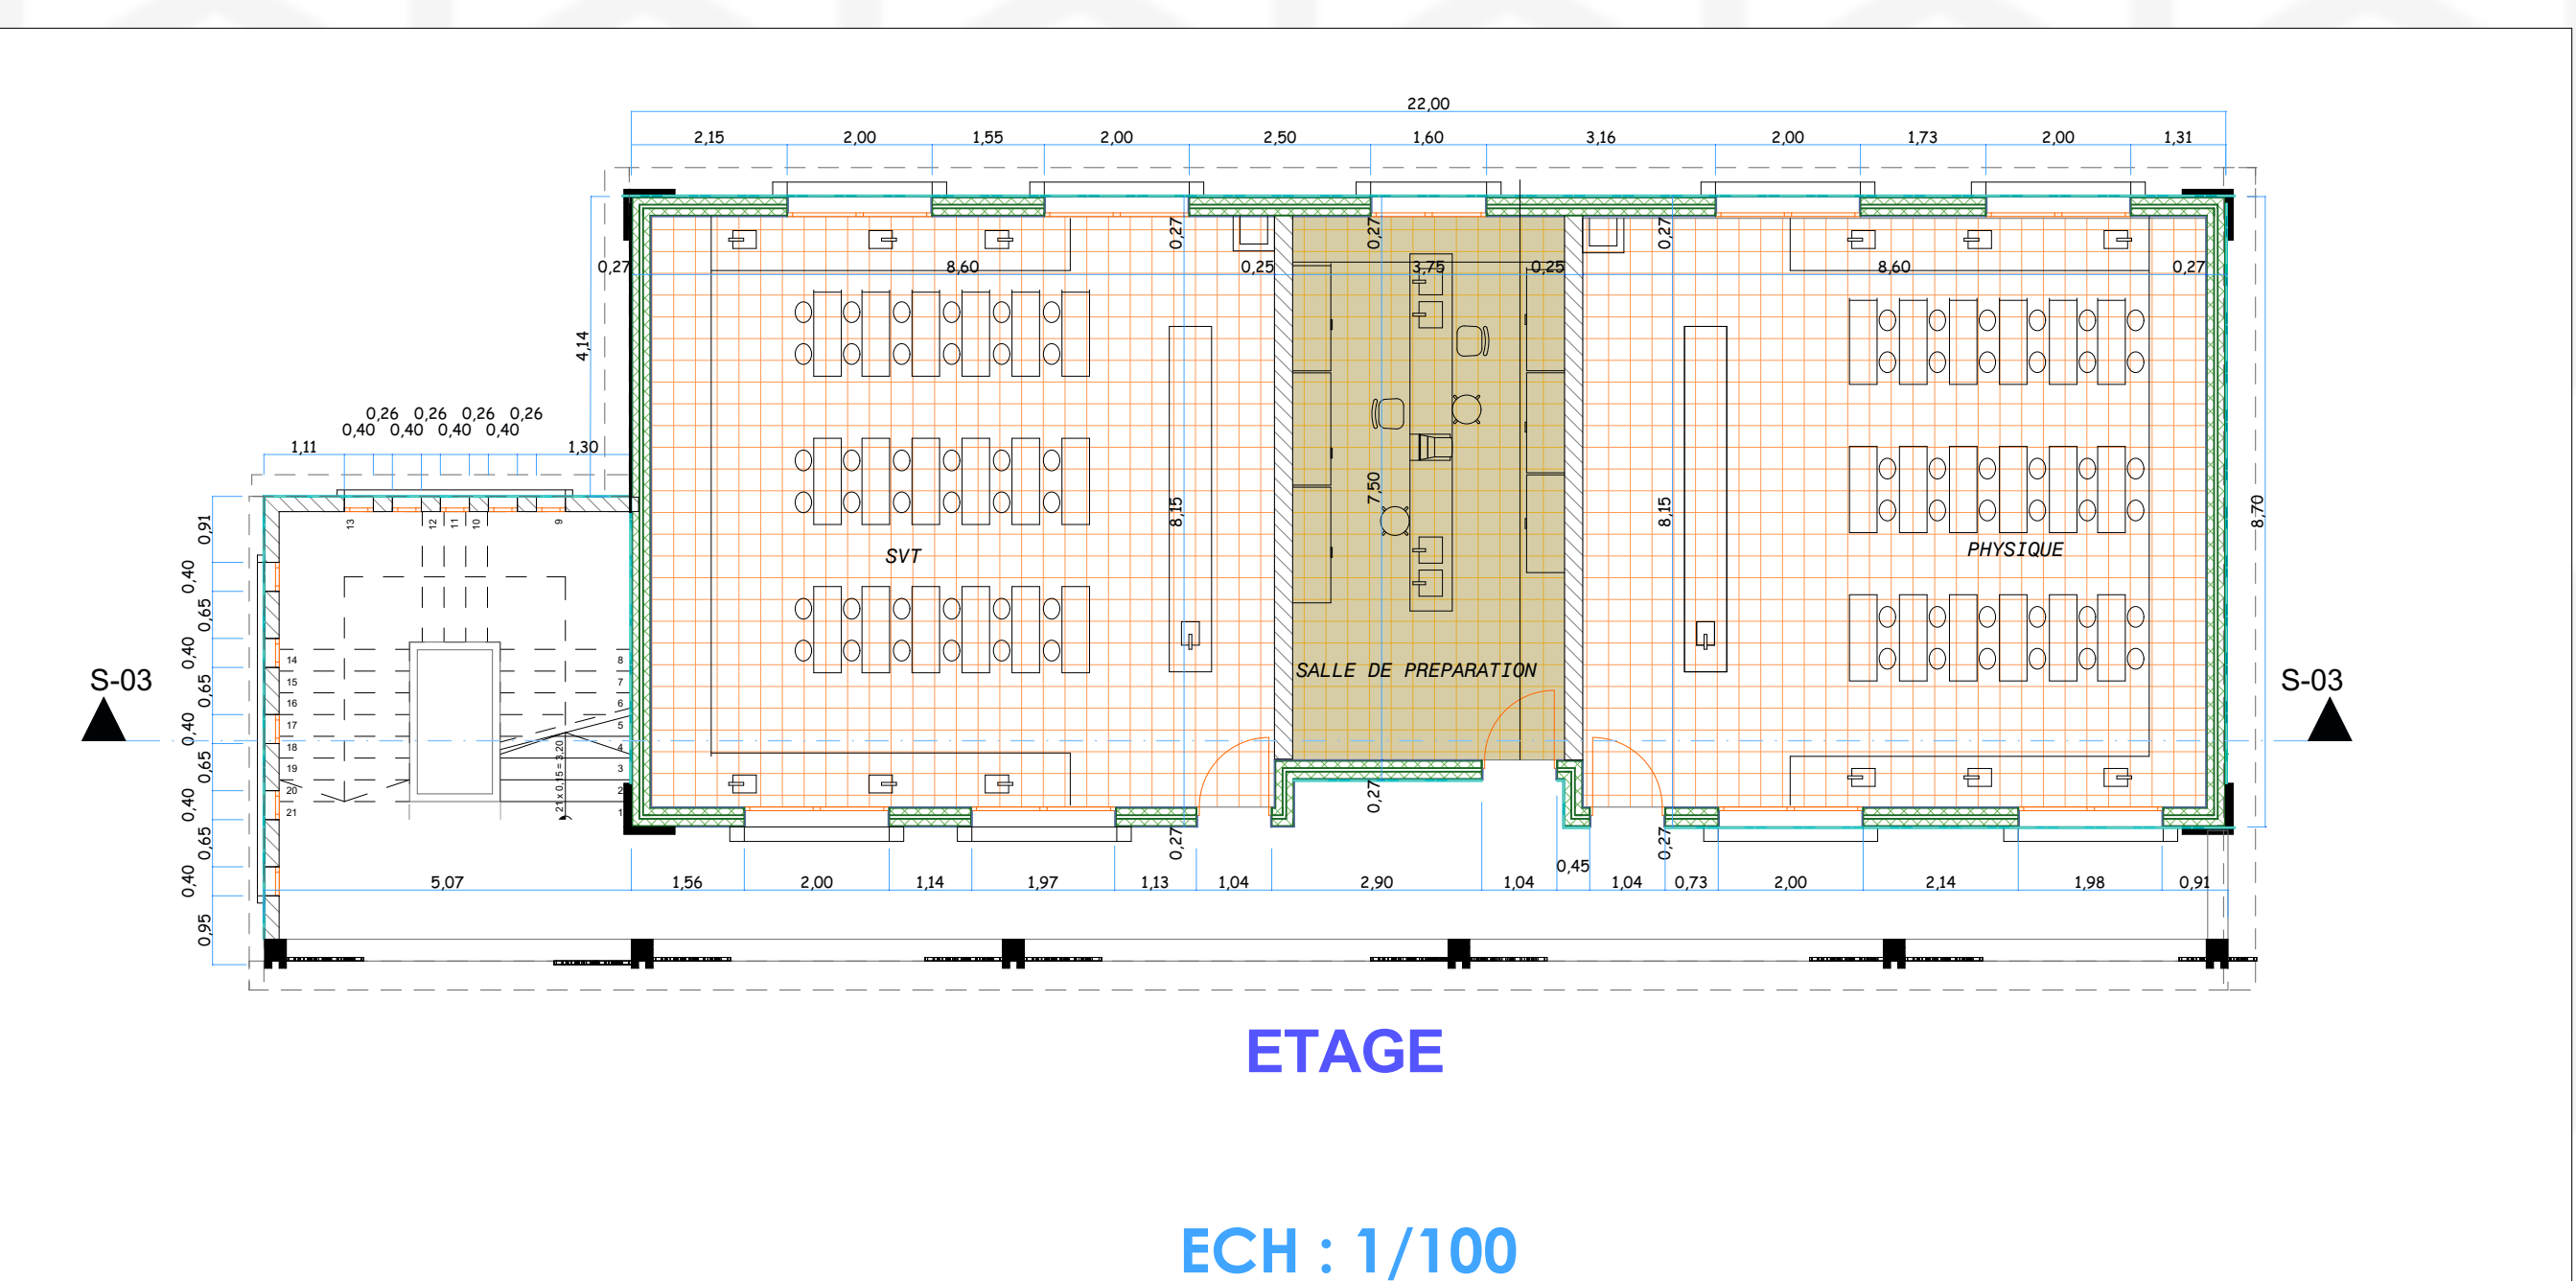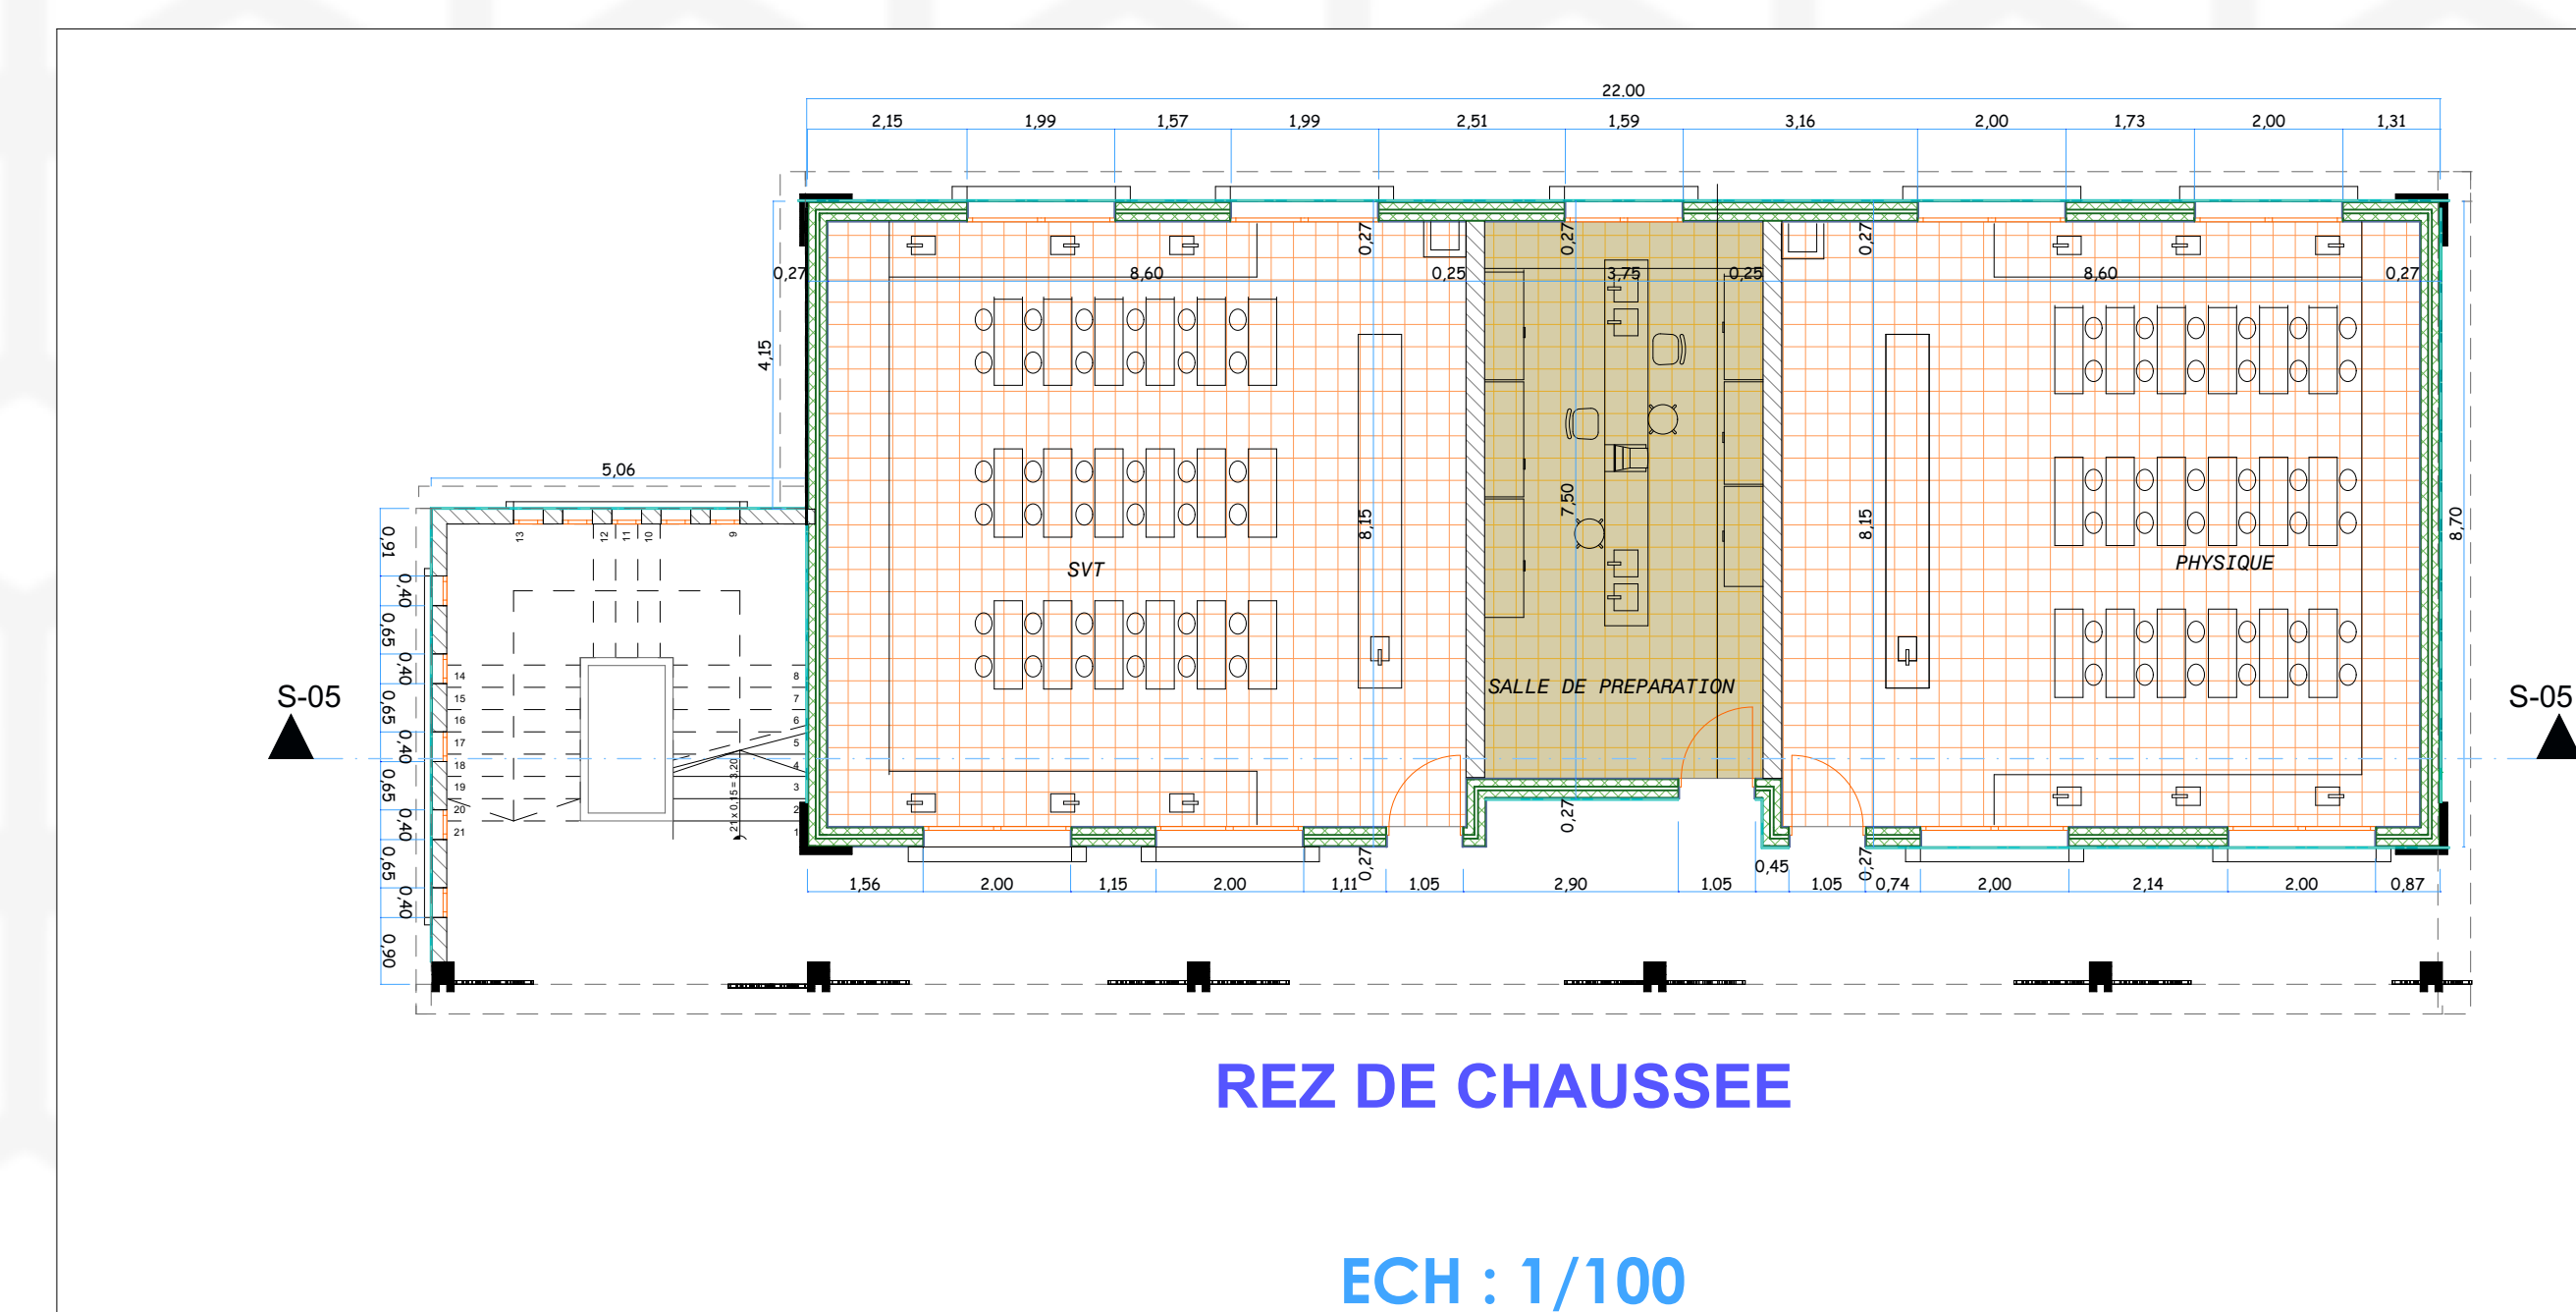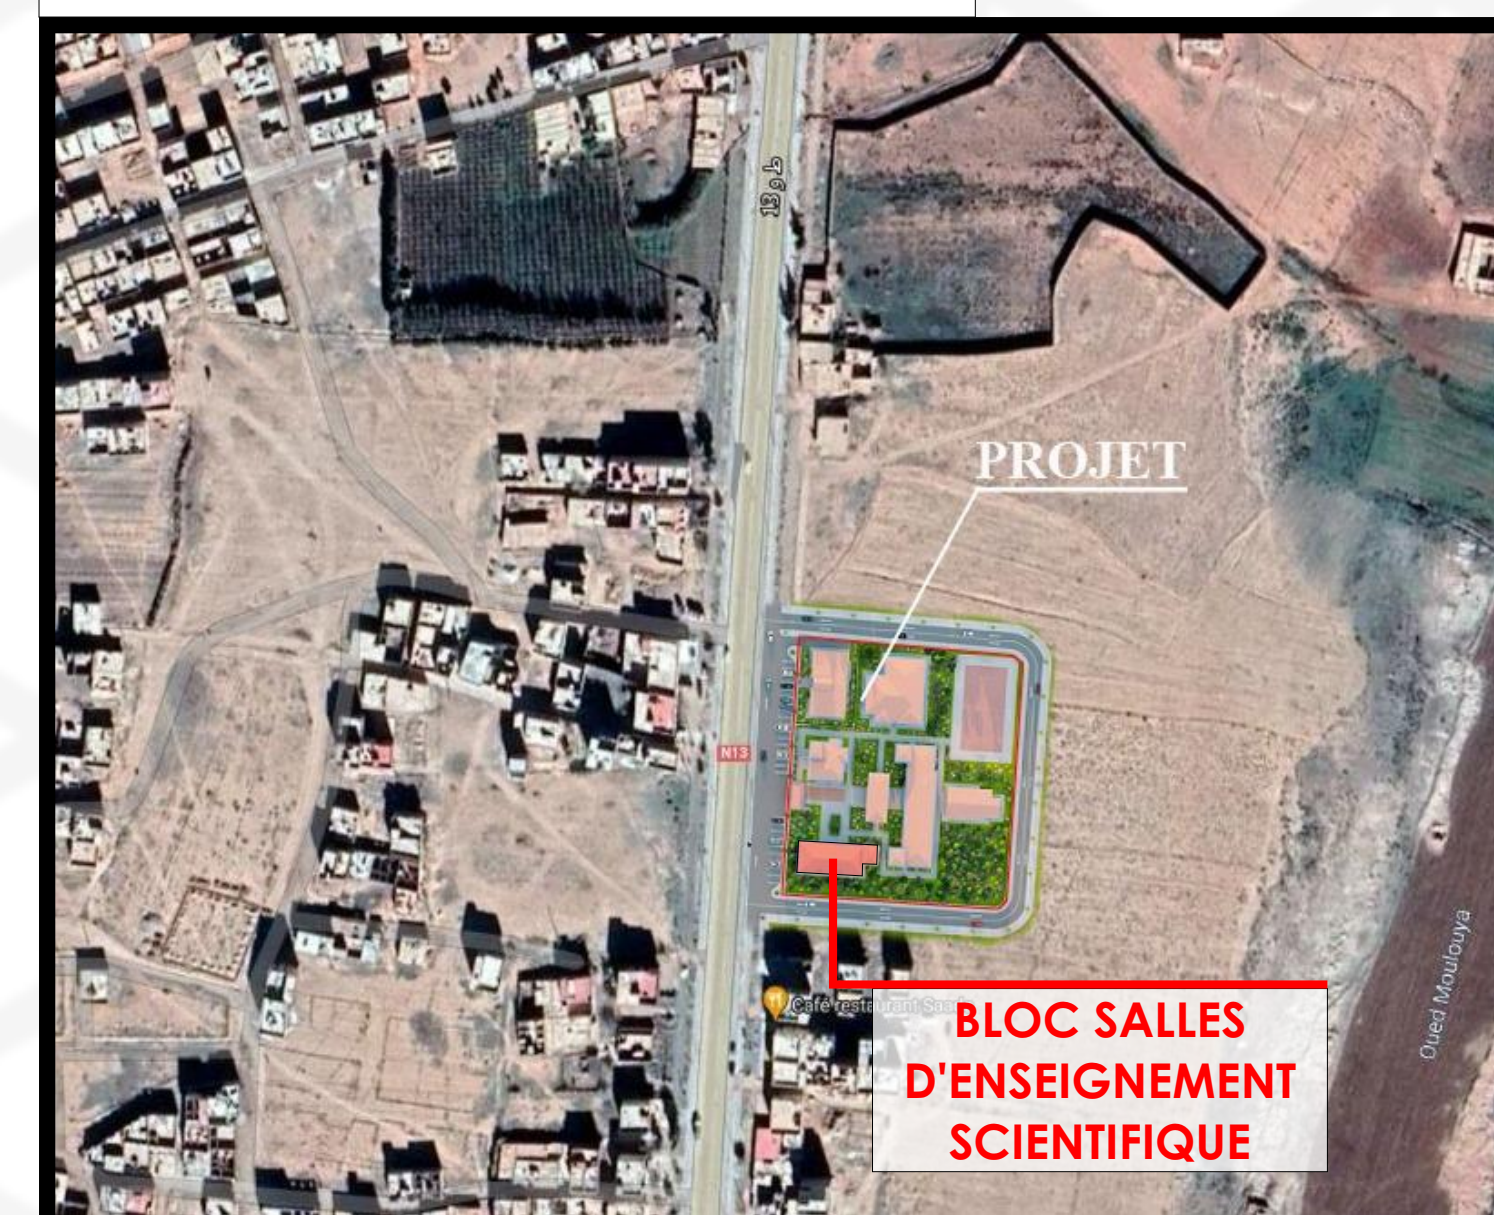


BLOC SALLES D'ENSEIGNEMENT SCIENTIFIQUE

FAÇADES / COUPE / PLANS / PLAN DE MASSE - SITUATION / VUES D'AMBIANCES



MY ABDELAZIZ EL HARRANE ARCHITECTE D.P.L.G

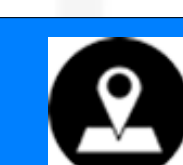

AV Hassan II 1er Etage App N° : 2 Midelt



Email : archiharrane@yahoo.fr



Tel - Fax : 05 35 36 00 79