




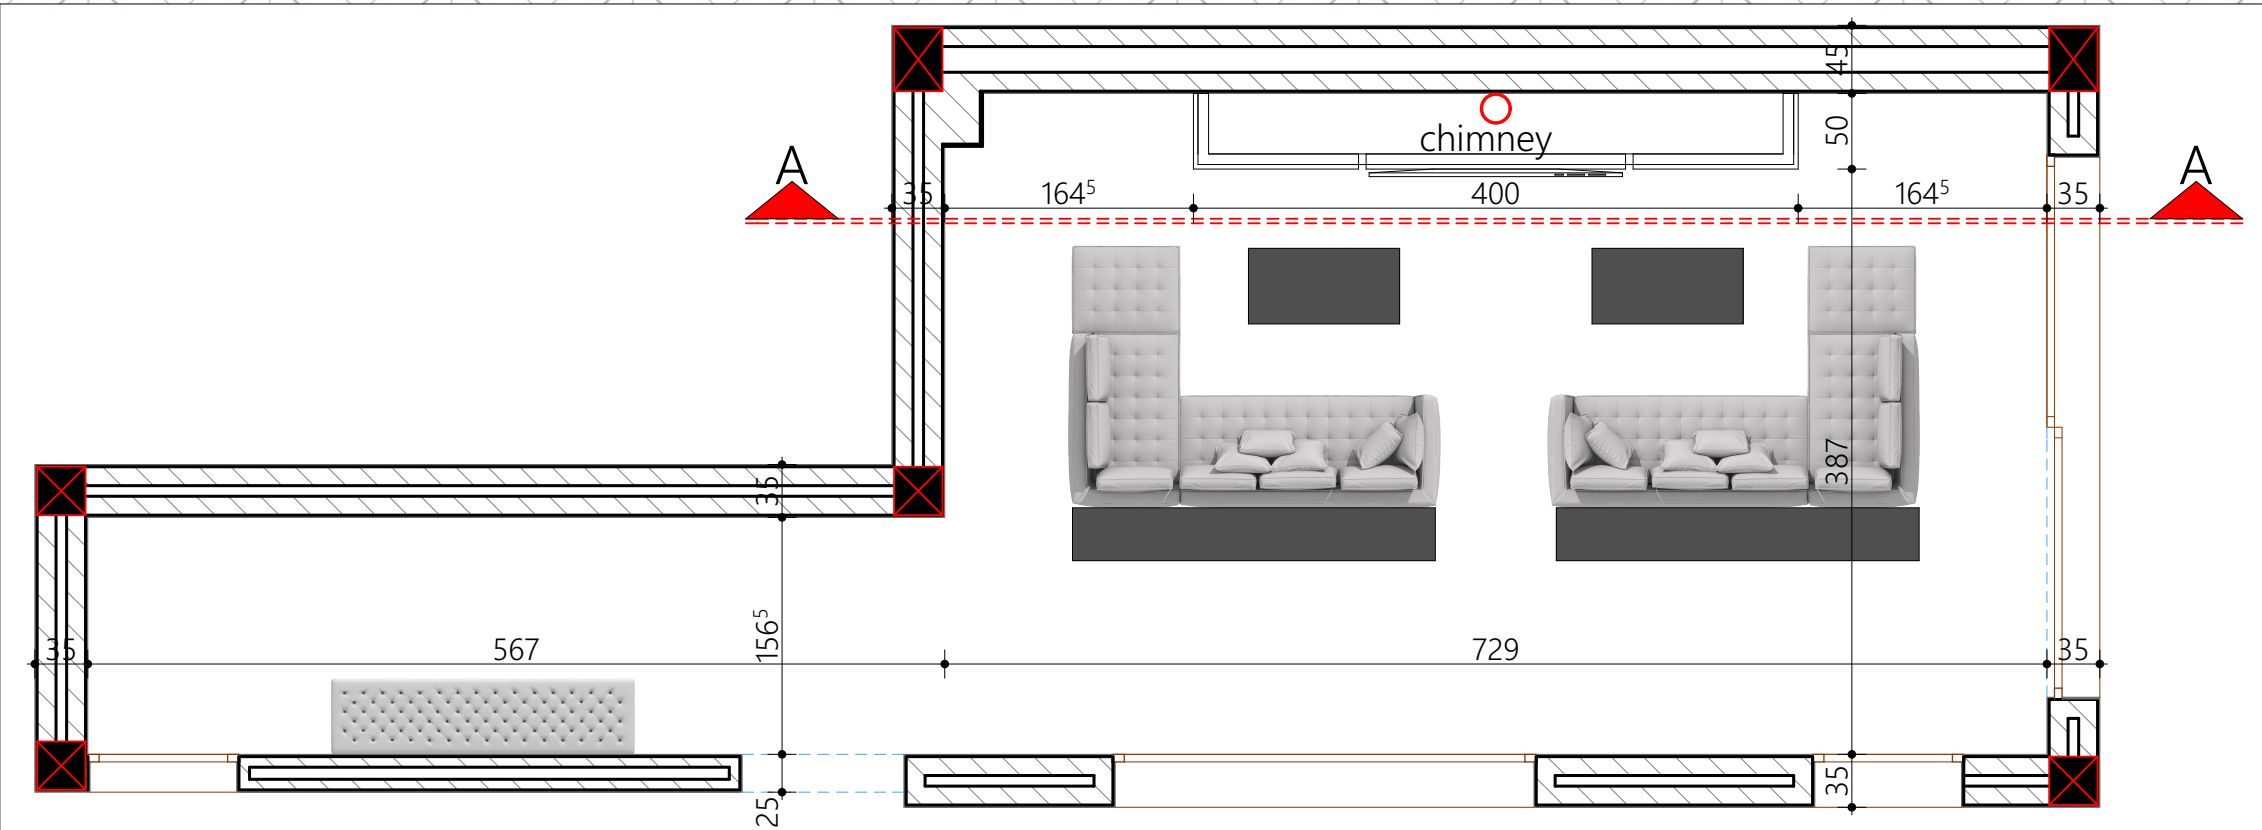

PLAN VIEW

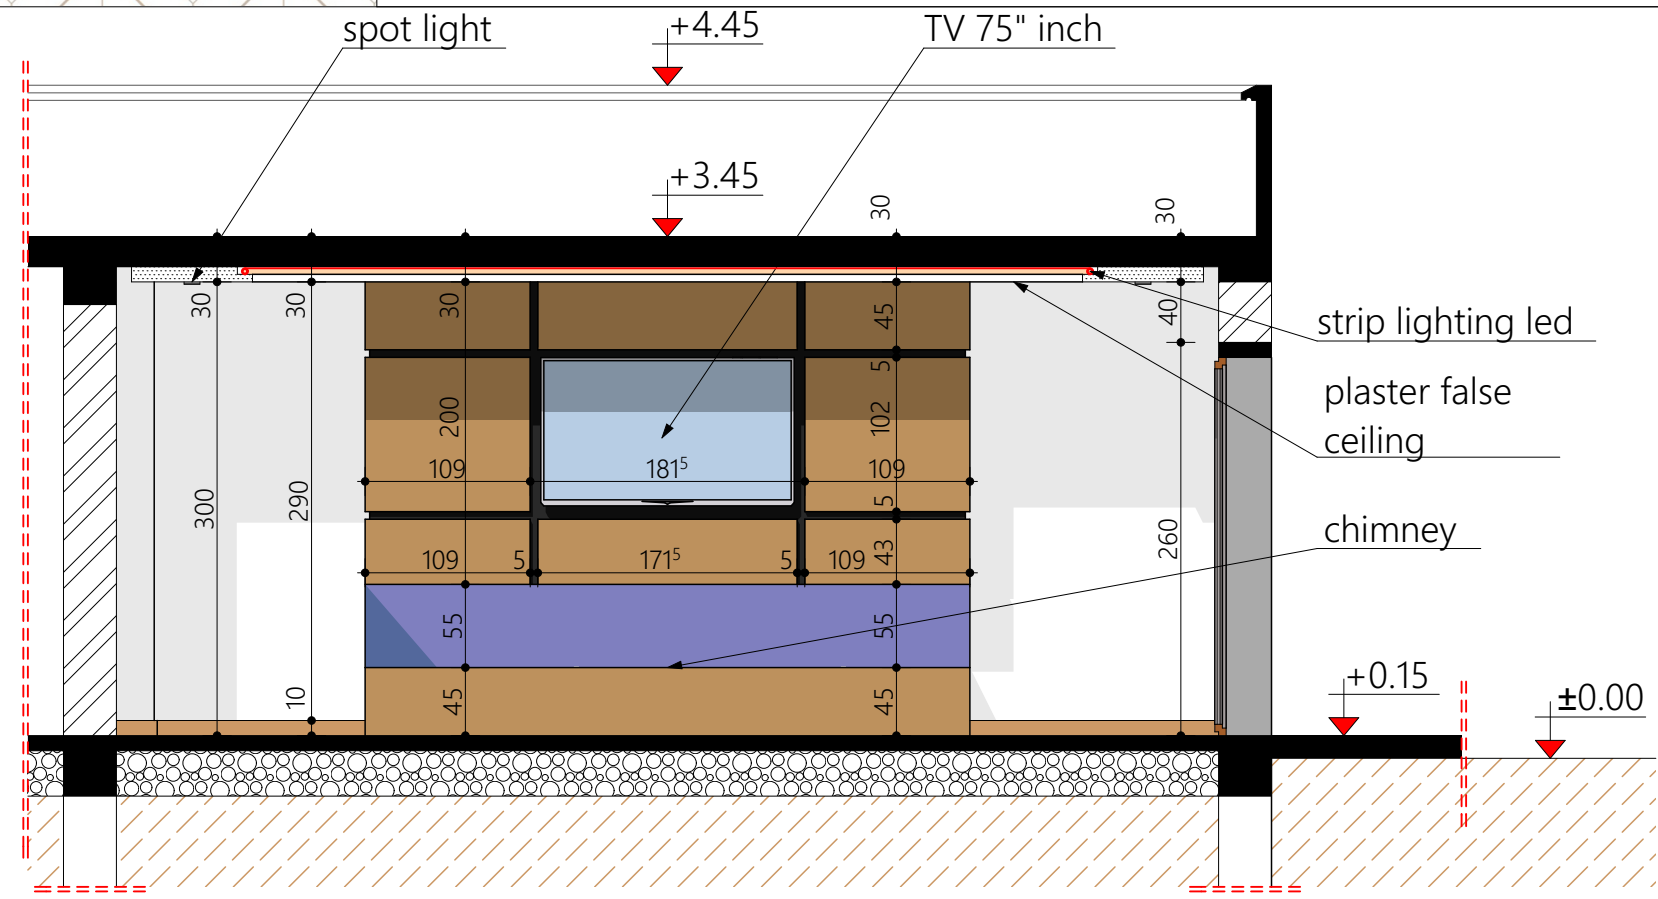

SECTION A-A

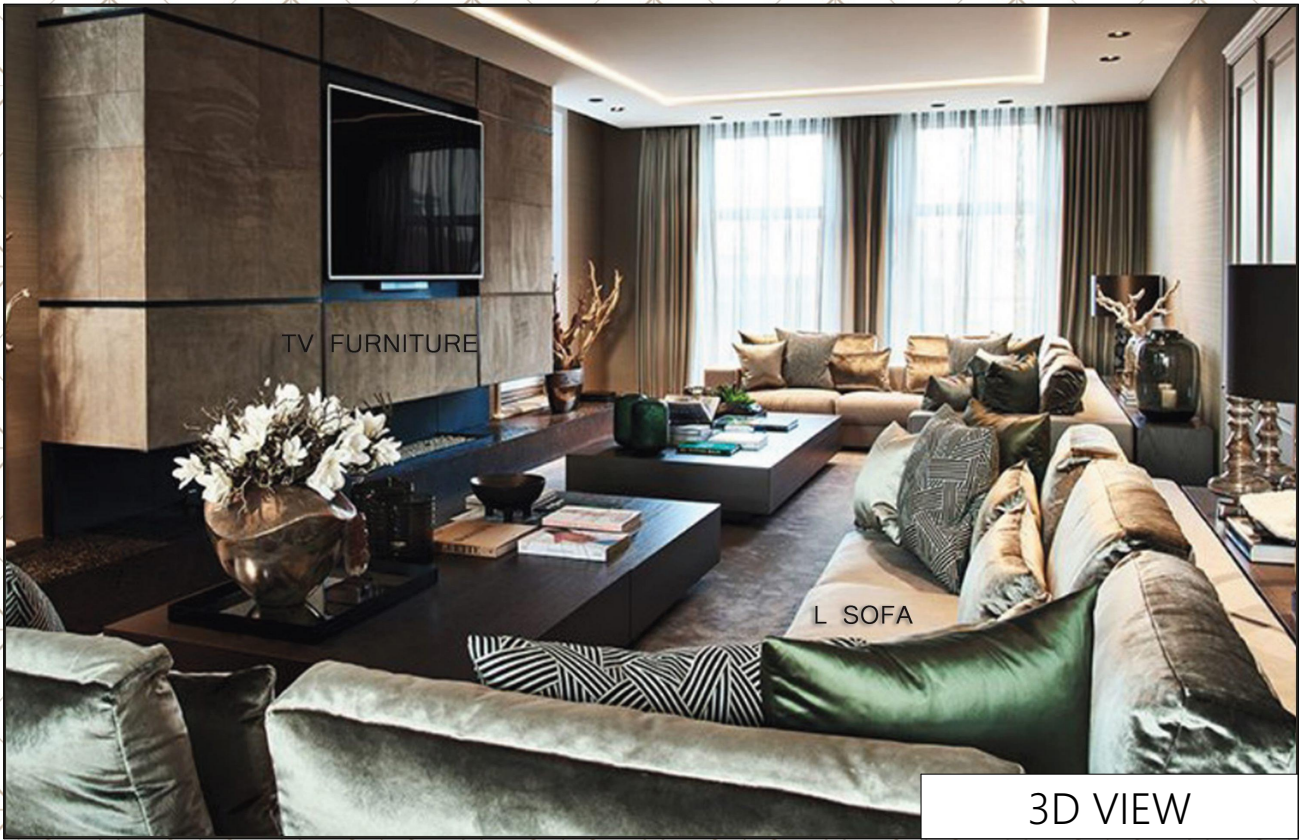

3D VIEW