

ⵜⴰⴳⴷⴰⵏⵜ ⵏ ⵙⵓⵔⵉⵏⵜ
ⵜⴰⴳⴷⴰⵏⵜ ⵏ ⵙⵓⵔⵉⵏⵜ
ⵏ ⵙⵓⵔⵉⵏⵜ ⵏ ⵙⵓⵔⵉⵏⵜ
ⵜⴰⴳⴷⴰⵏⵜ ⵏ ⵙⵓⵔⵉⵏⵜ
ⵜⴰⴳⴷⴰⵏⵜ ⵏ ⵙⵓⵔⵉⵏⵜ
ⵜⴰⴳⴷⴰⵏⵜ ⵏ ⵙⵓⵔⵉⵏⵜ



CONSULTATION ARCHITECTURALE ET SUIVI DES TRAVAUX DE CONSTRUCTION DE LYCEE QUALIFIANT IBN ROCHD A LA CT ZAIDA RELEVANT DE LA DIRECTION PROVINCIALE DE L'AREF - DT DE MIDELT





المملكة المغربية
وزارة التربية الوطنية
والتعليم العالي والرياضة
الأكاديمية الجهوية للتربية والتكوين
جهة درعة تافيلالت
المديرية الإقليمية بميدلت

BLOC ADMINISTRATION

FAÇADES/COUPE


ECH : 1/100

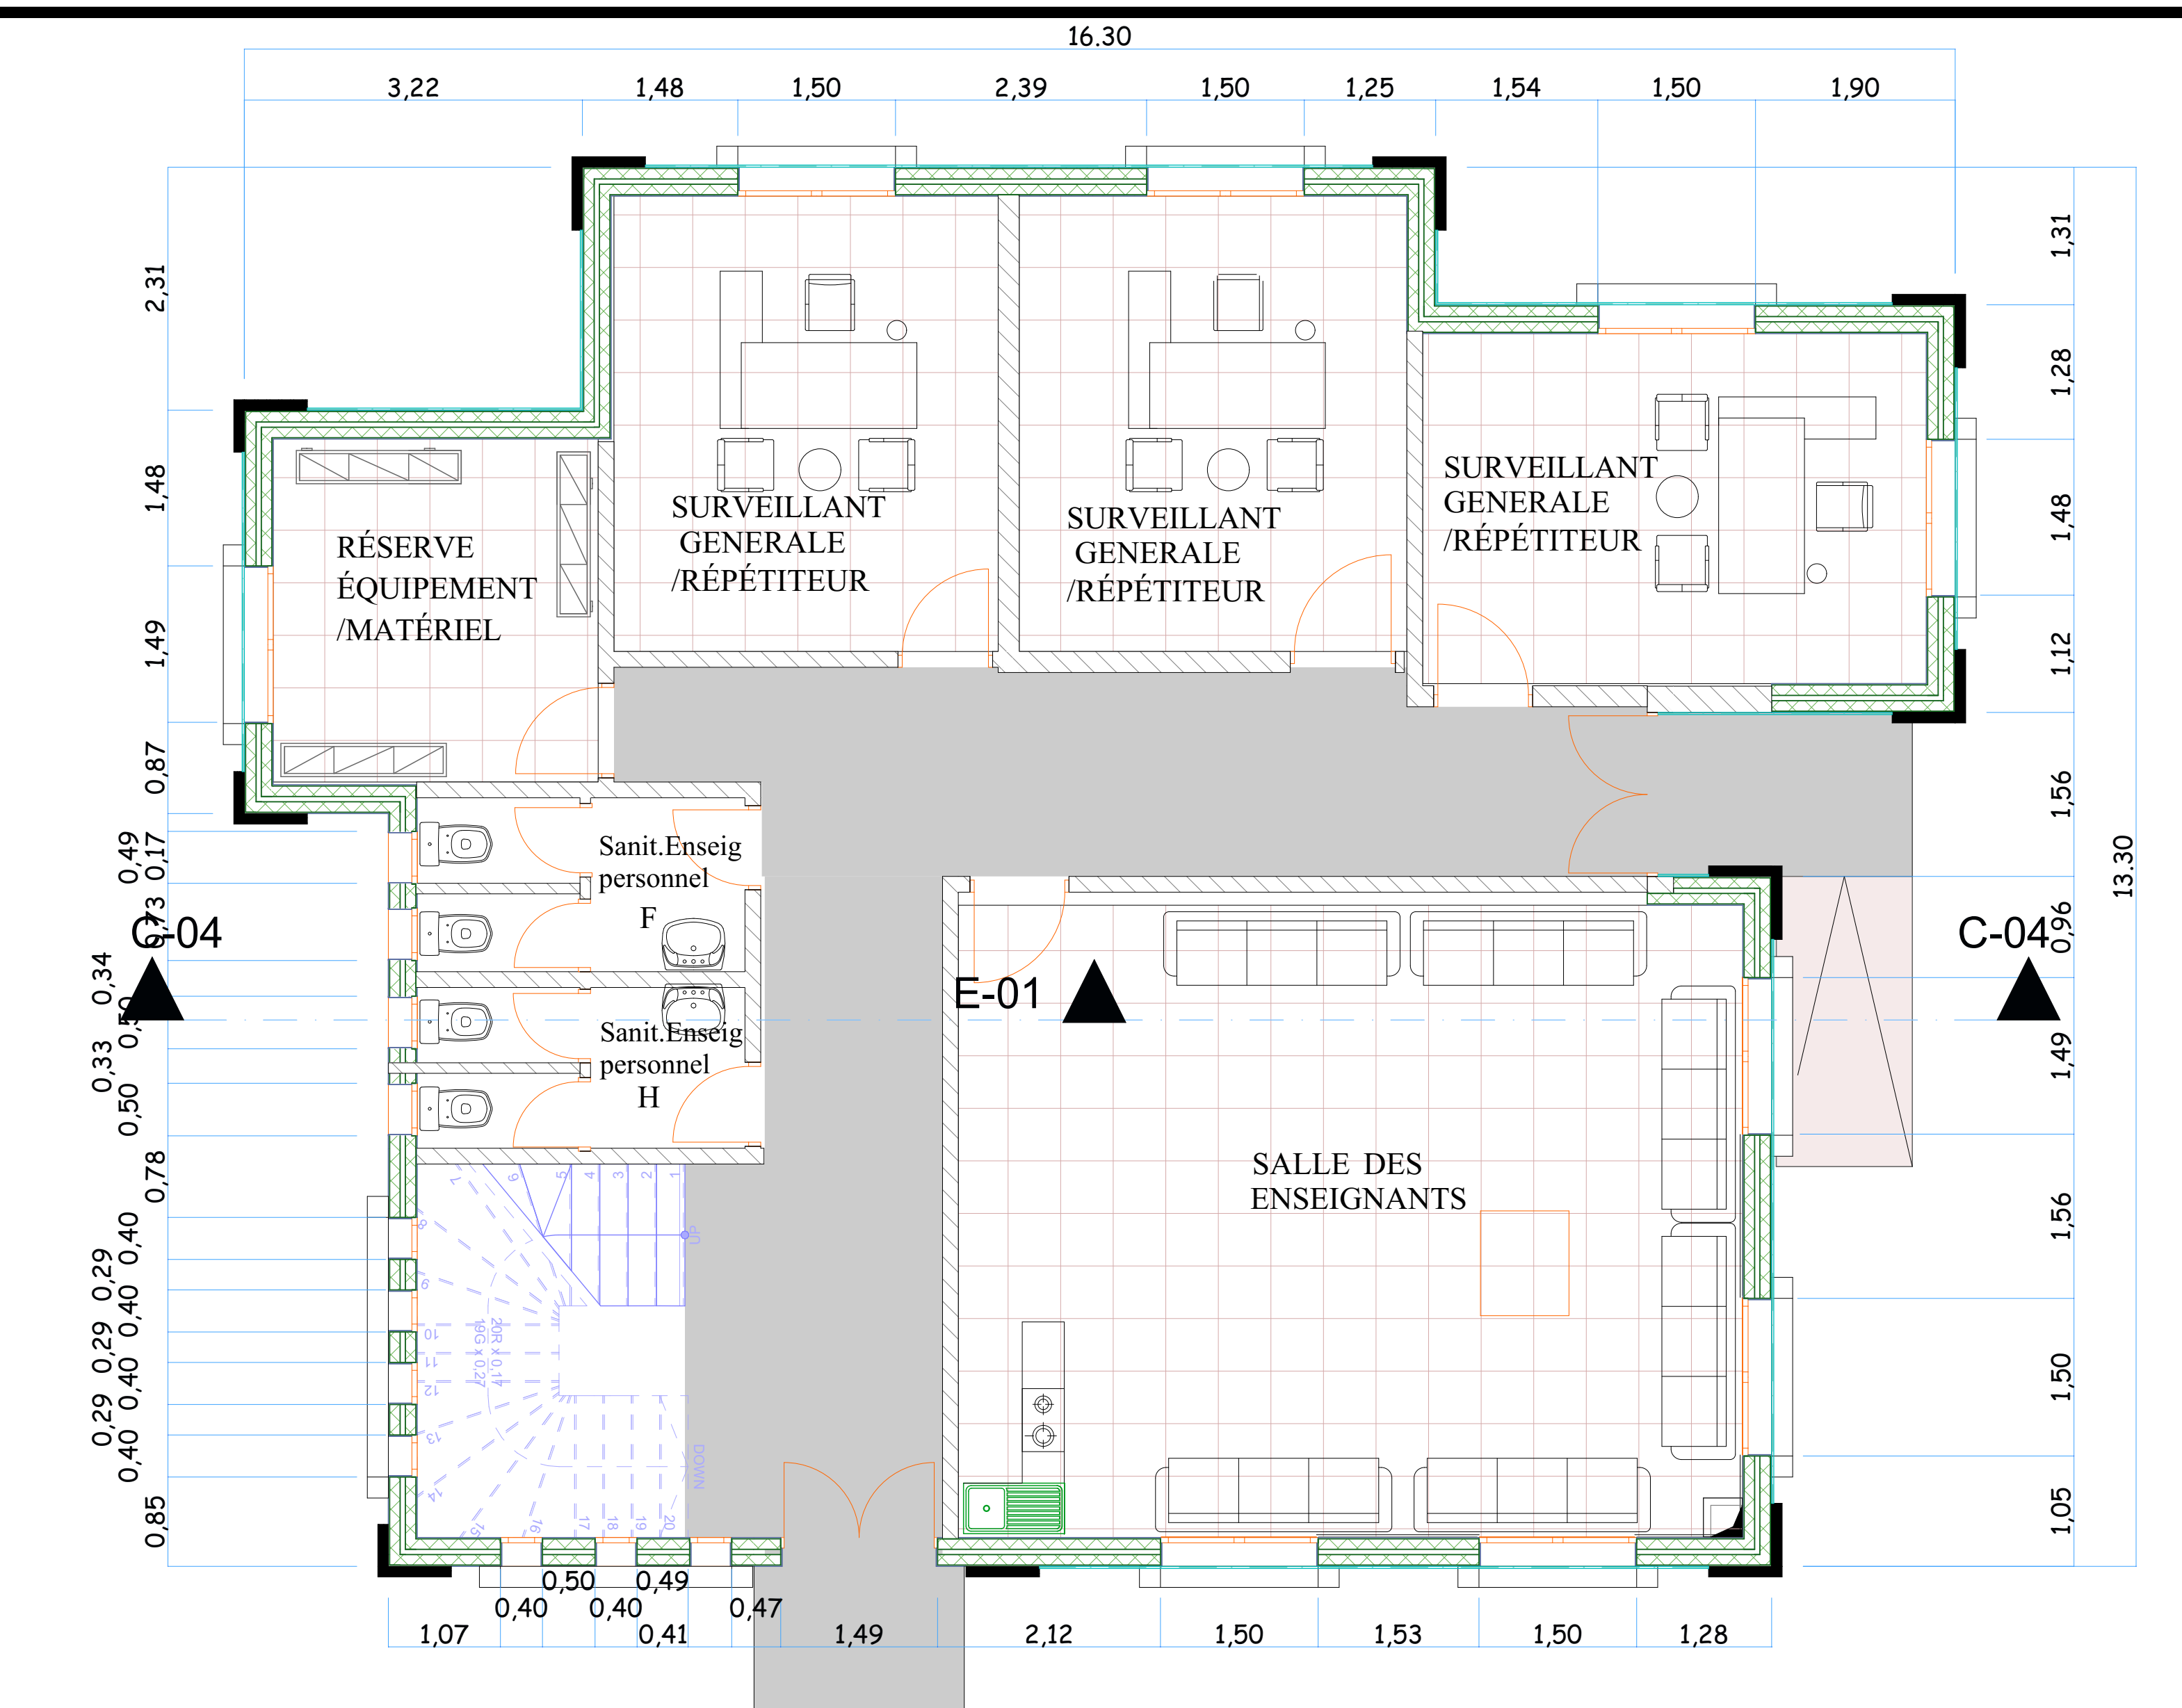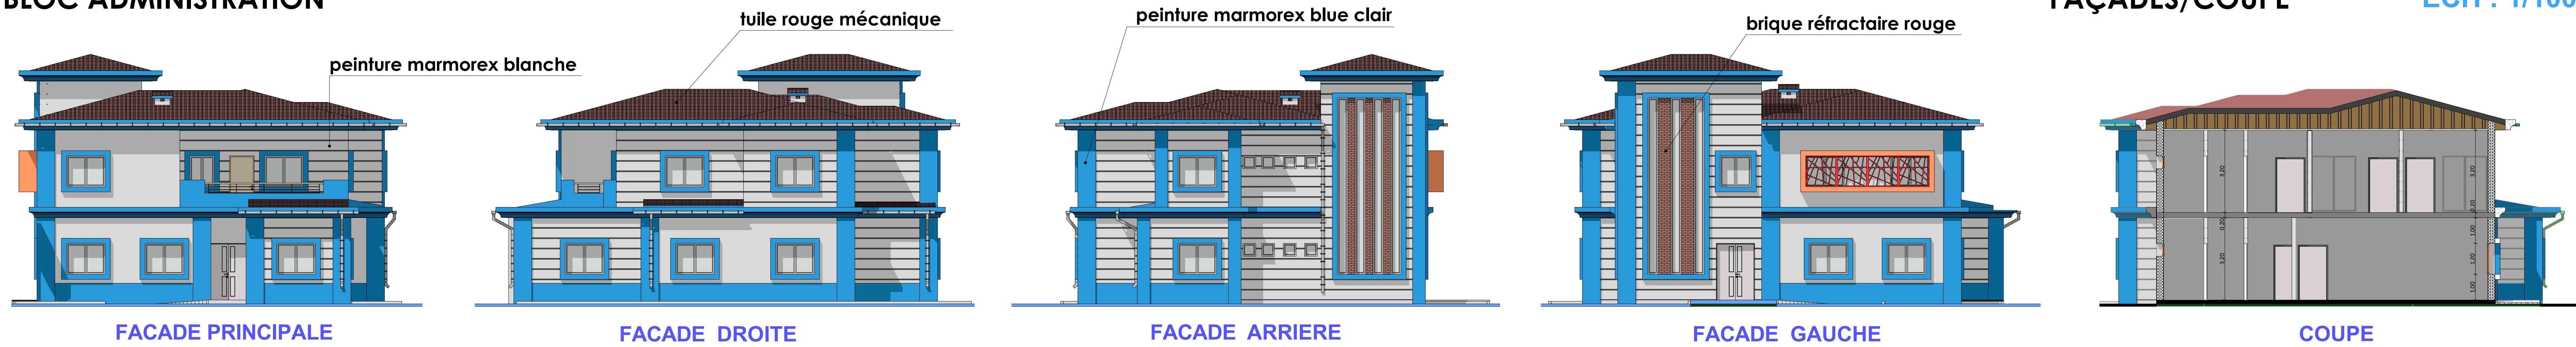

PLAN

REZ DE CHAUSSEE

ECH : 1/50

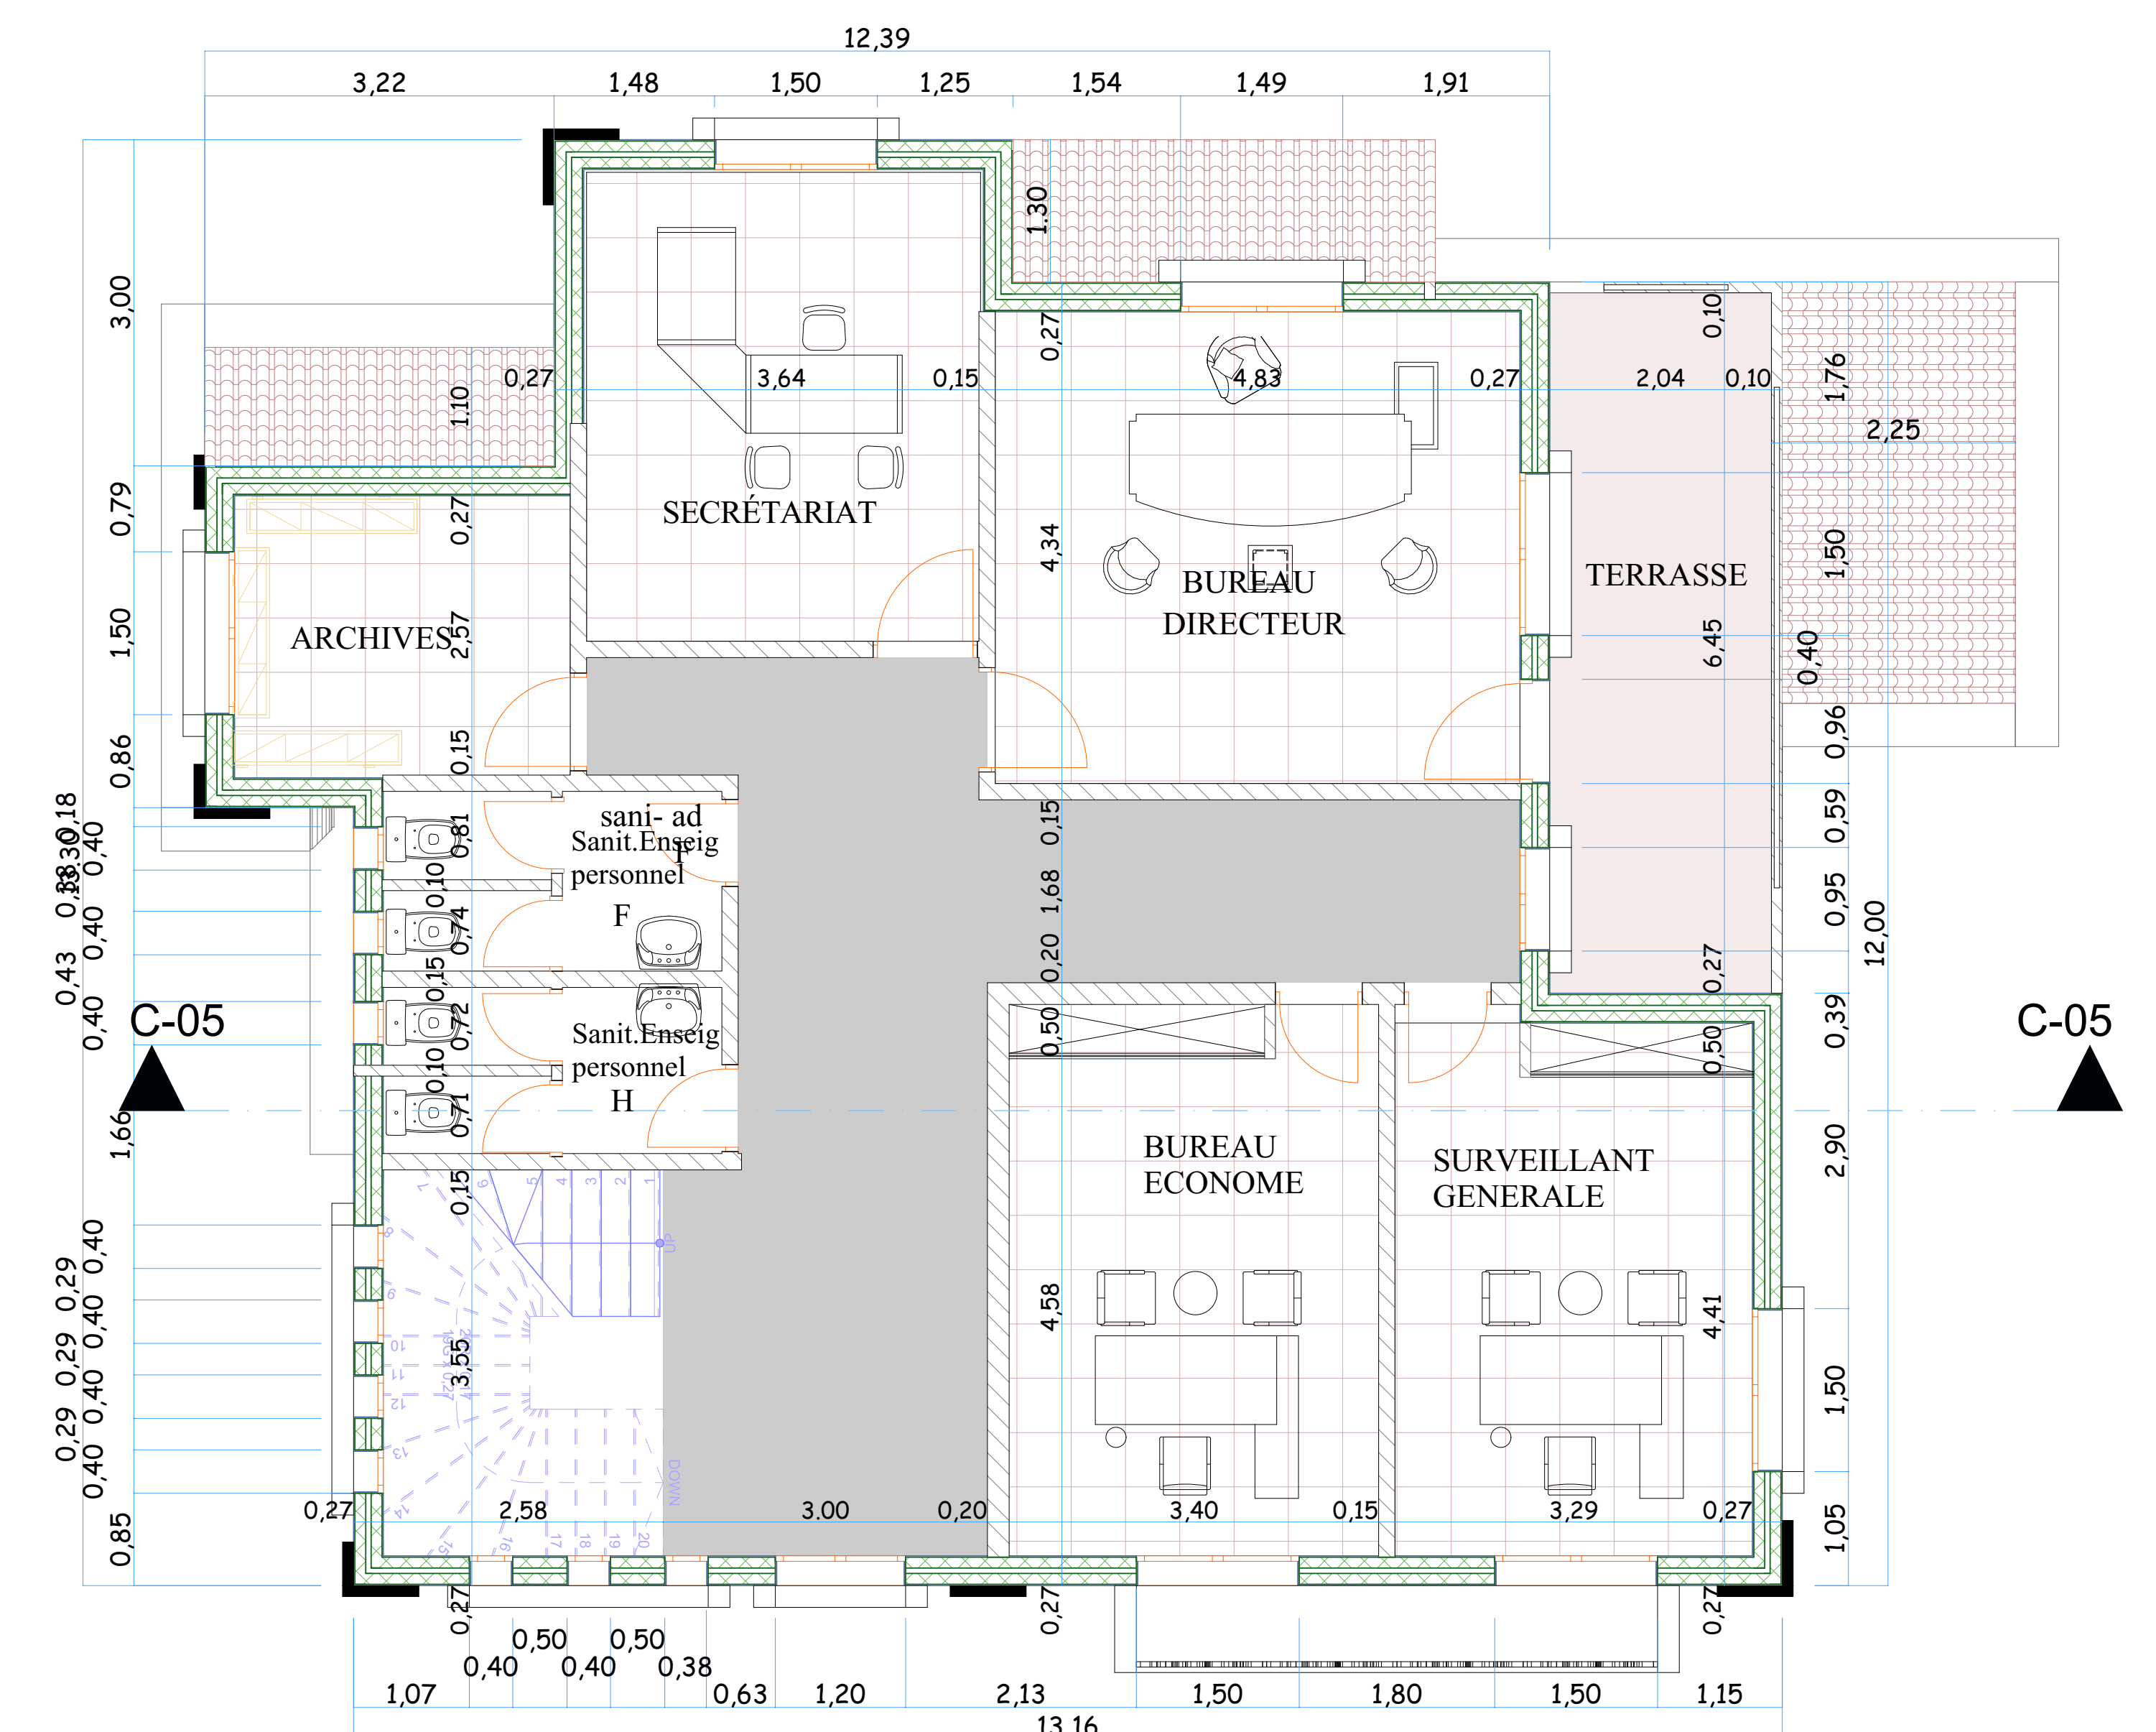

PLAN

ETAGE

ECH : 1/50

PLAN MASSE - SITUATION



VUE D'AMBIANCE SUR BLOC ADMINISTRATION



VUE D'AMBIANCE SUR BLOC ADMINISTRATION



VUE D'AMBIANCE GLOBALE




BLOC ADMINISTRATION

FAÇADES / COUPE / PLANS / PLAN DE MASSE - SITUATION / VUES D'AMBIANCES



MY ABDELAZIZ EL HARRANE ARCHITECTE D.P.L.G

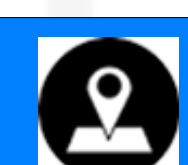

AV Hassan II 1er Etage App N° : 2 Midelt



Email : archiharrane@yahoo.fr



Tel - Fax : 05 35 36 00 79