




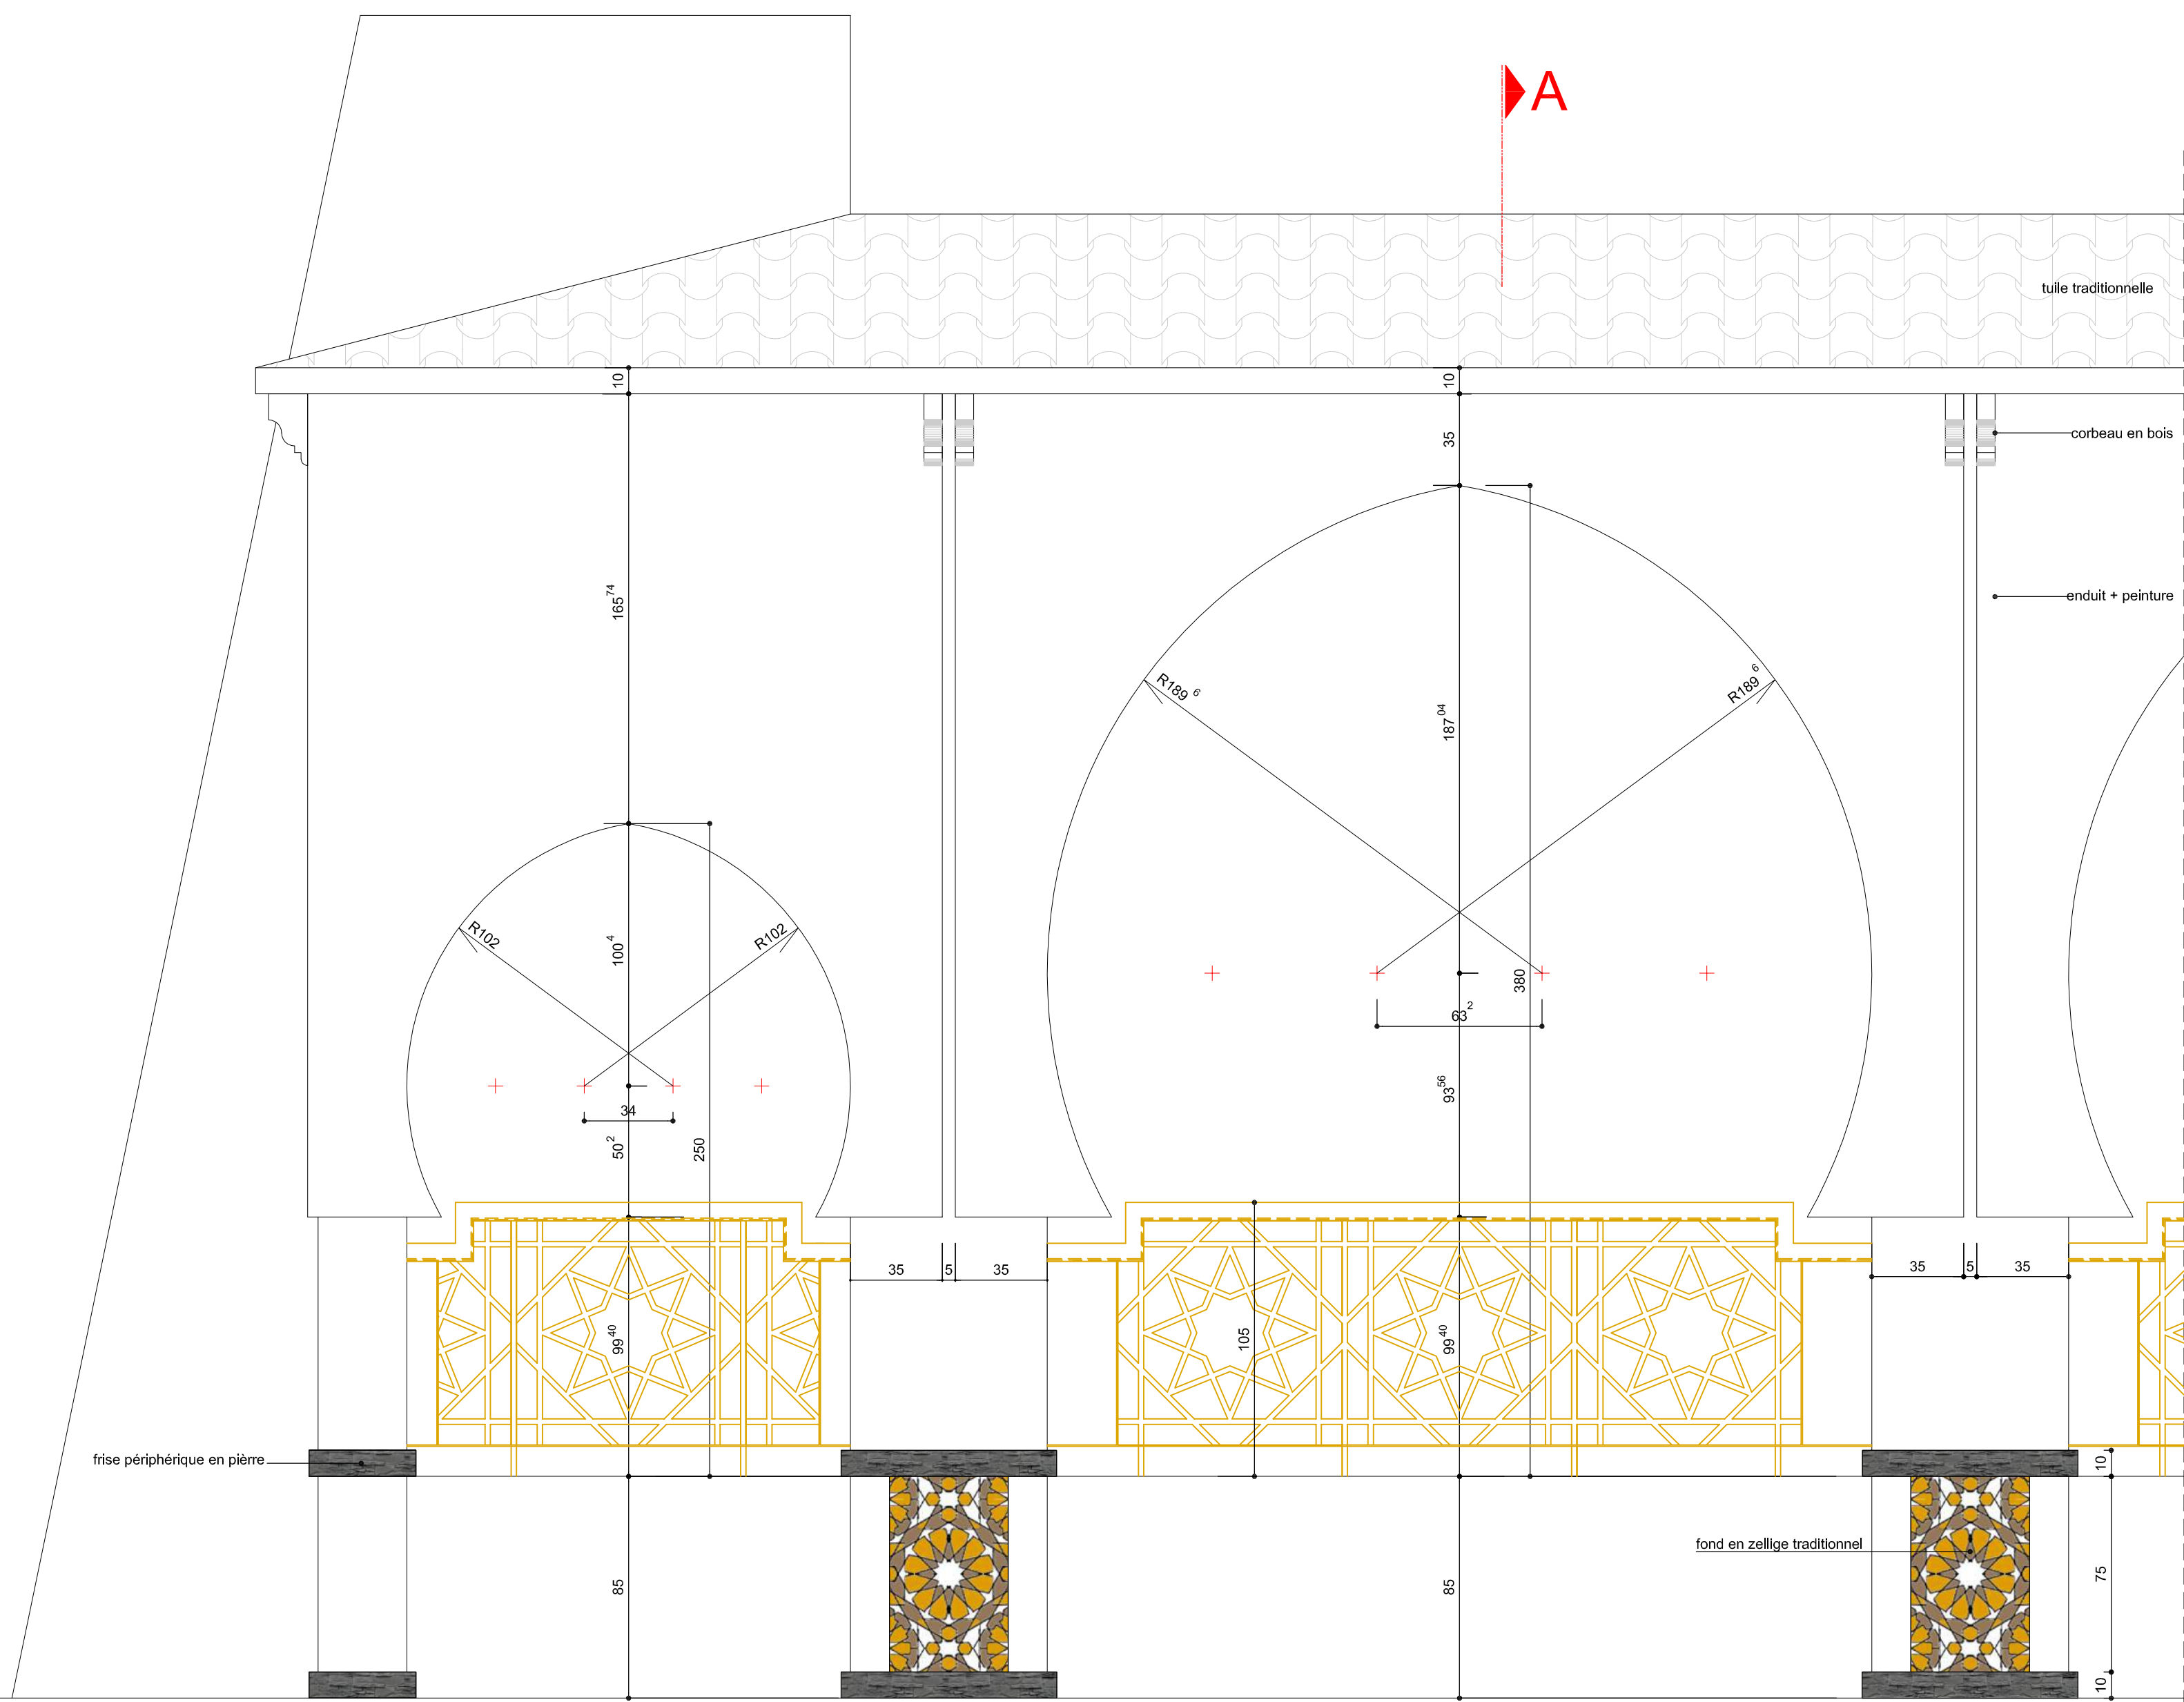


Elévation

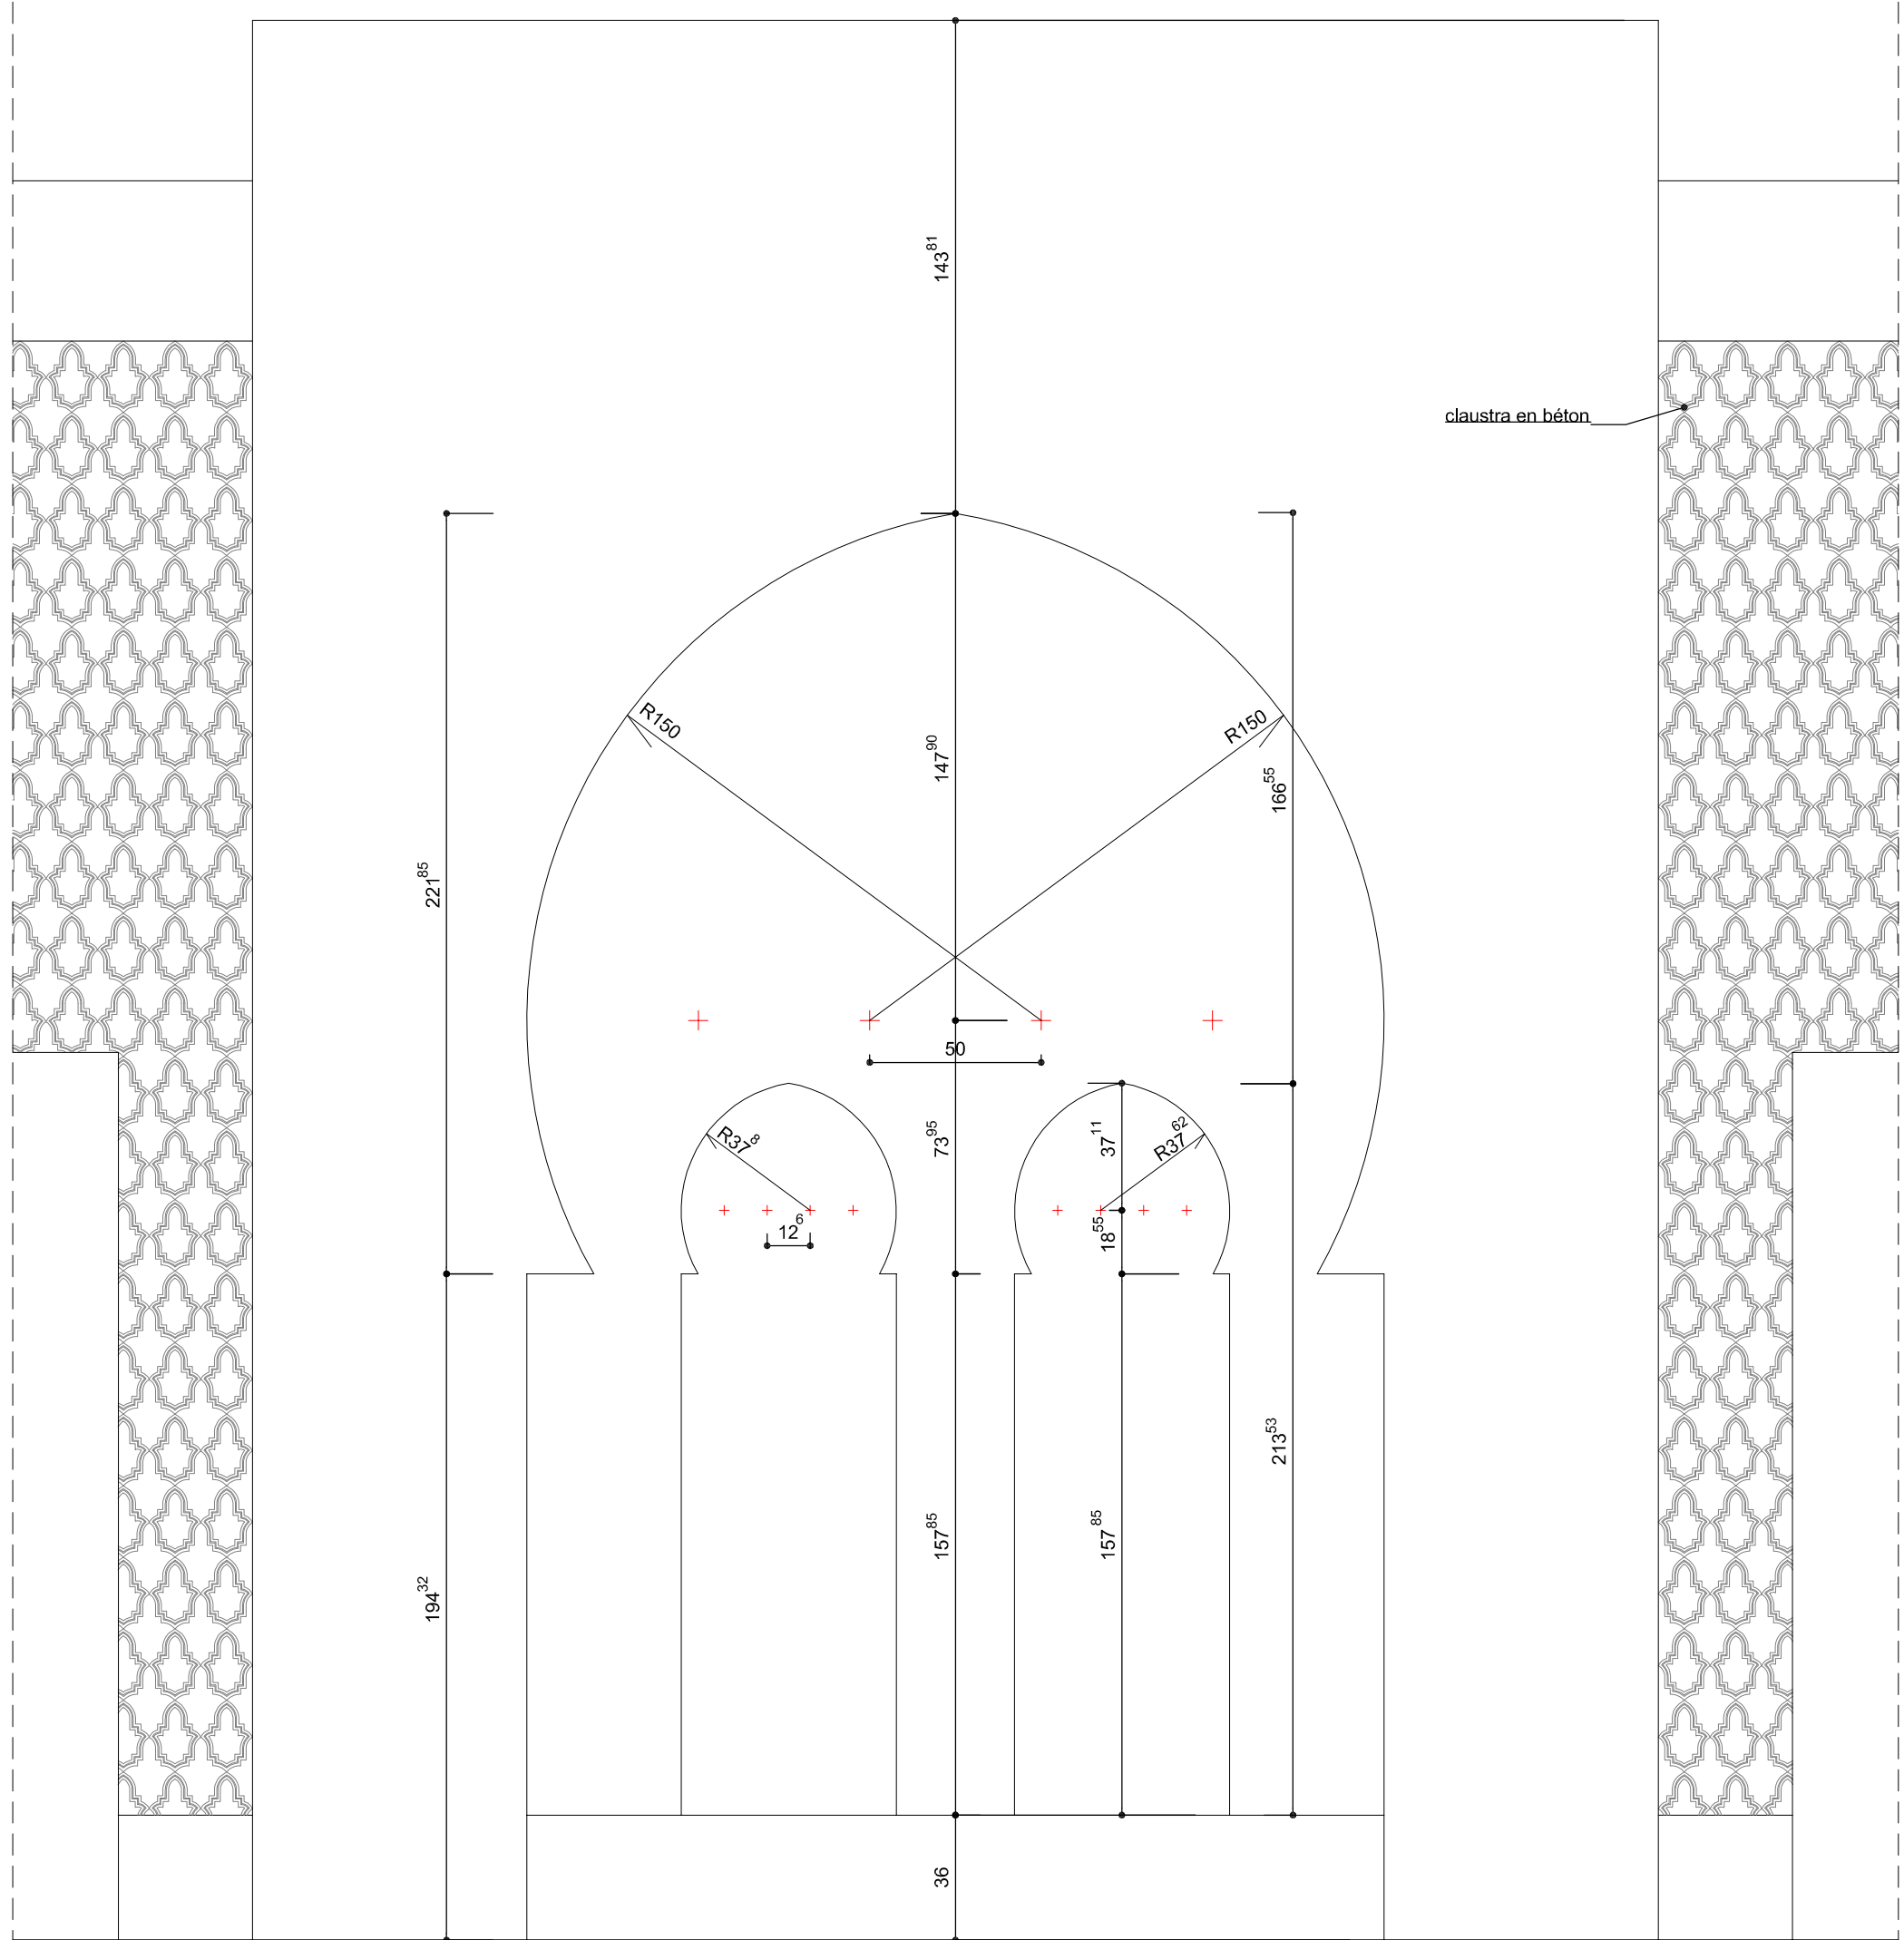


Elévation Entrée Principale

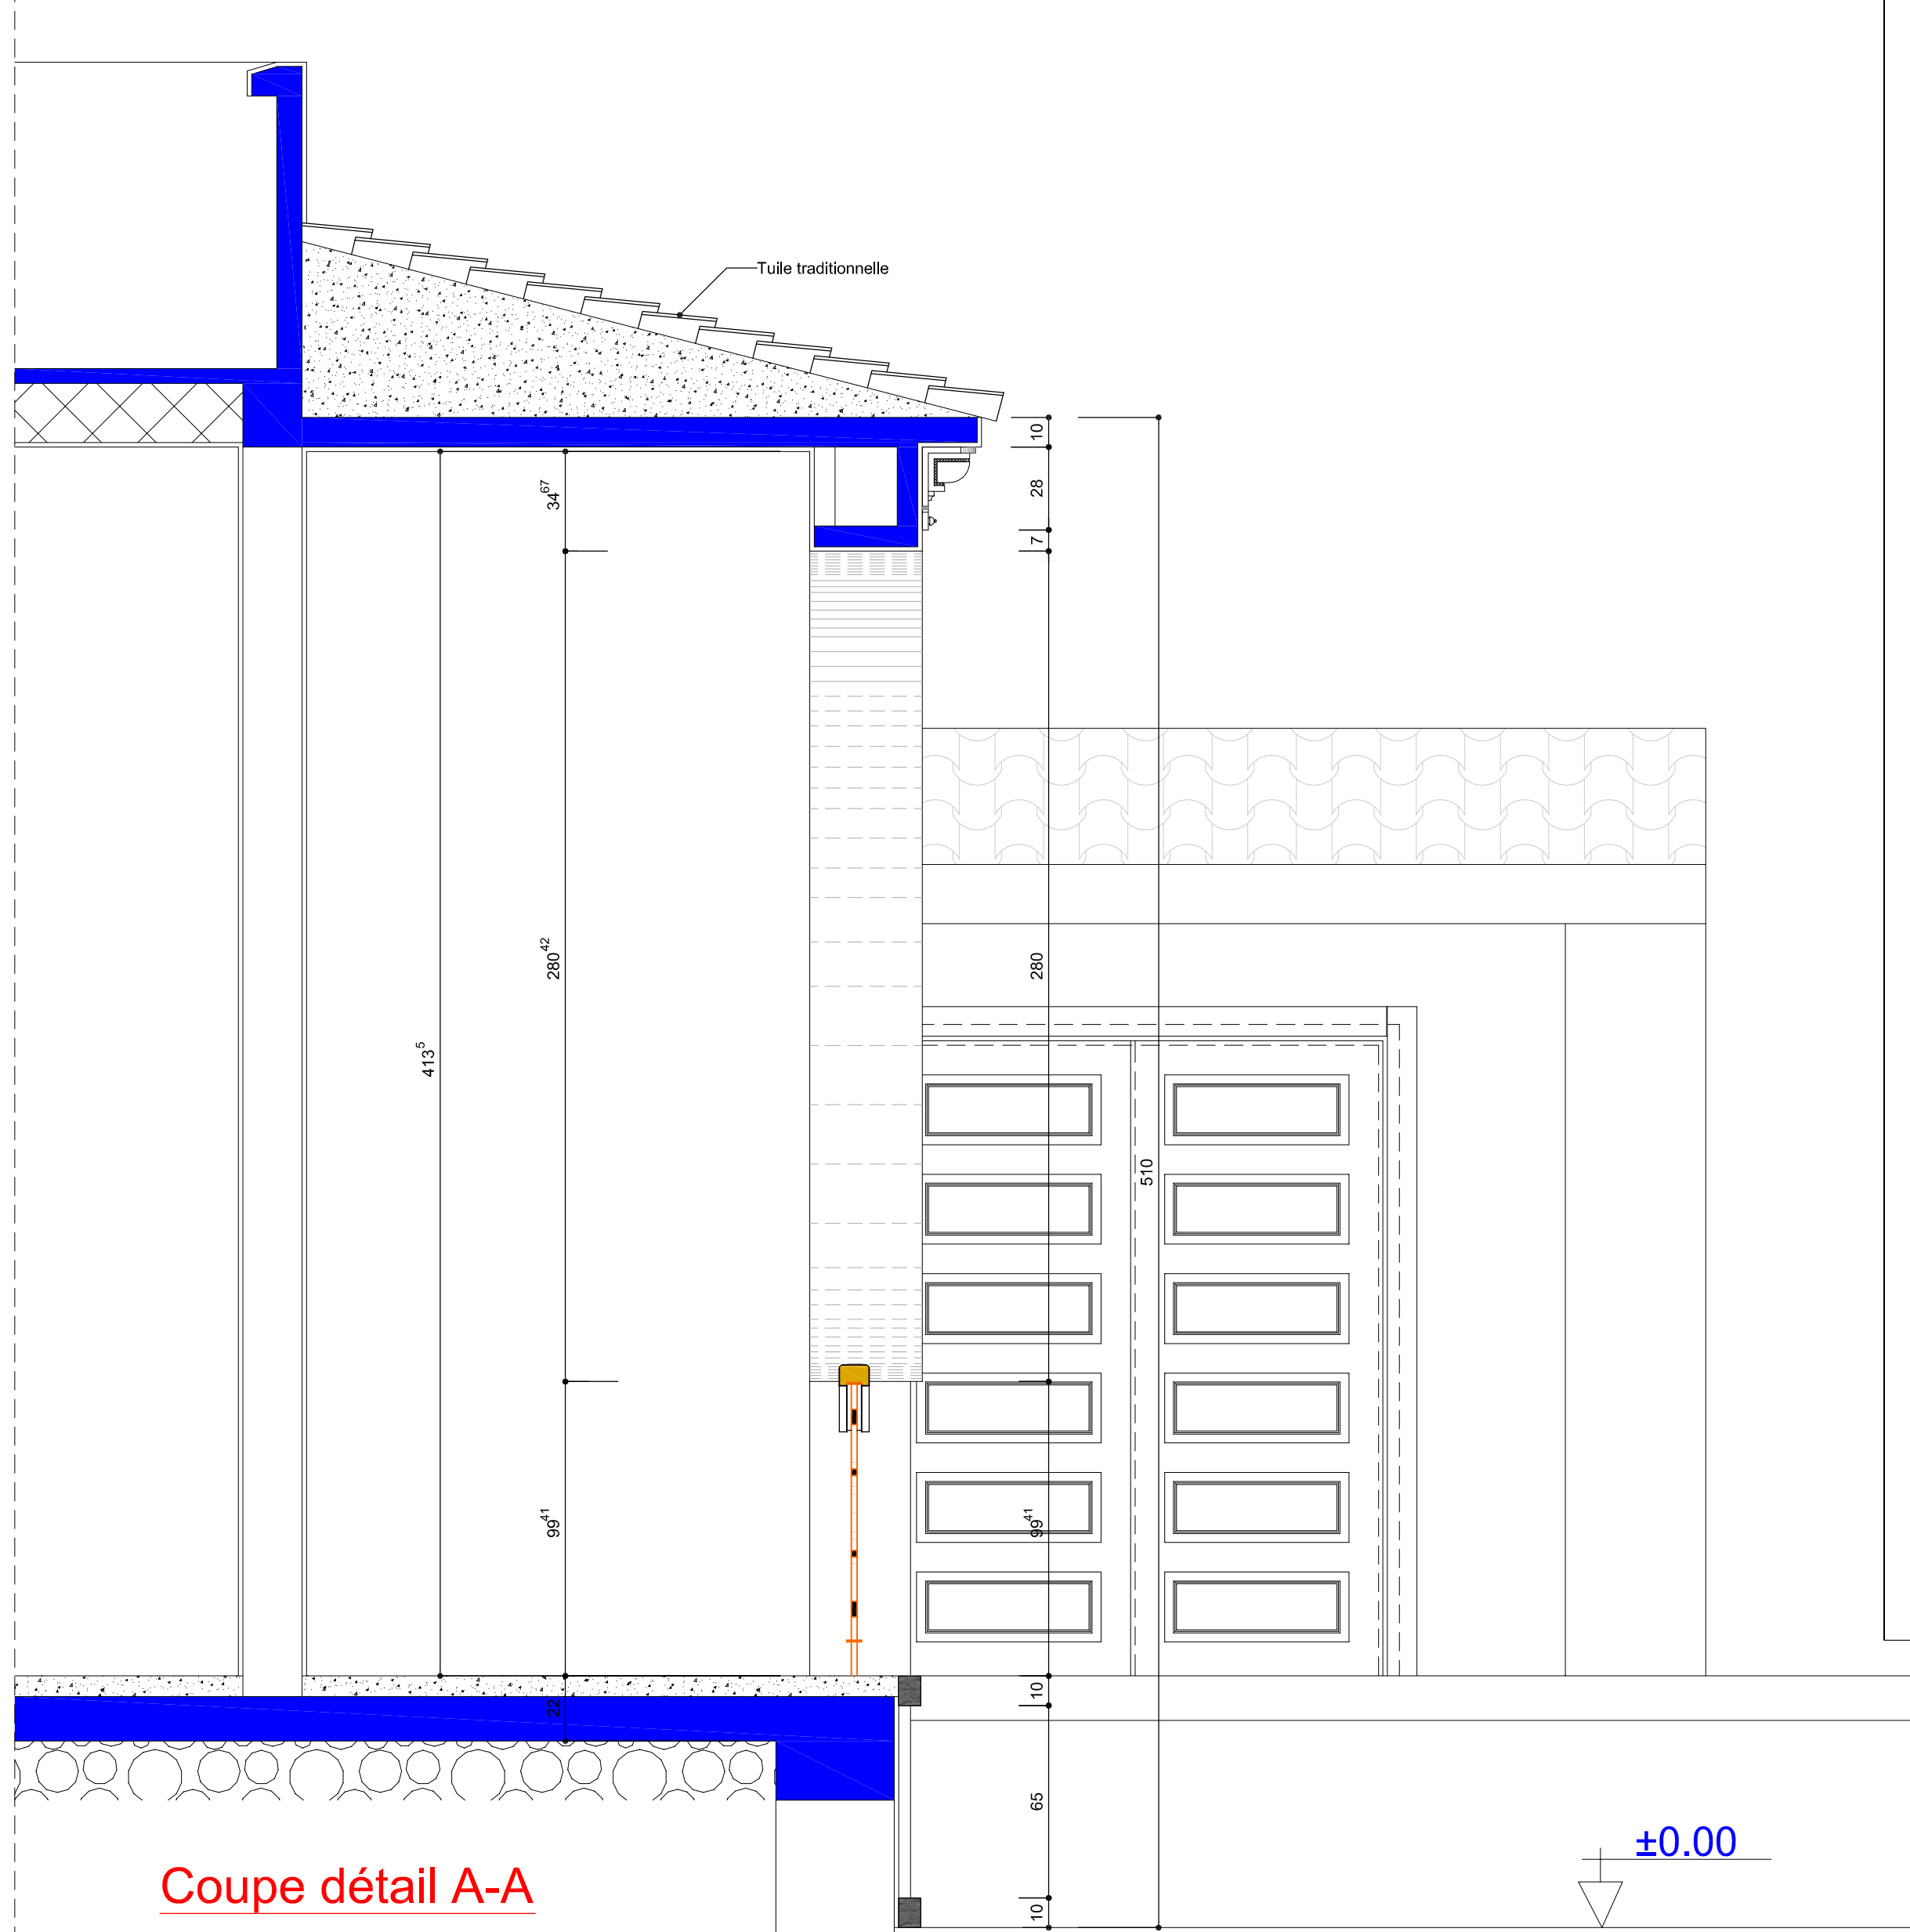


Coupe détail A-A

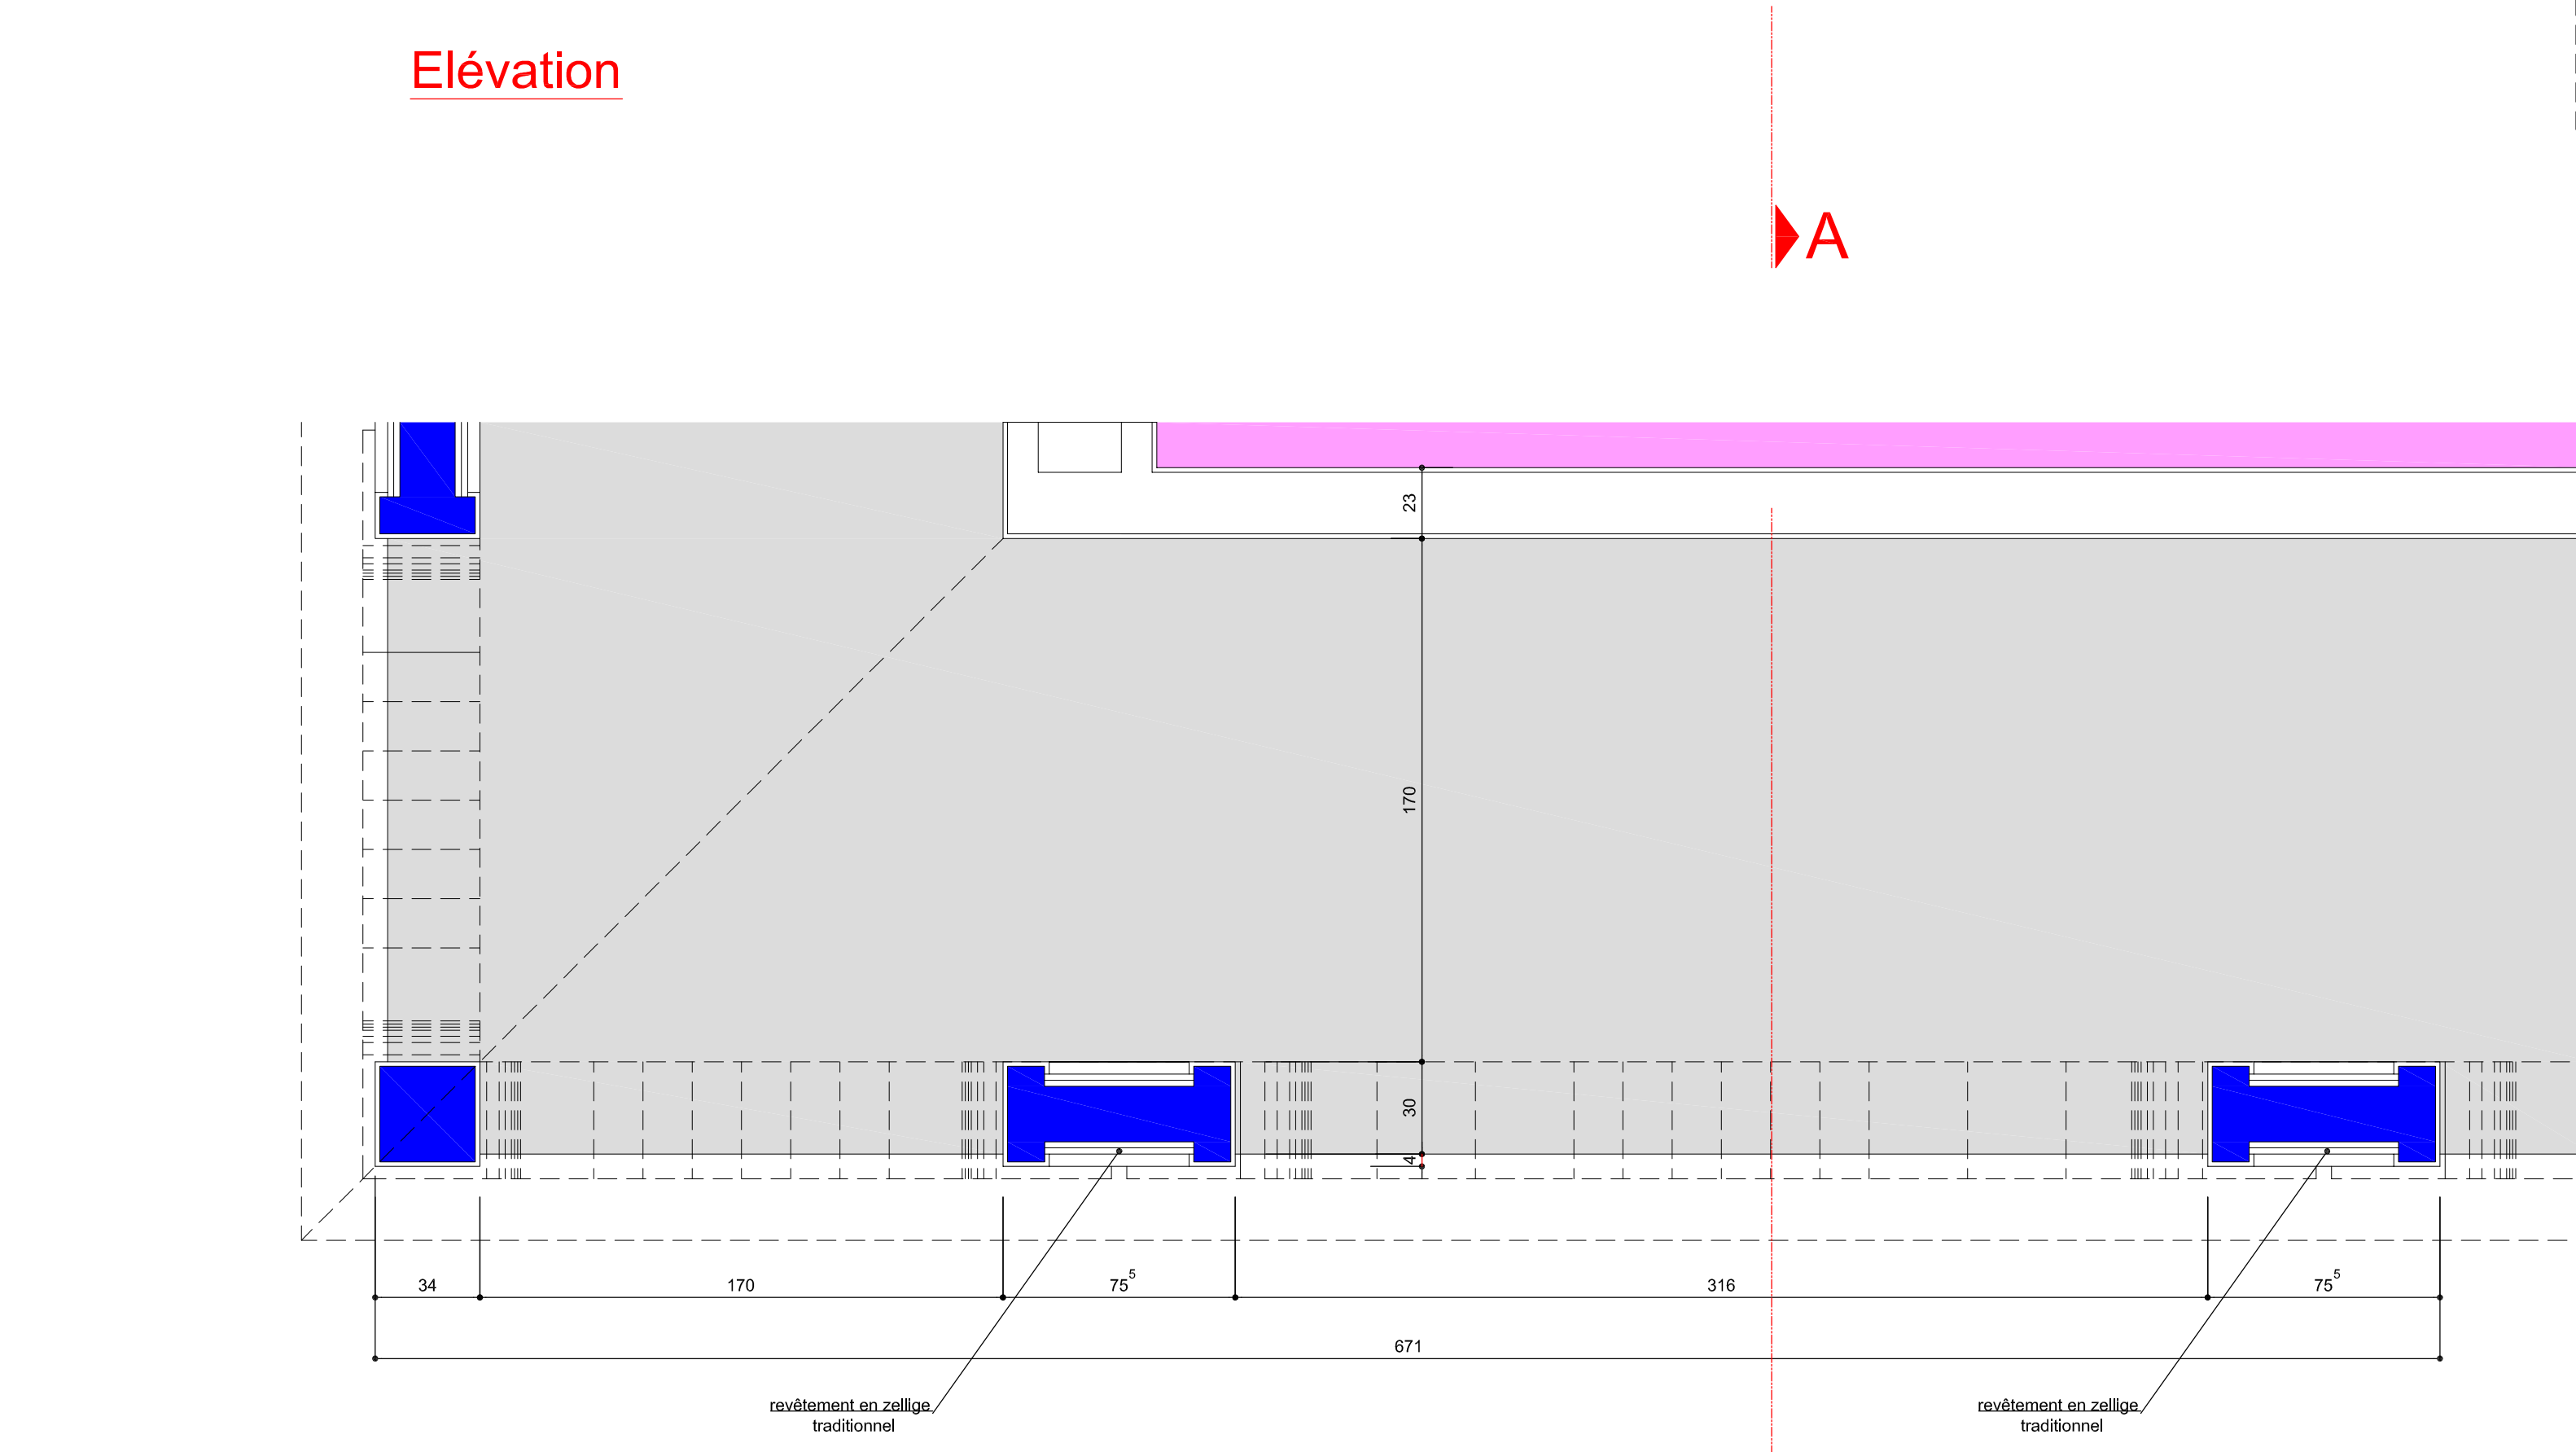


Plan

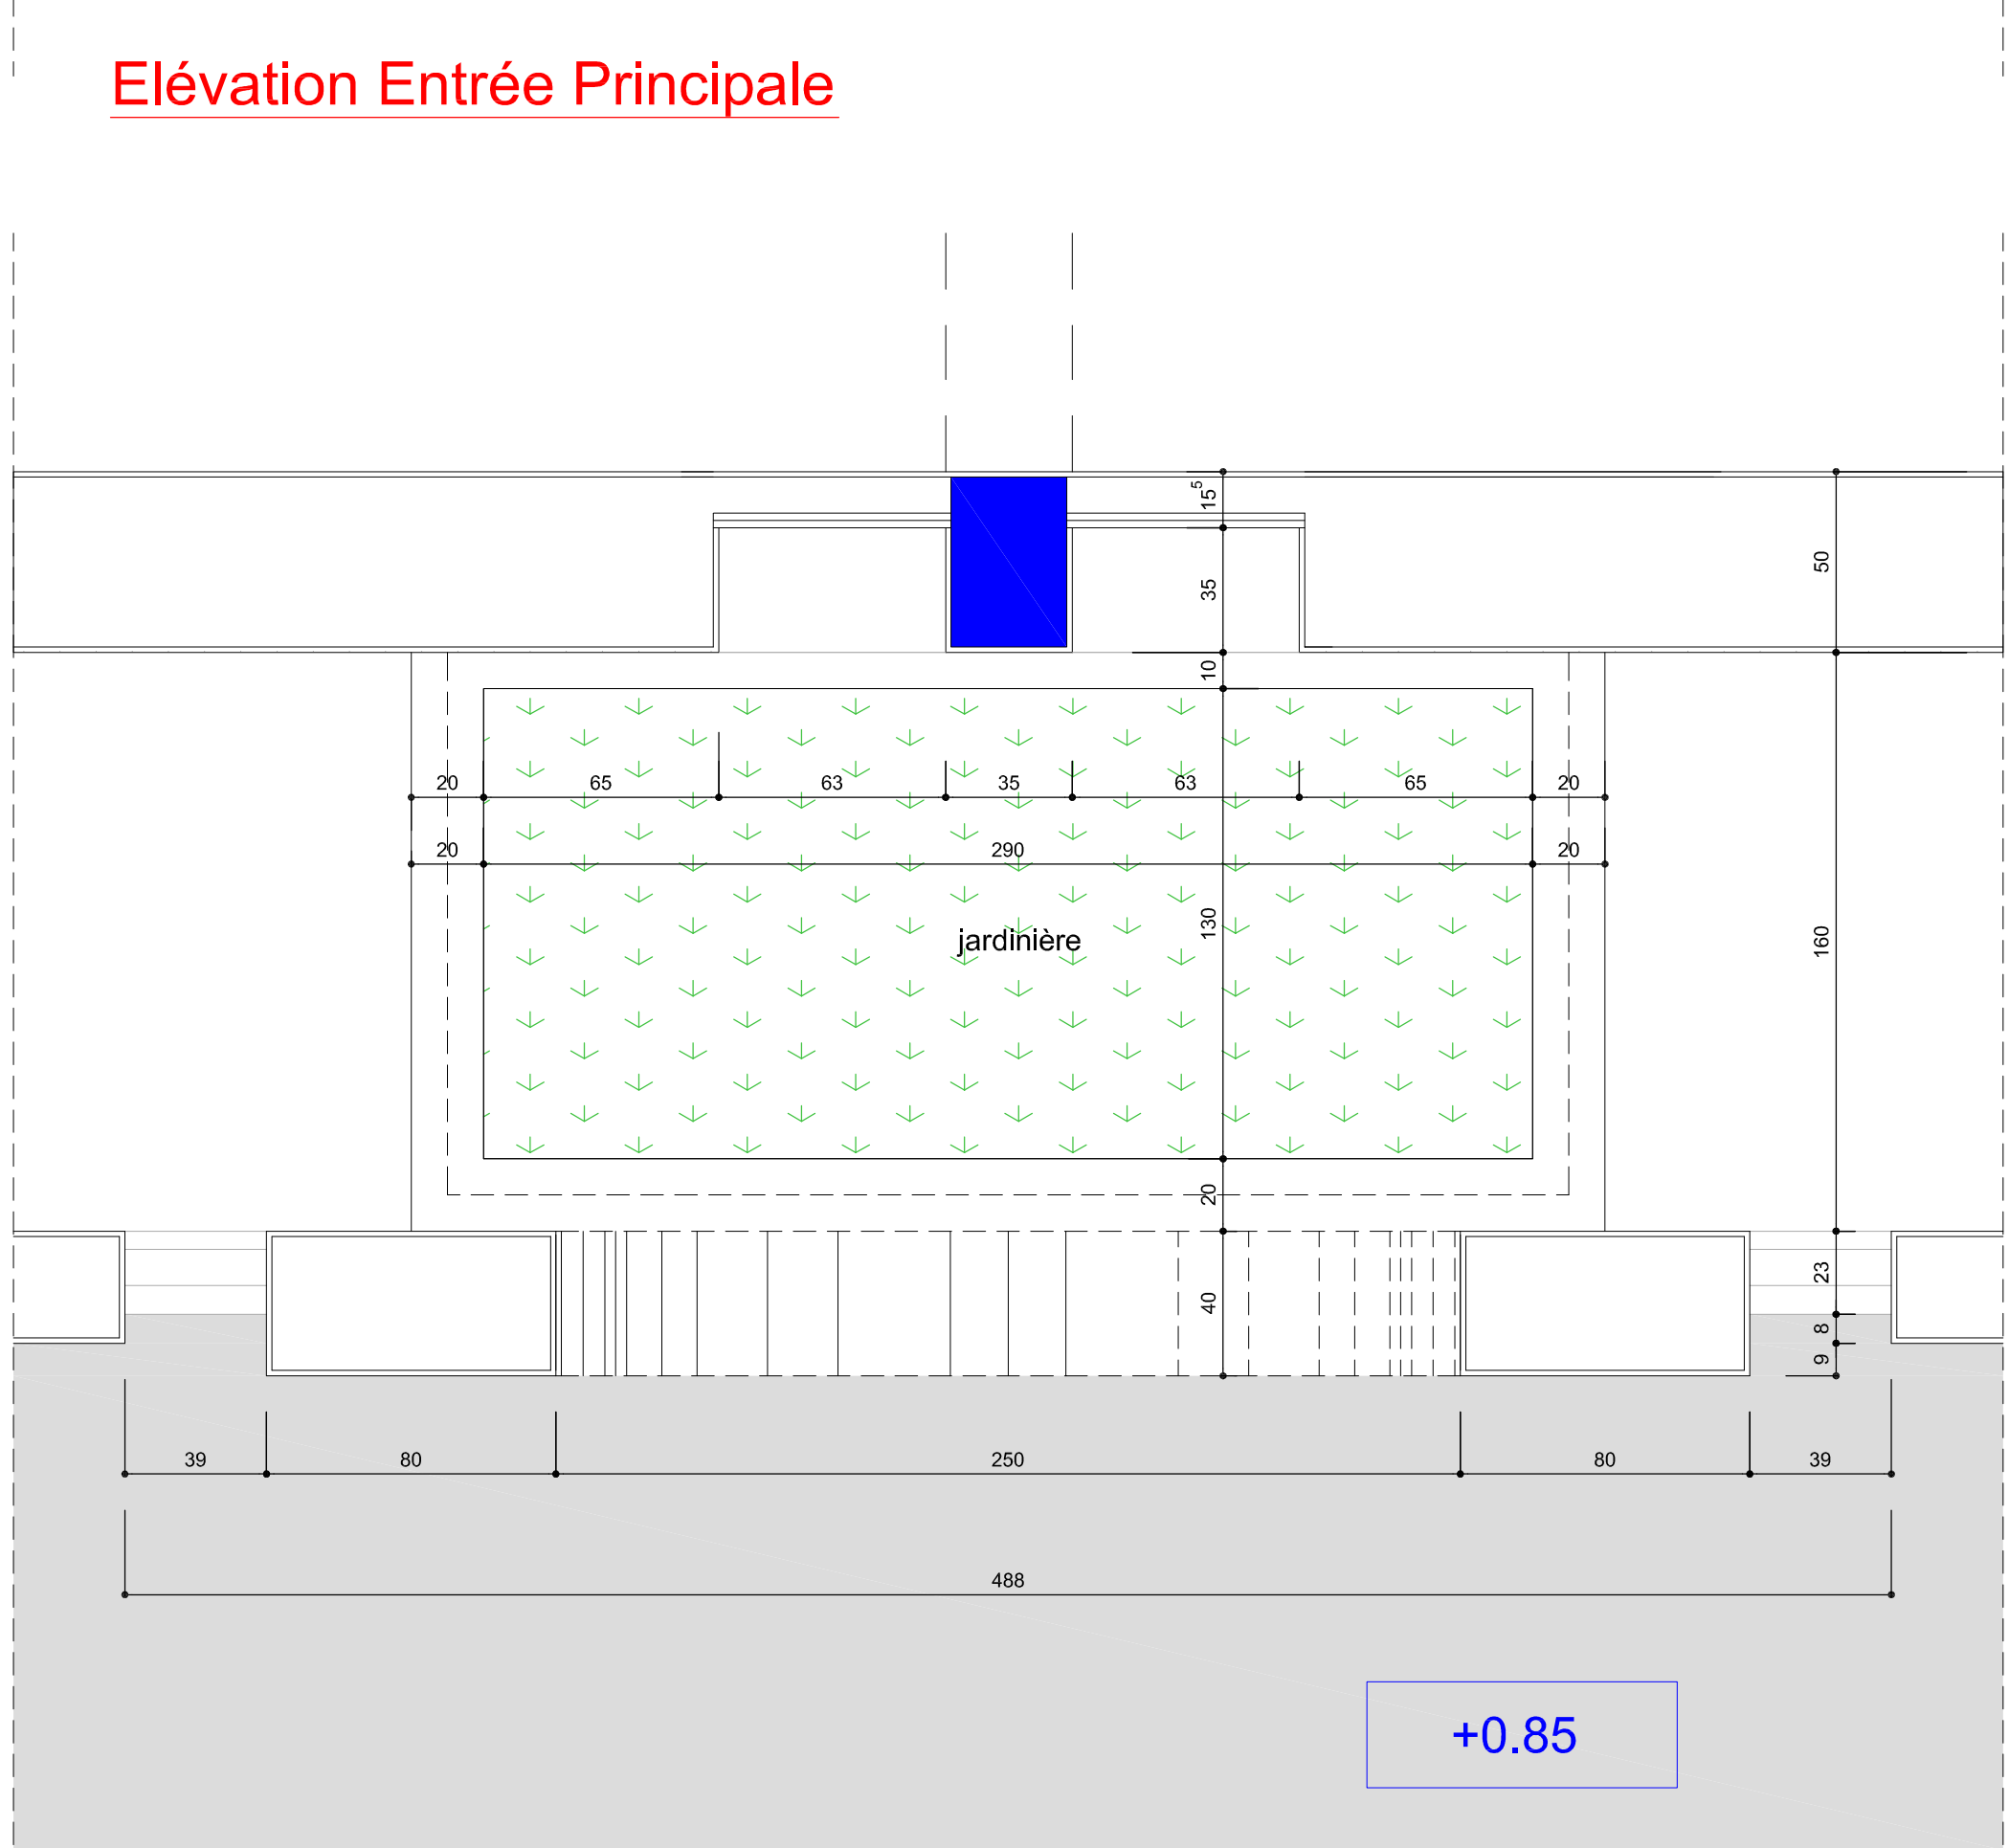


Plan Entrée Principale

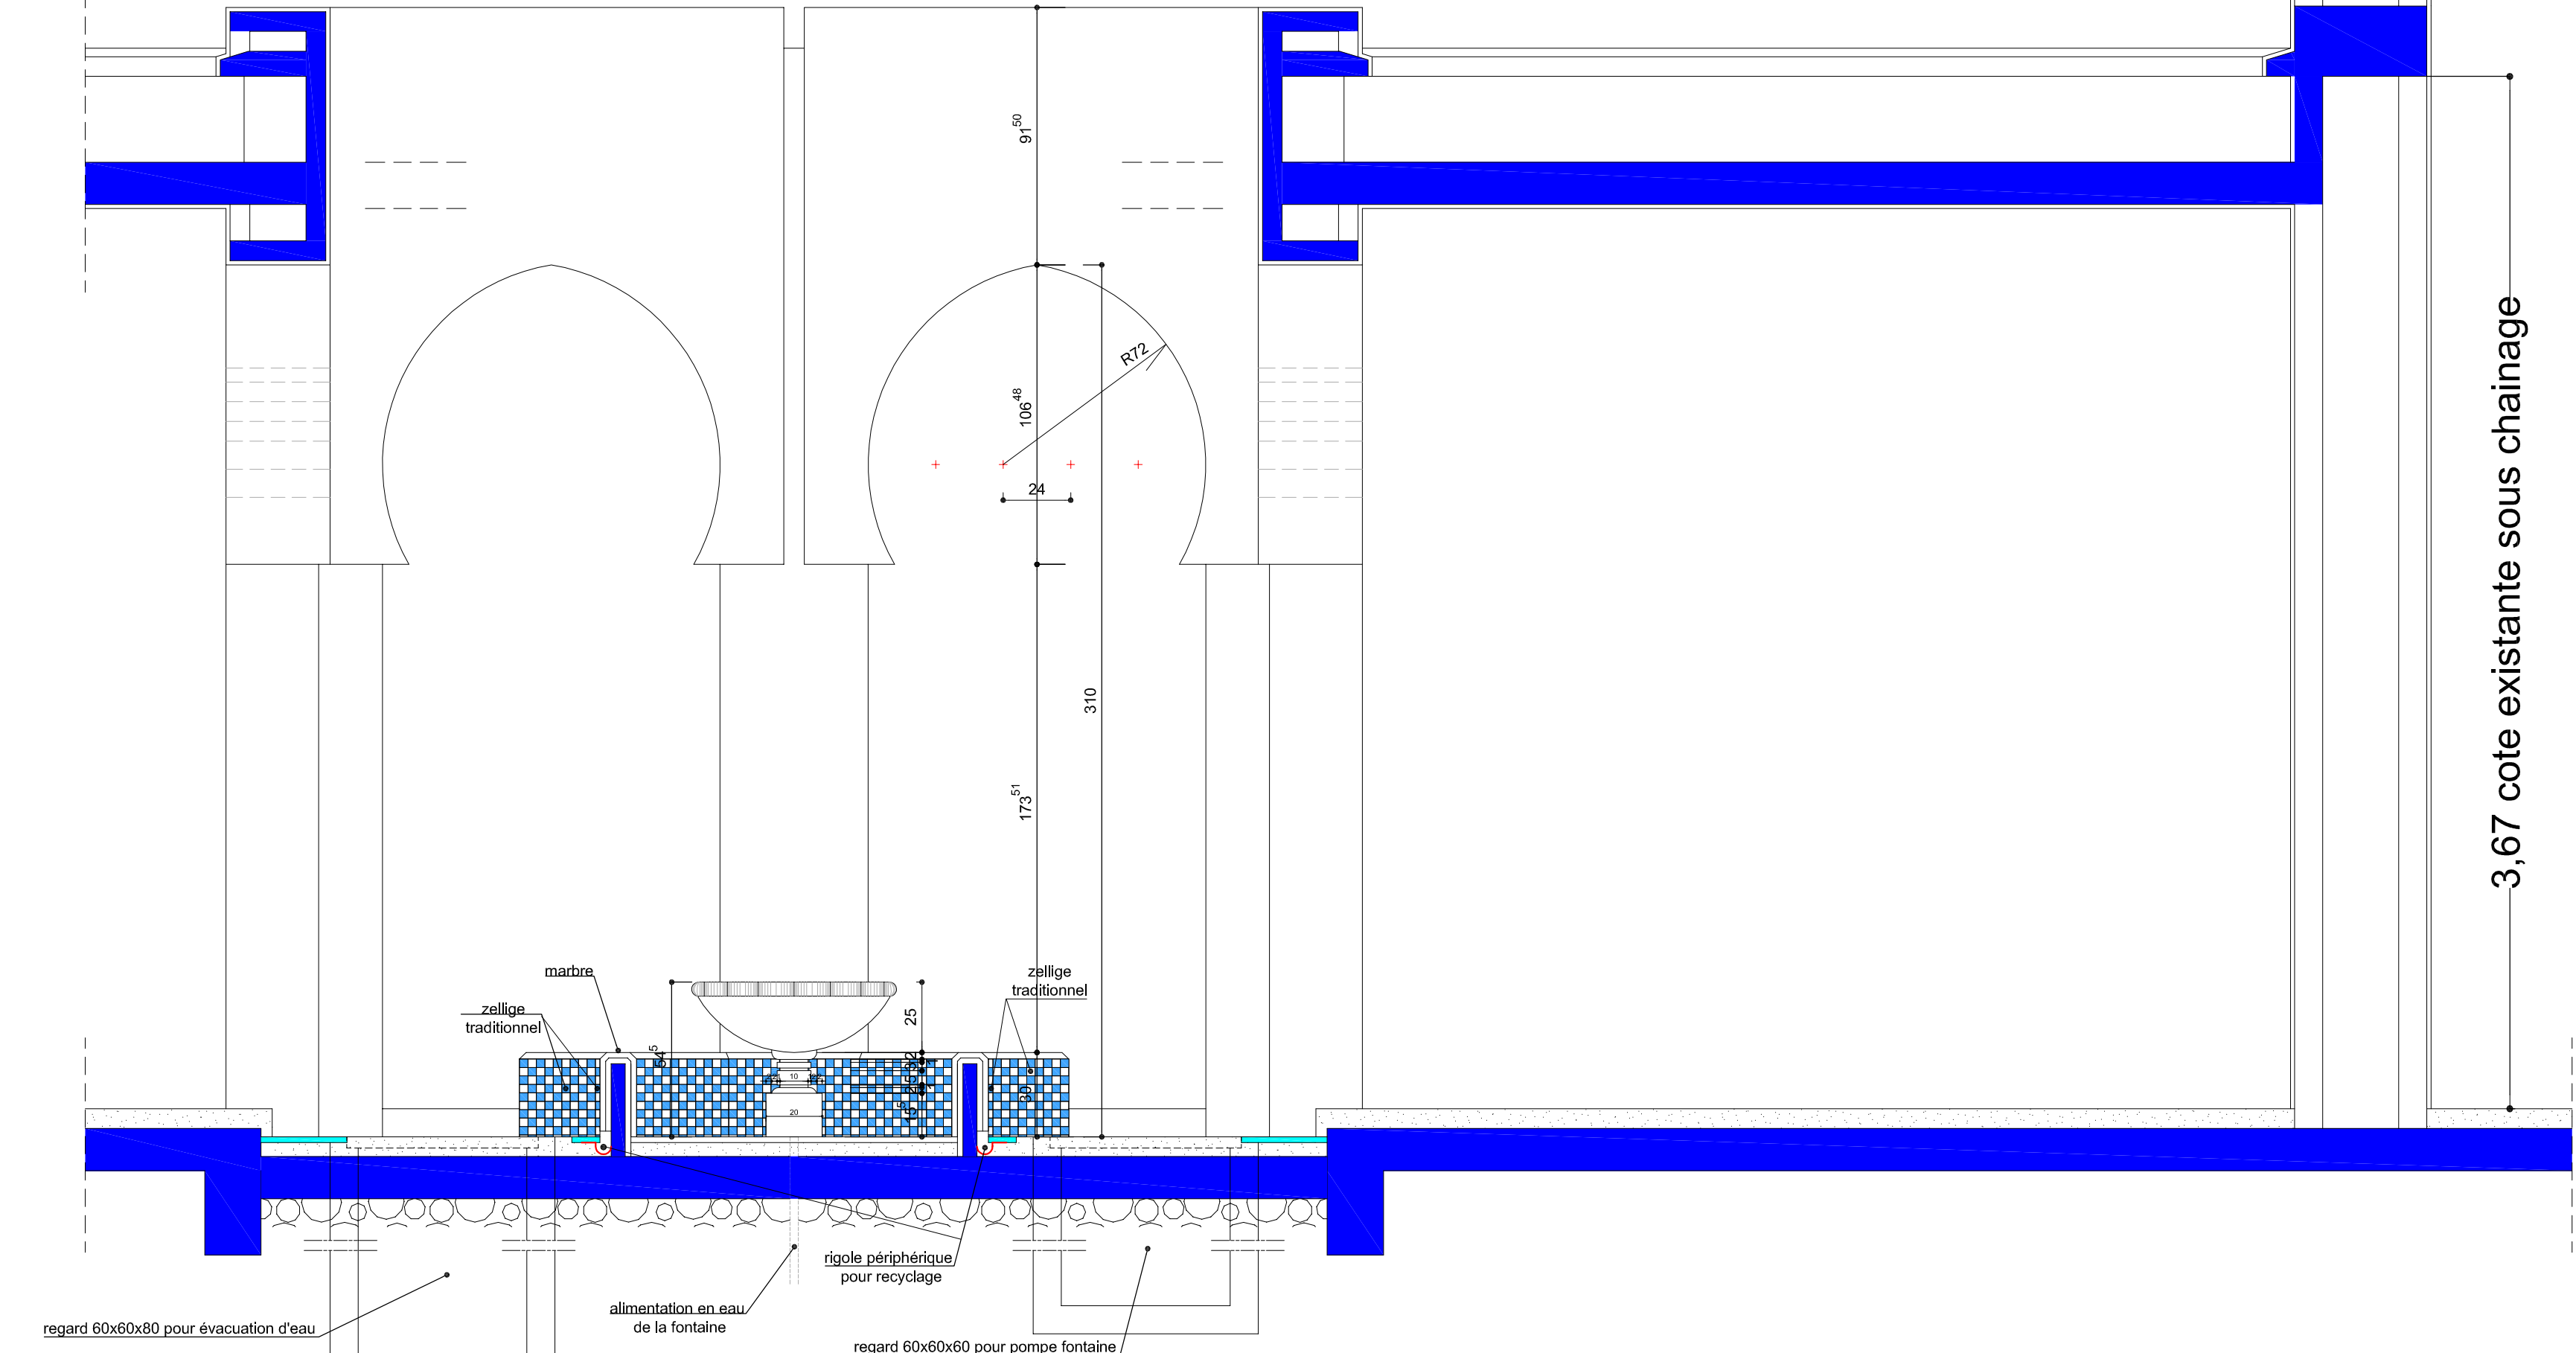


Coupe détail C-C sur fontaine

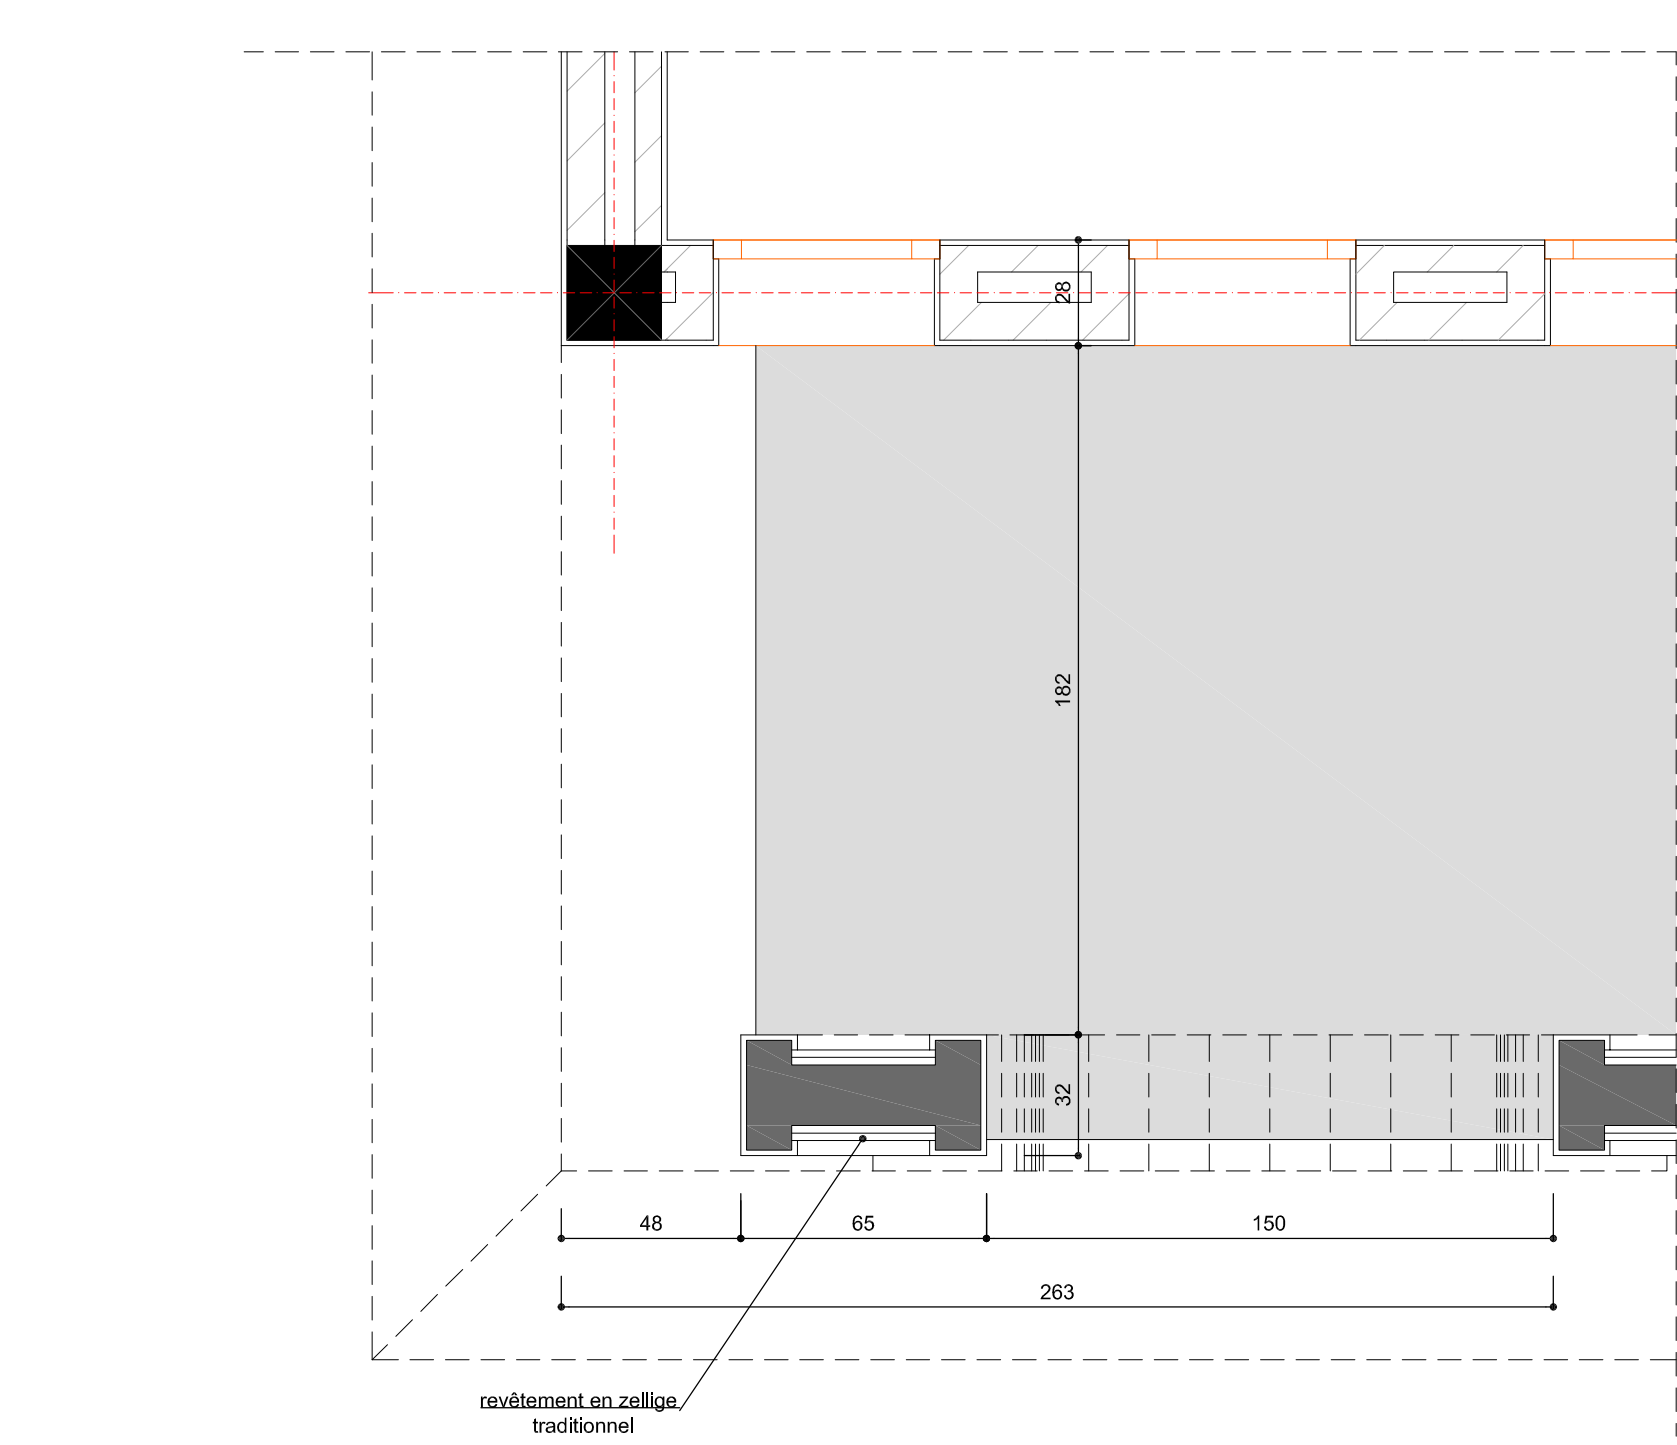

Plan Galerie Administration

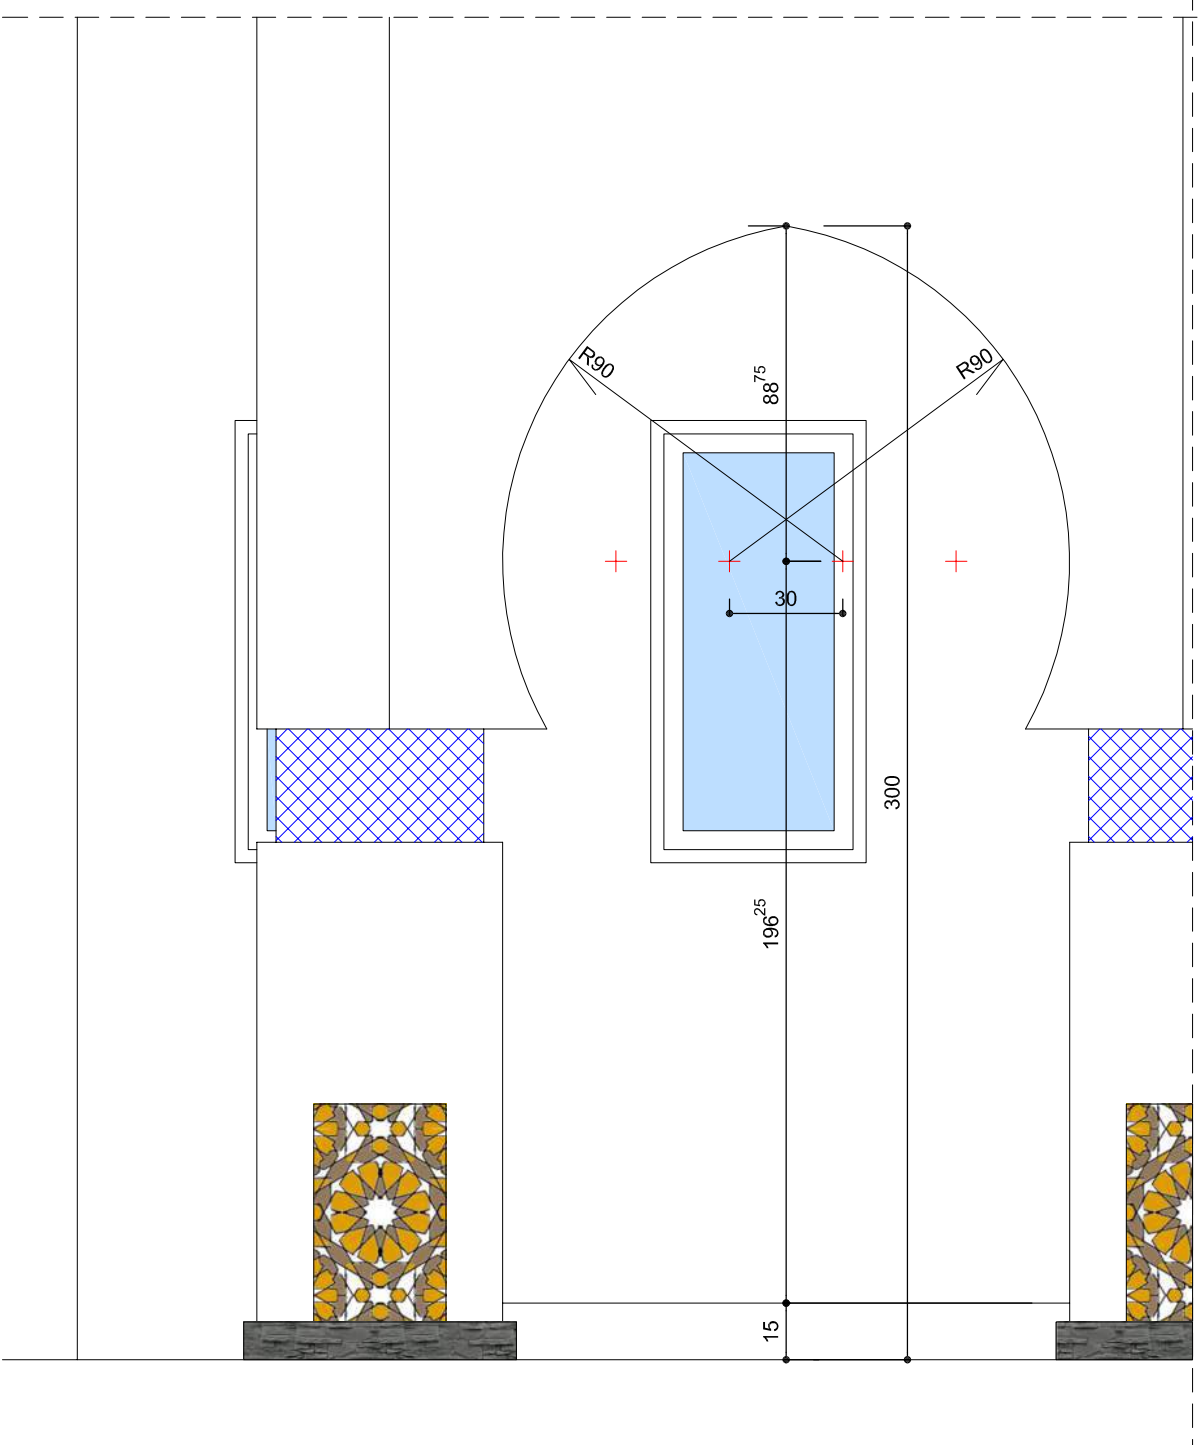


Elévation Galerie Administration

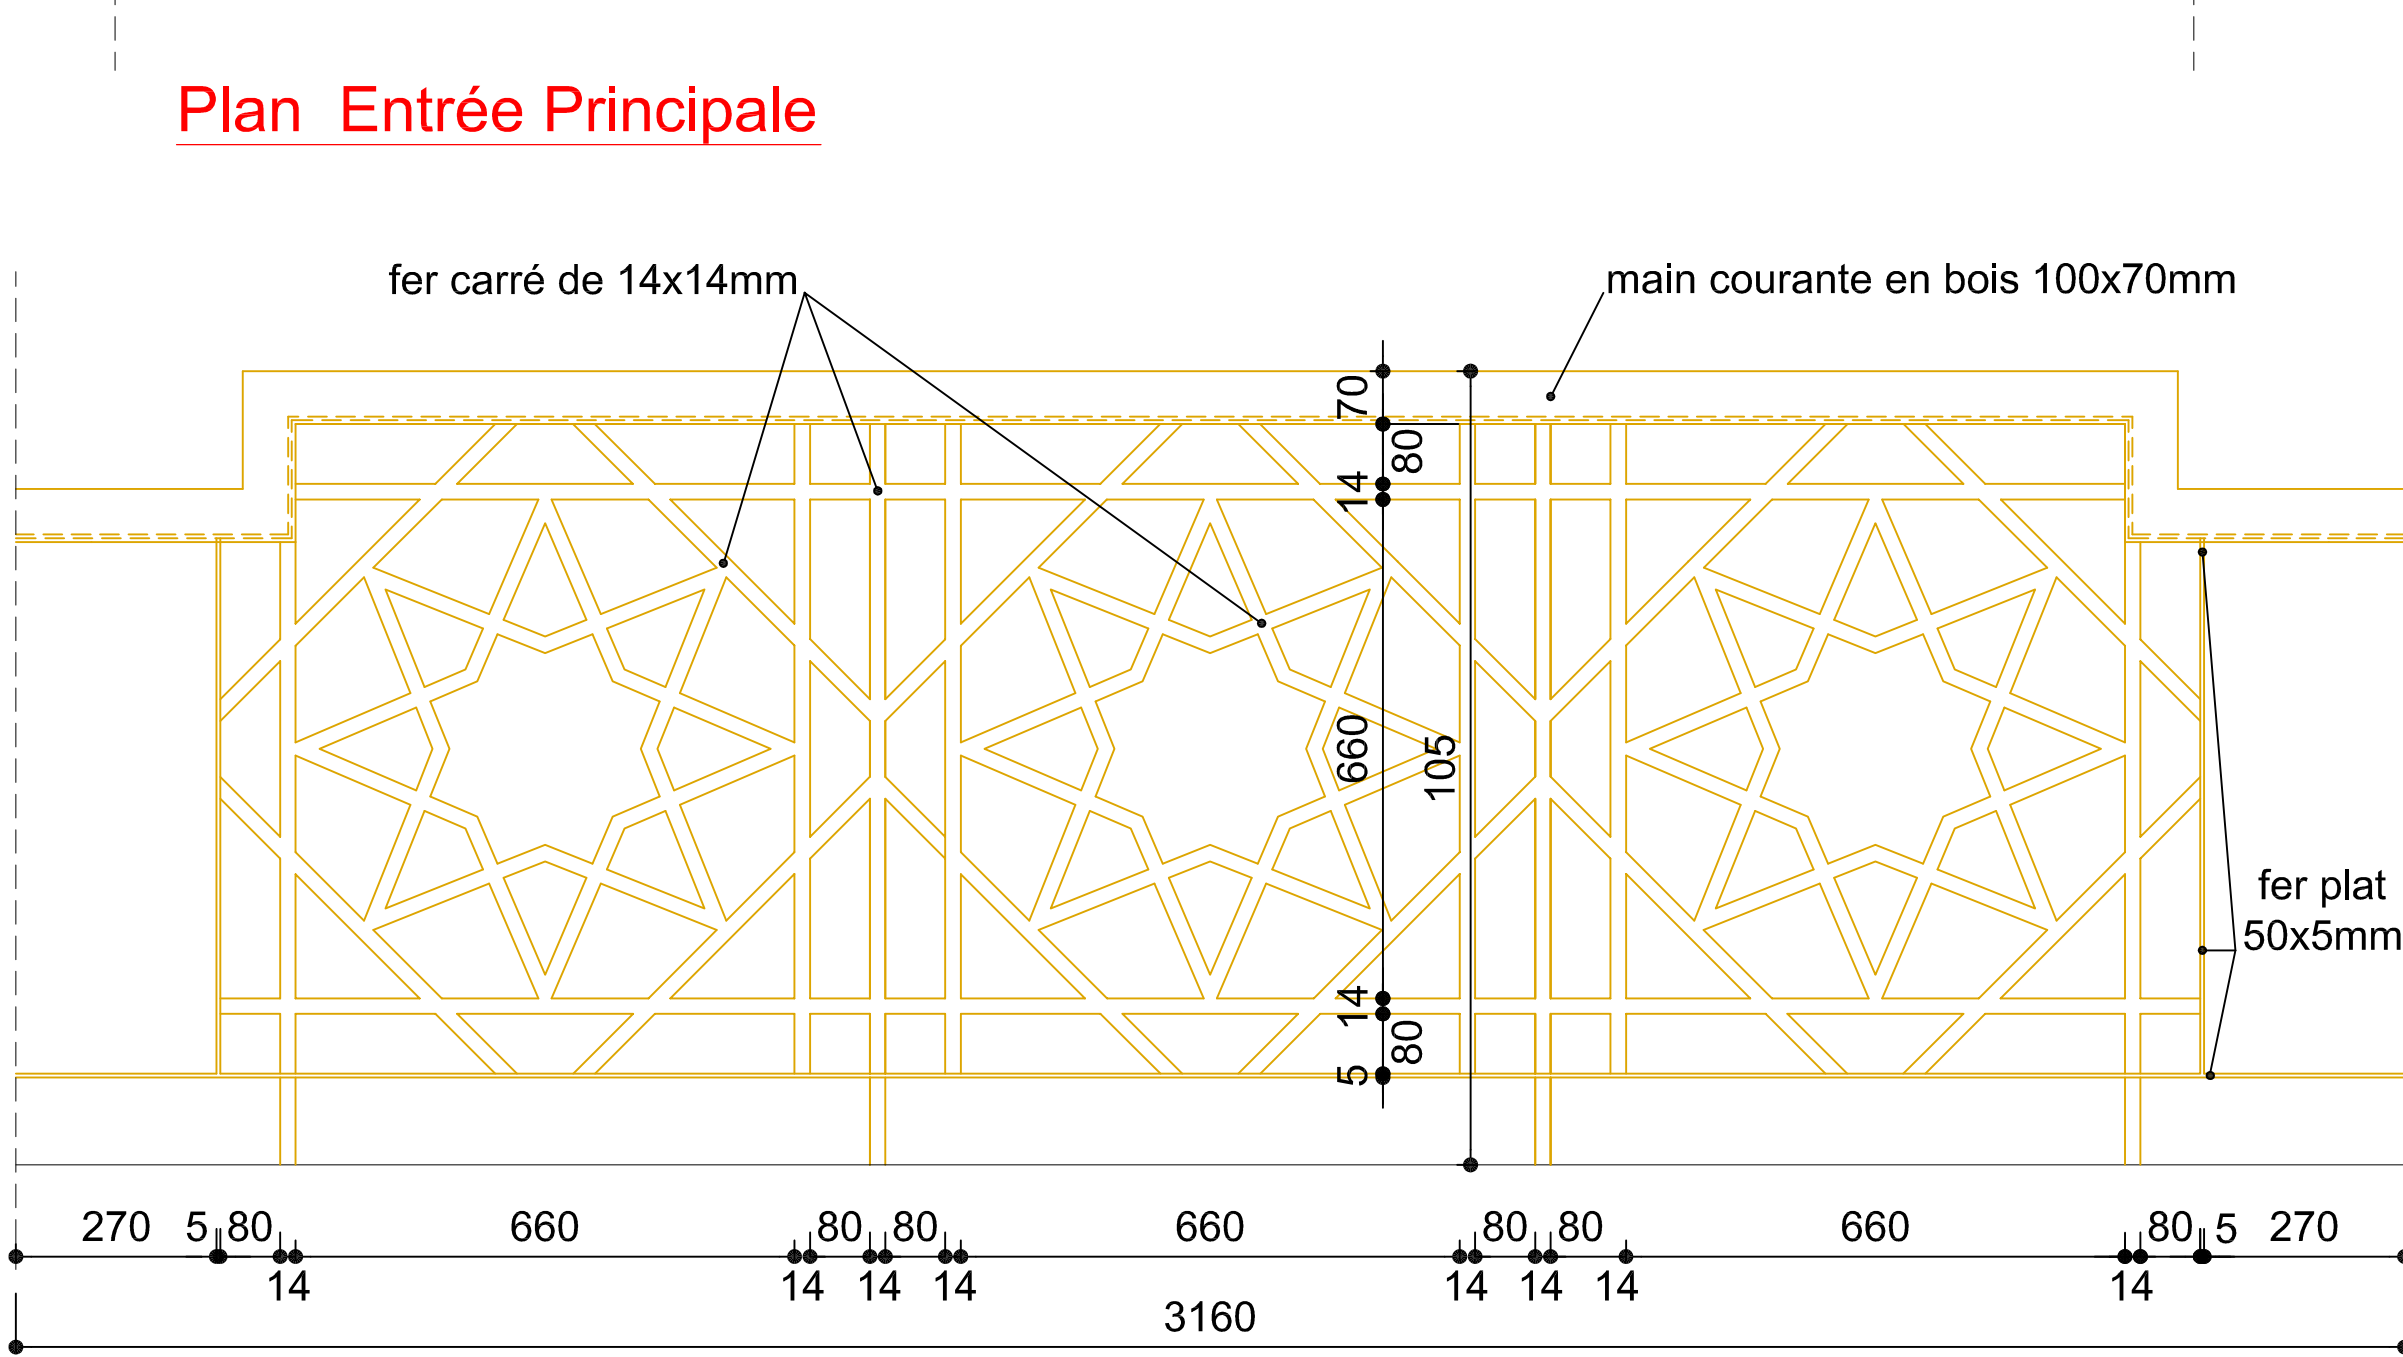

Détail Garde Corps


ECH : 1/10

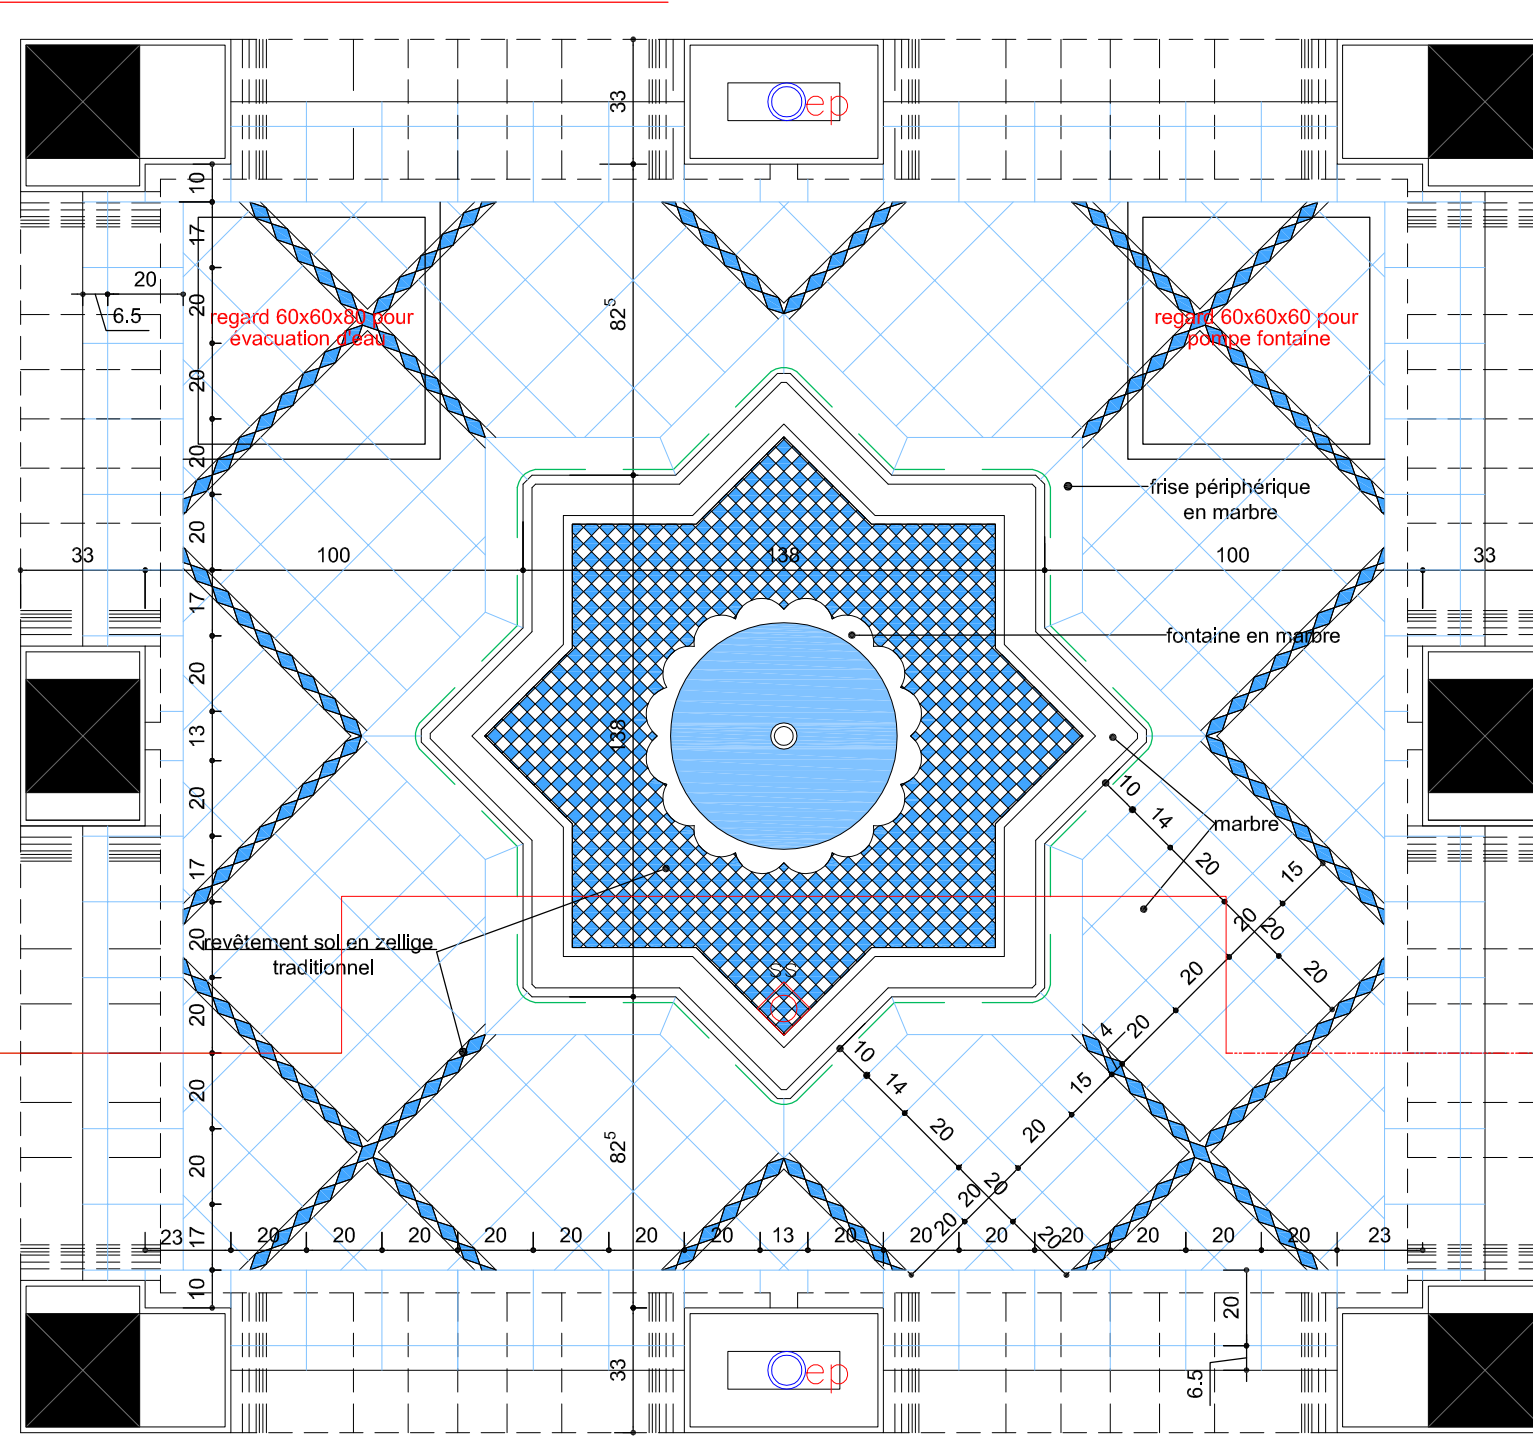


Plan détail C-C sur fontaine

détail console décorative en bois chêne

ECH : 1/2 grandeur

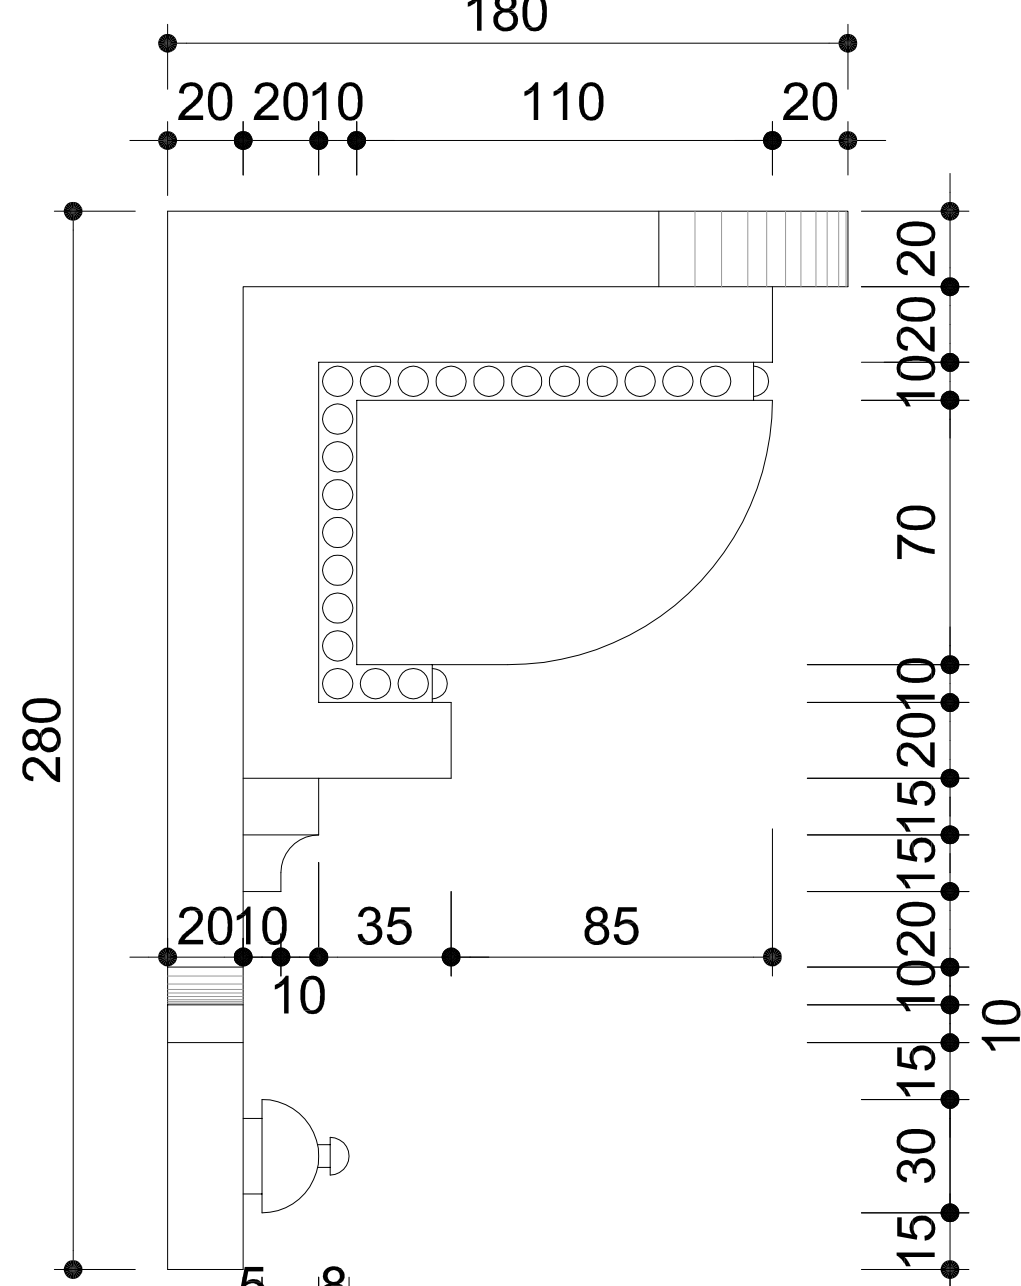


Vue de profil de la console

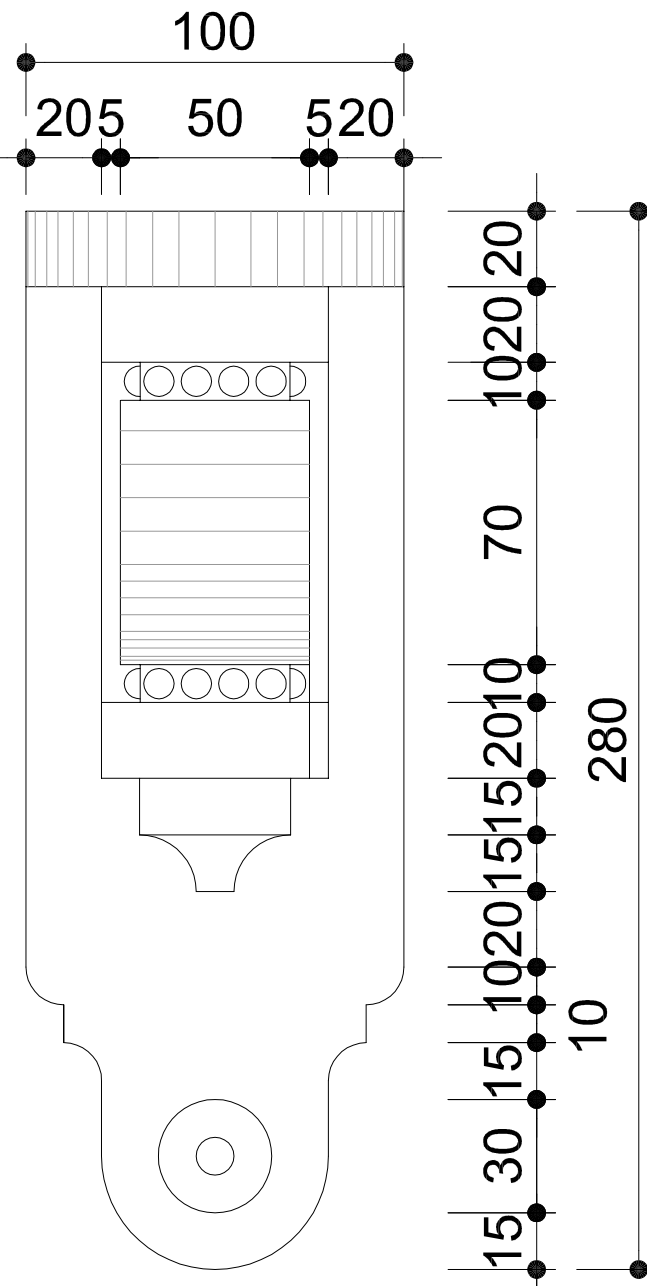


Vue frontale


détail 2 en mm
ECH : 1/10

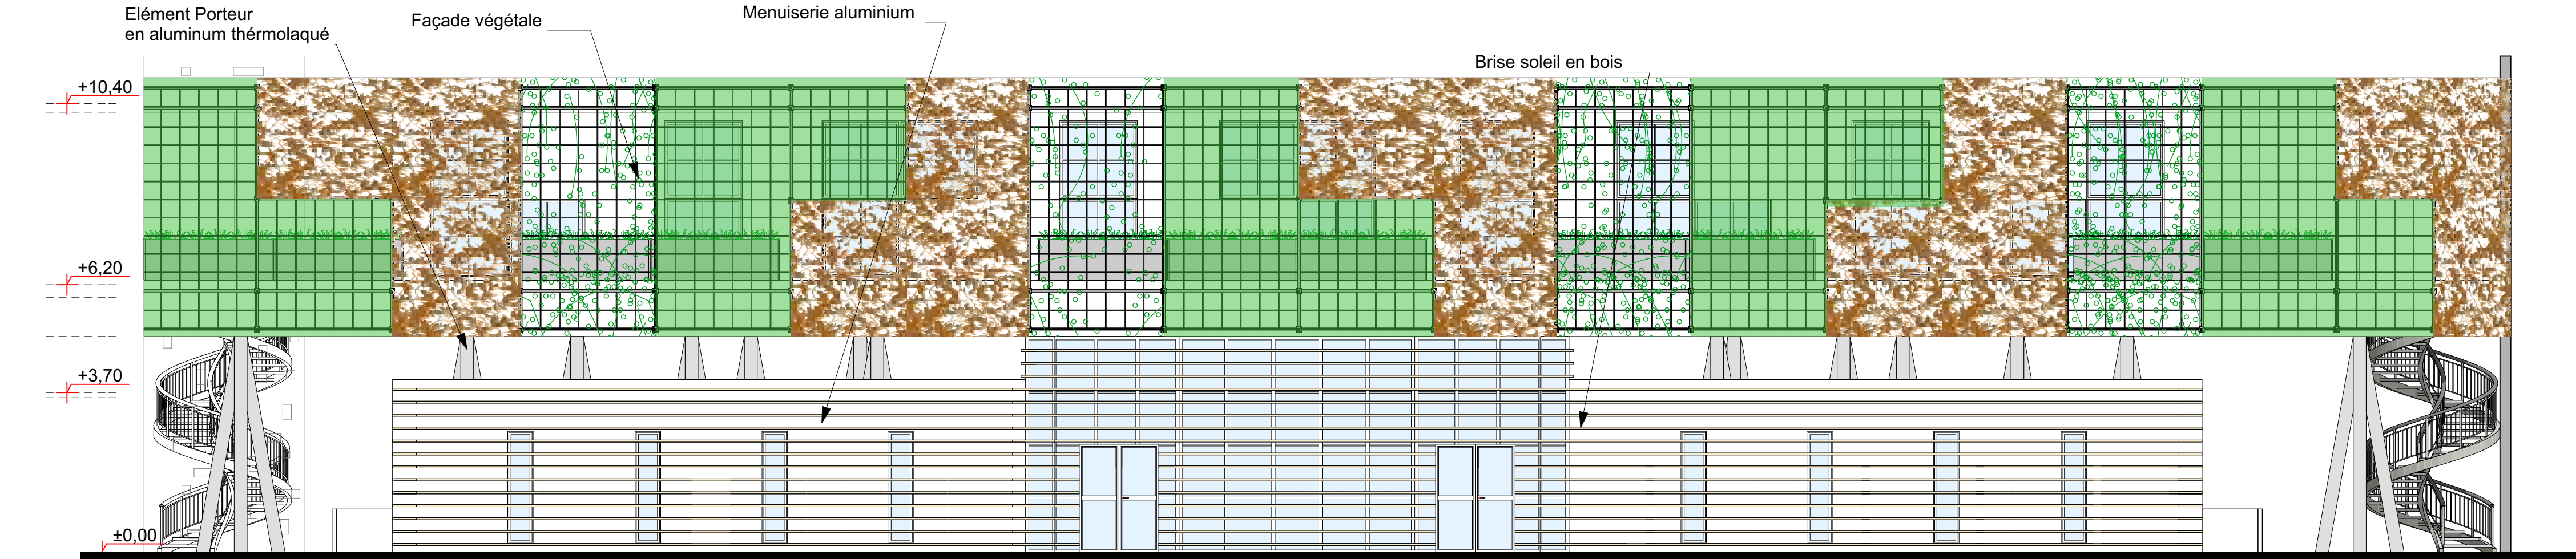


Façade Sud

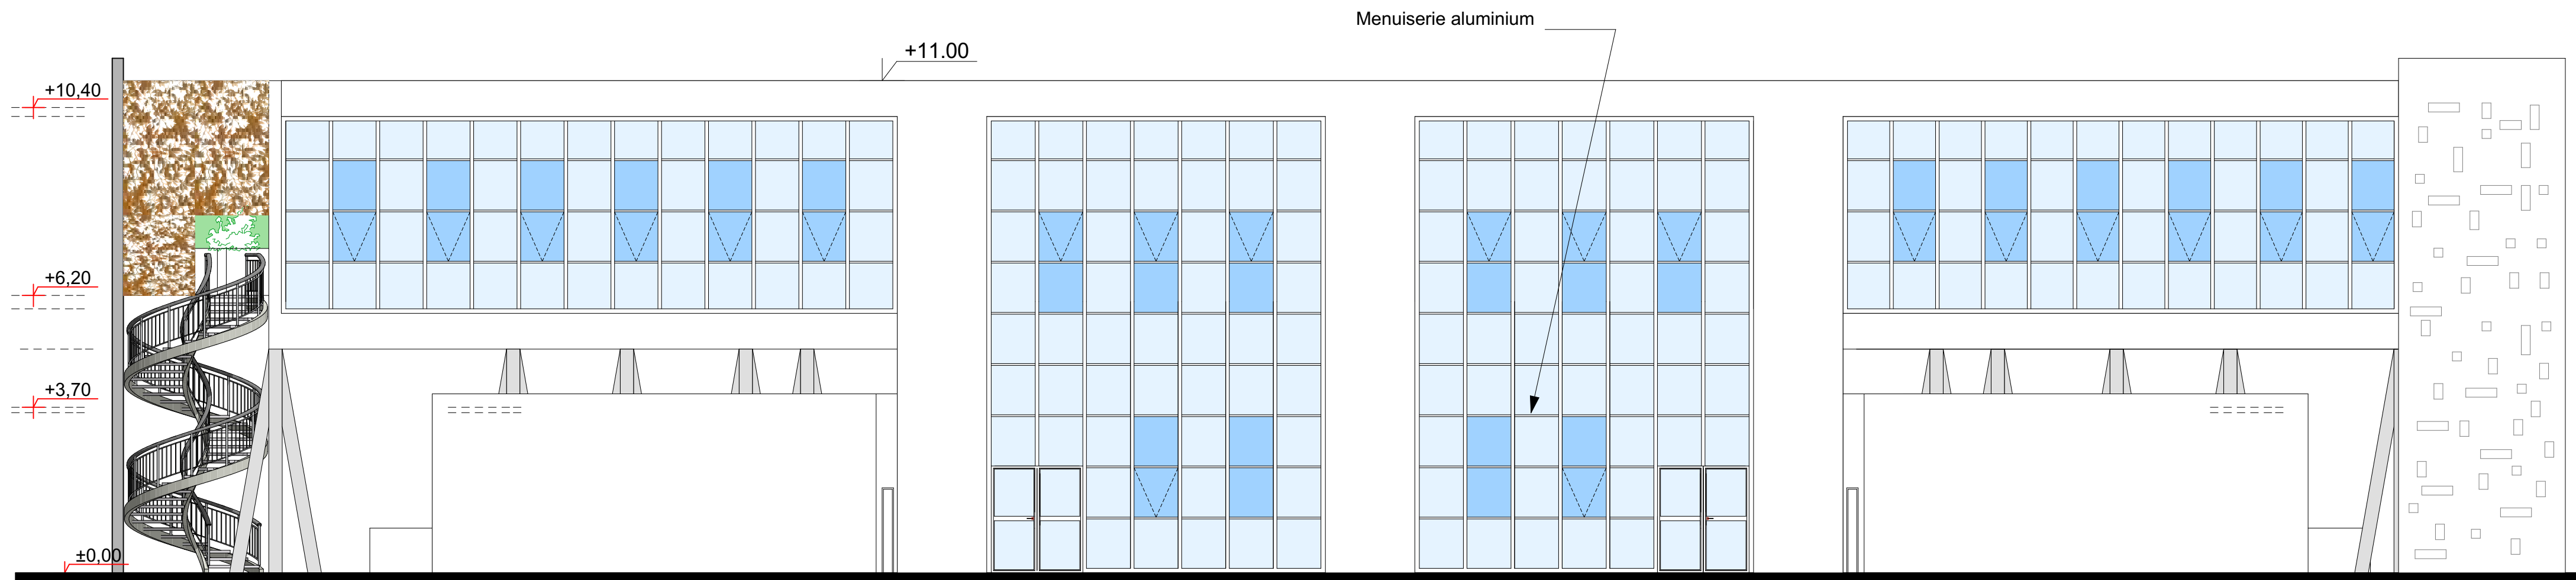

Façade Nord

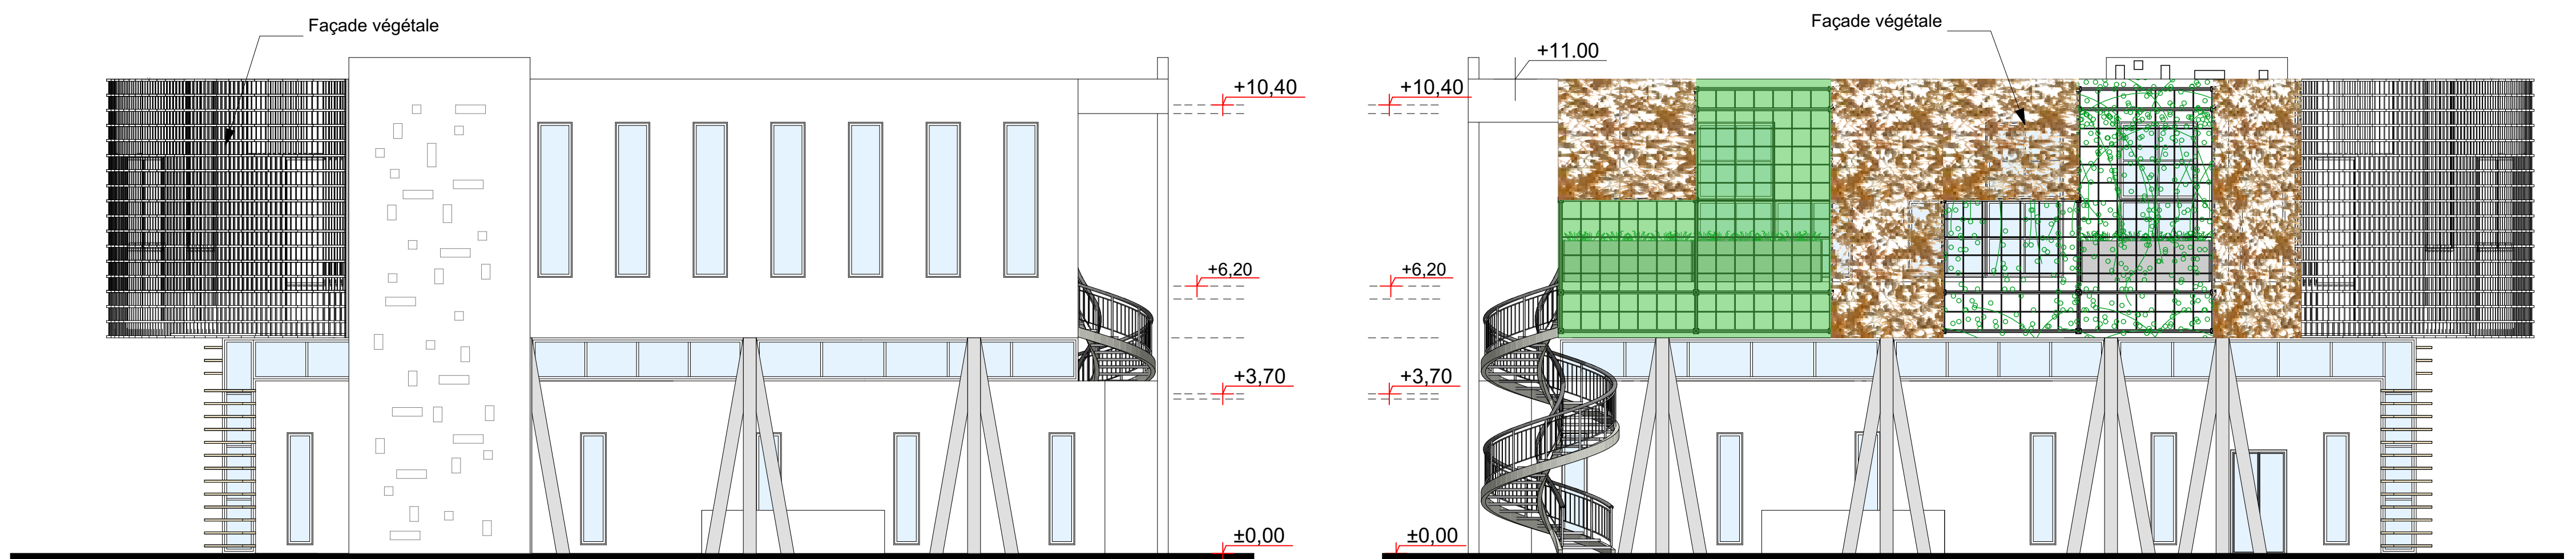


Façade Est

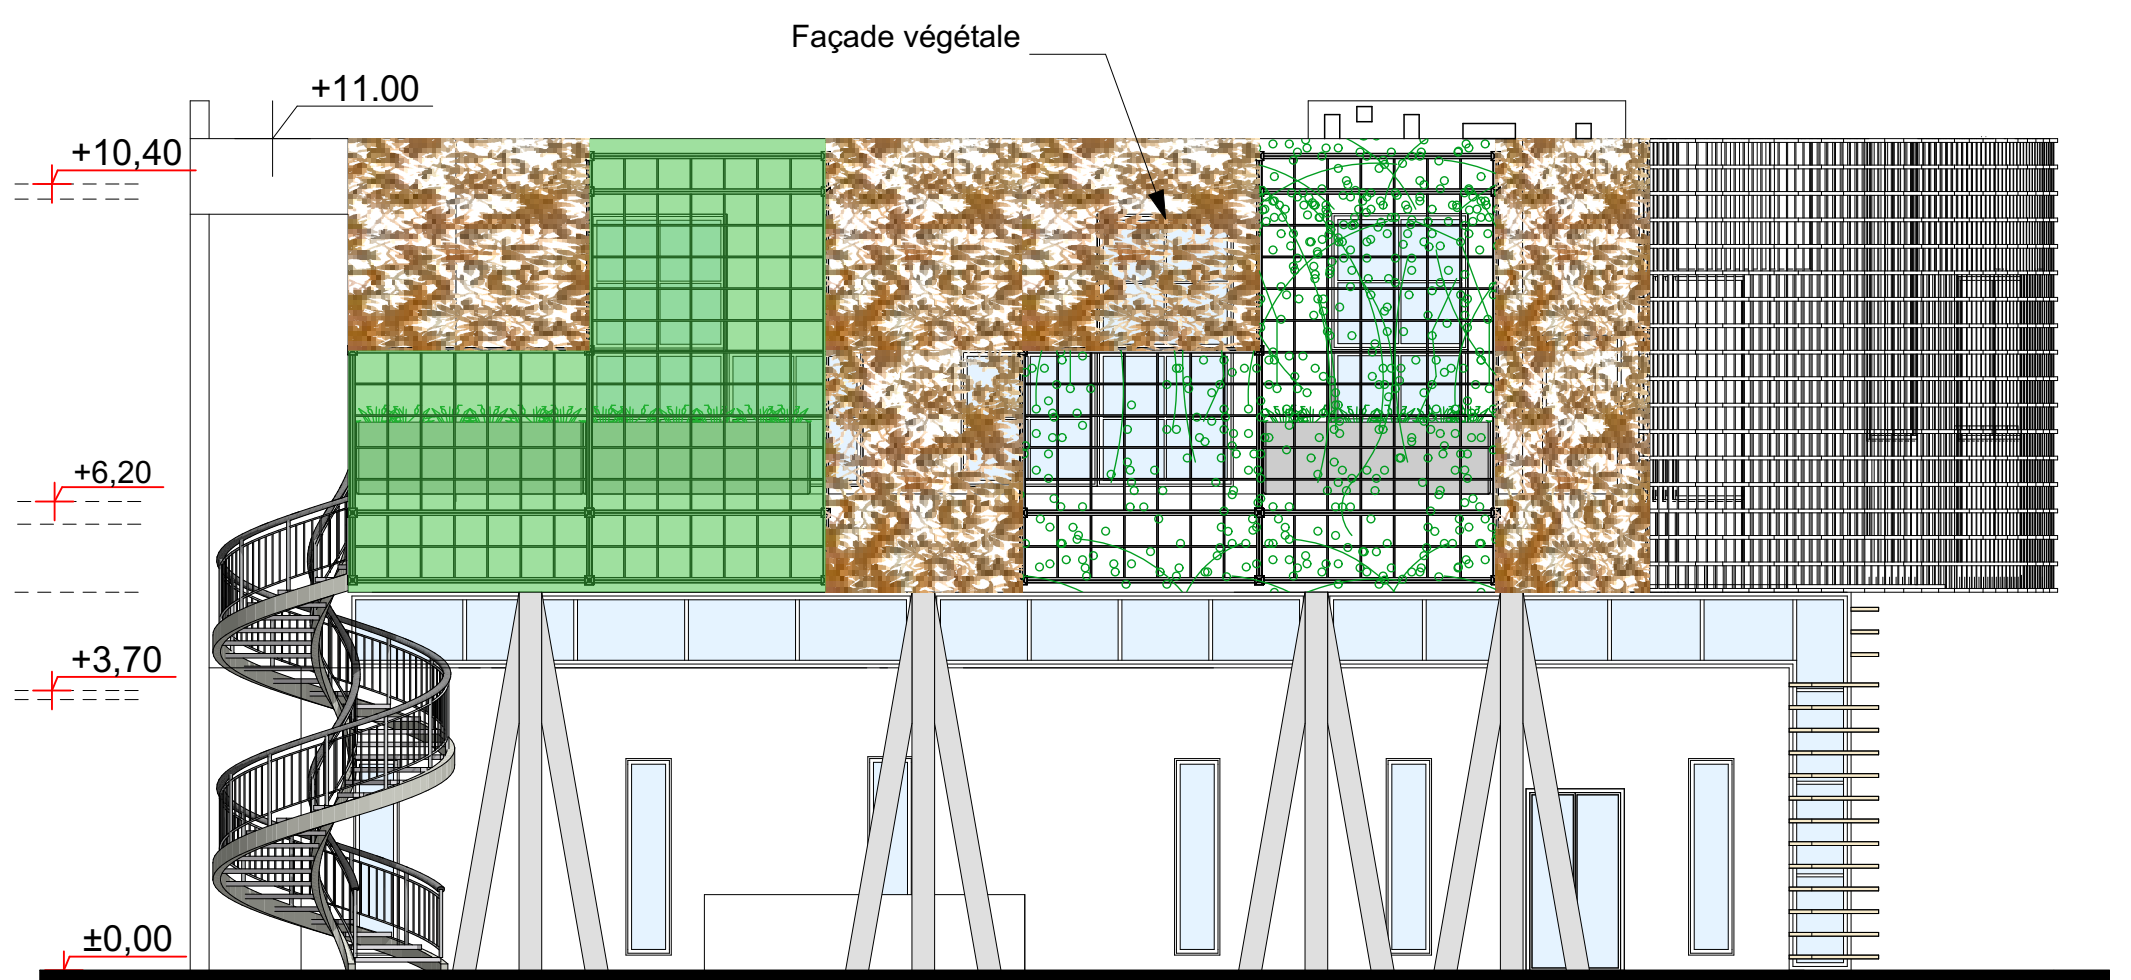


Façade Ouest




Coupe A-A

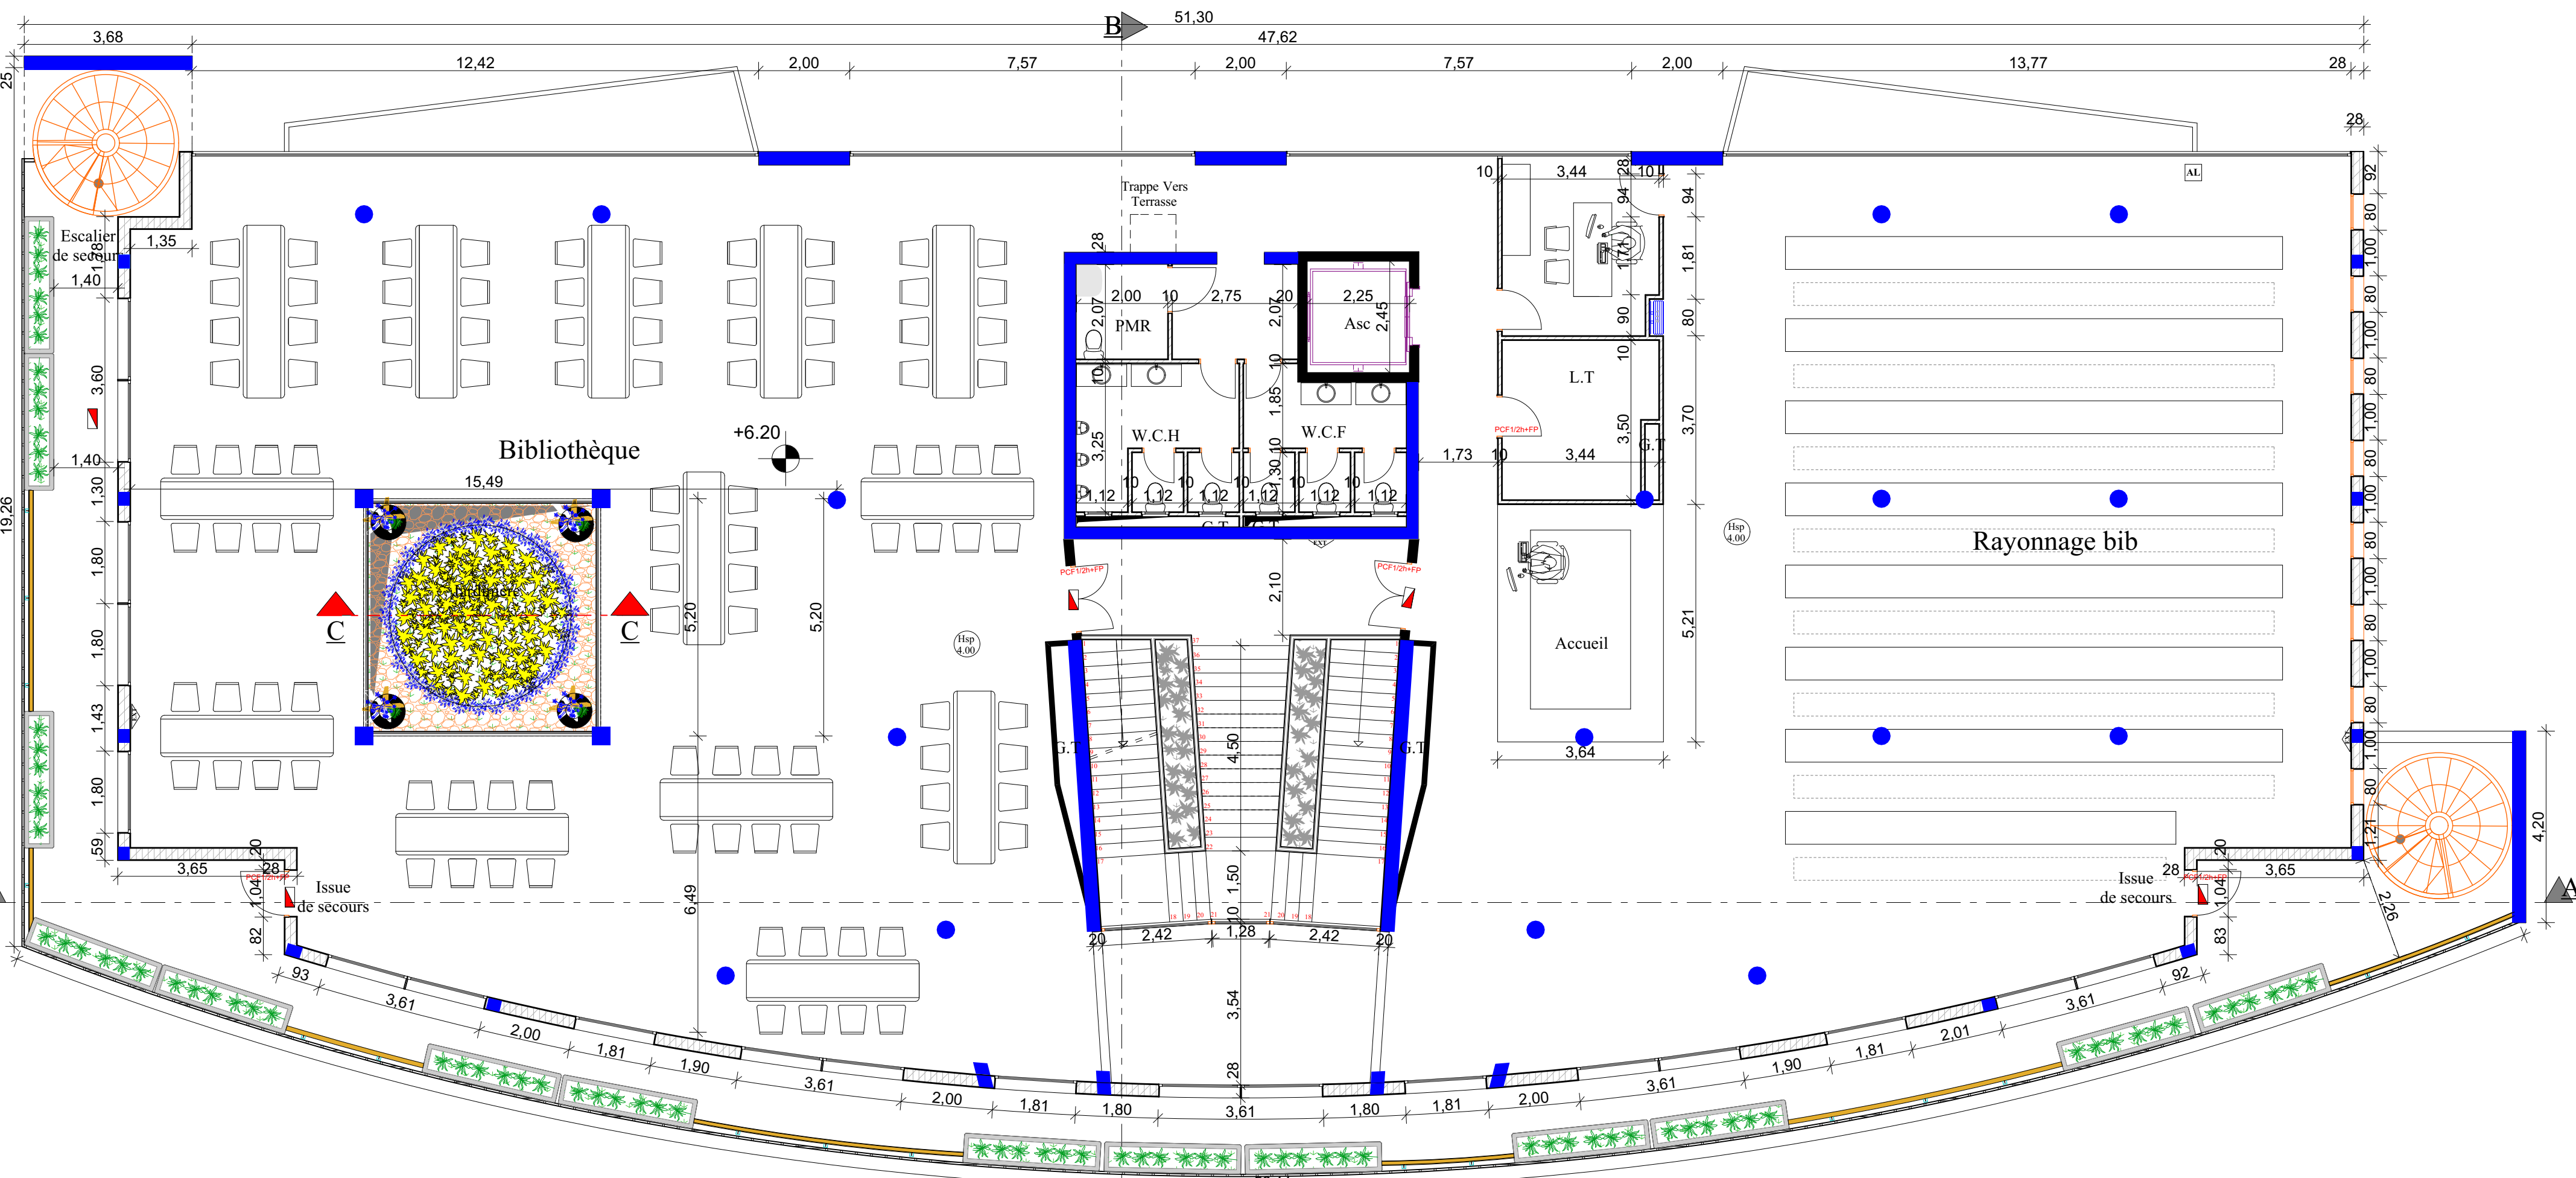


Etage

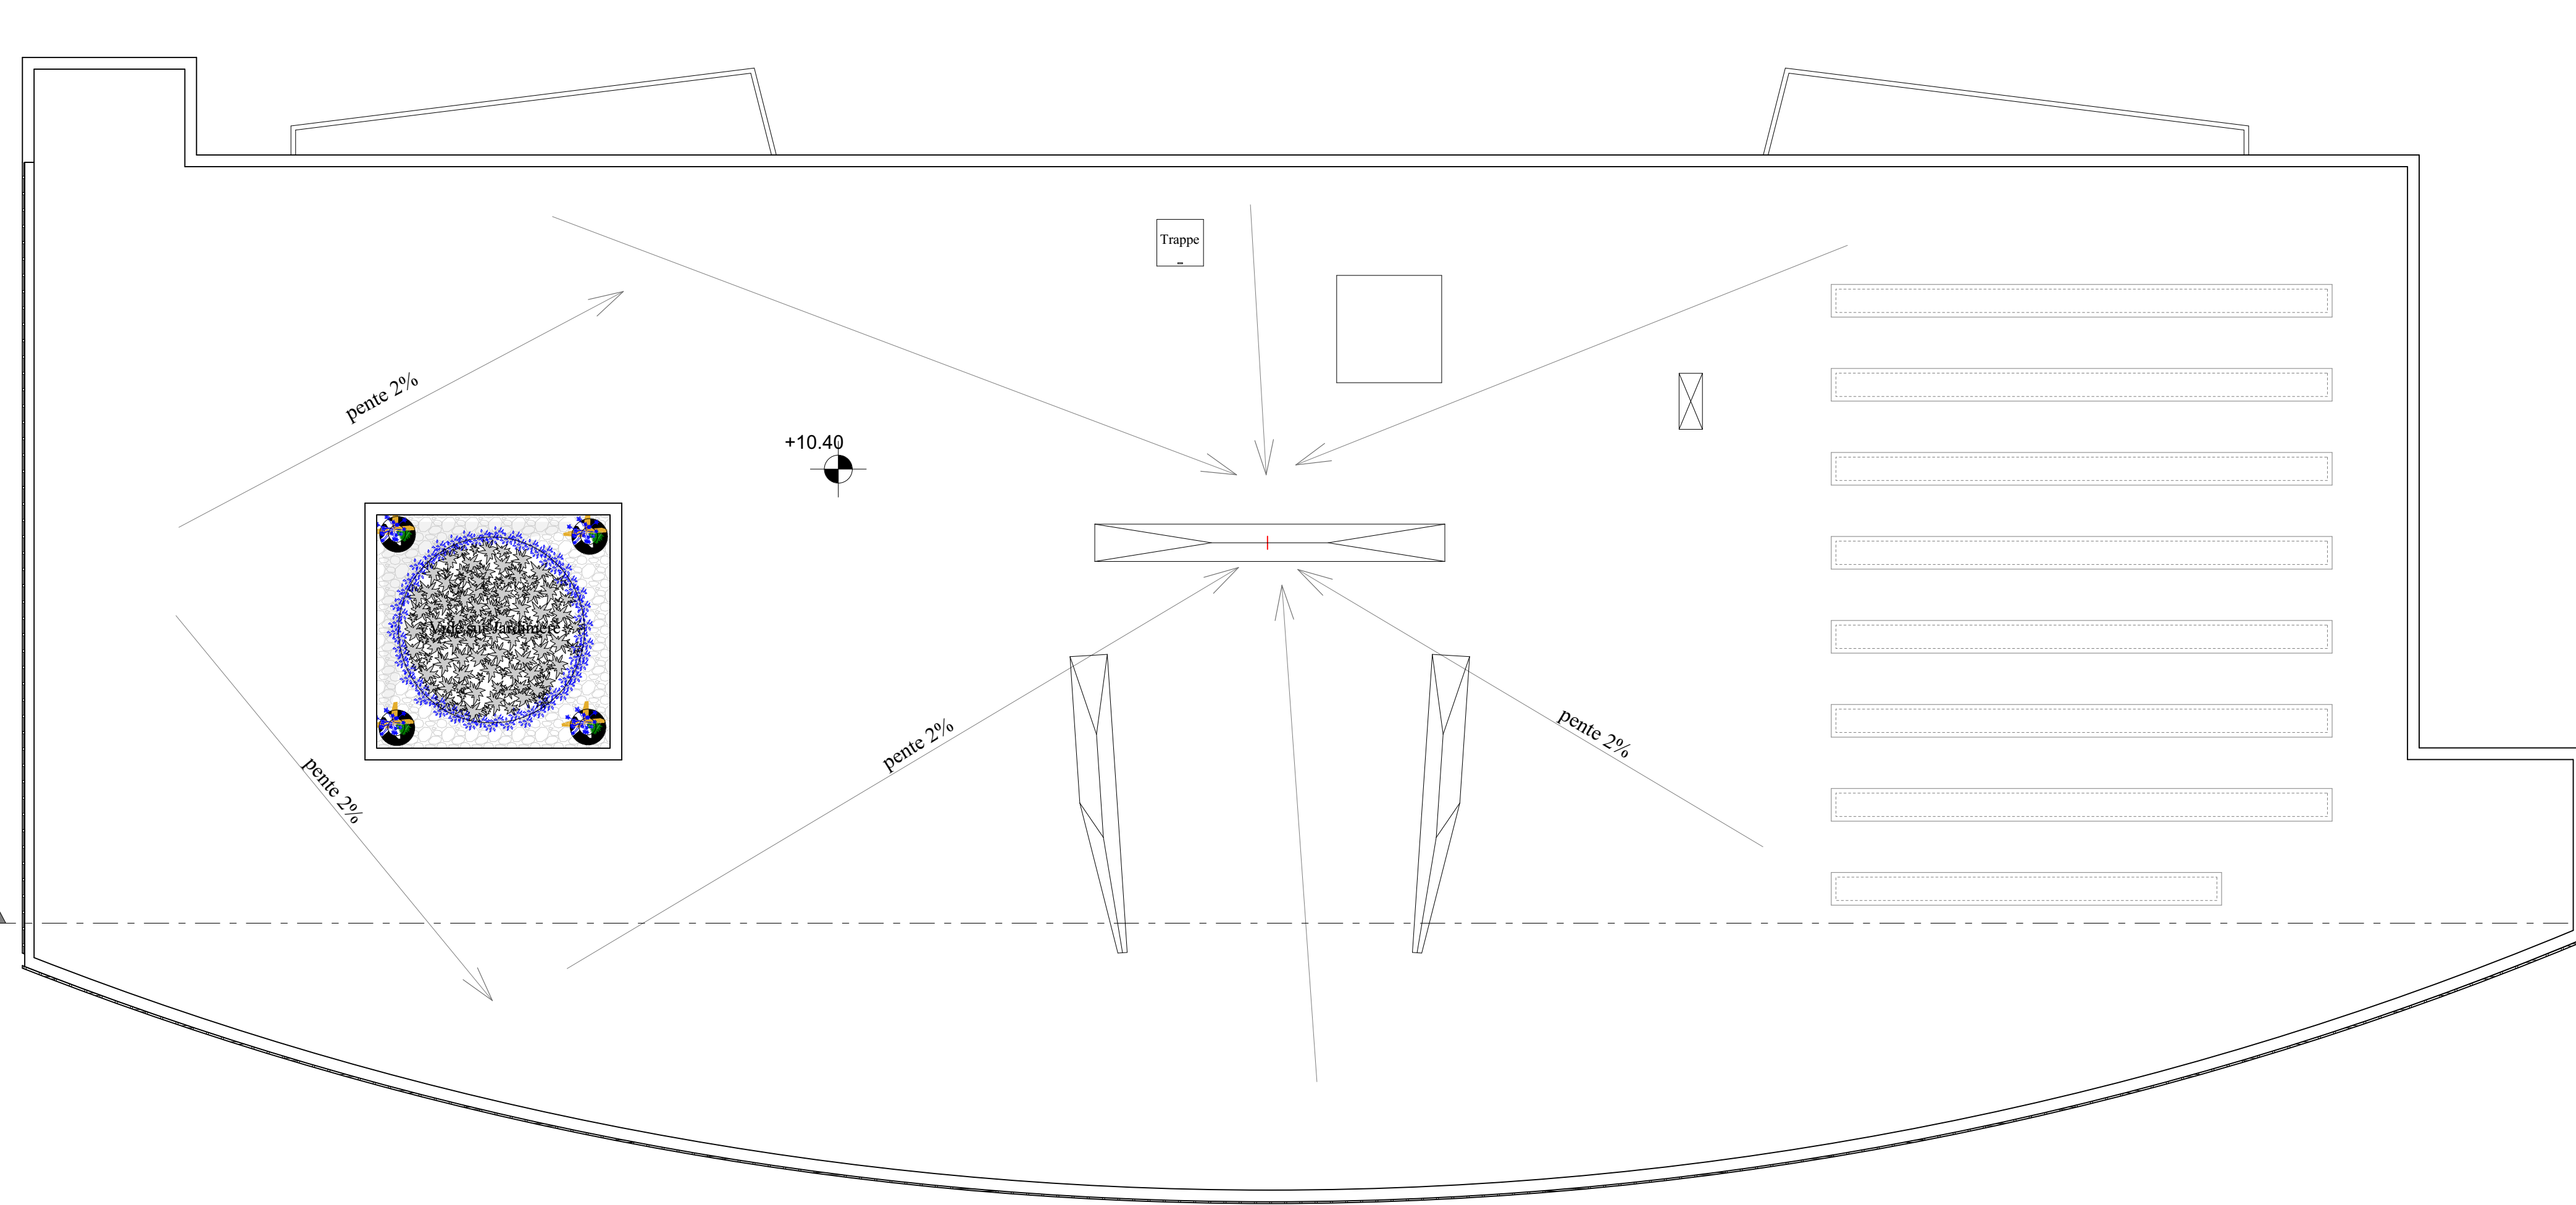

Terrasse

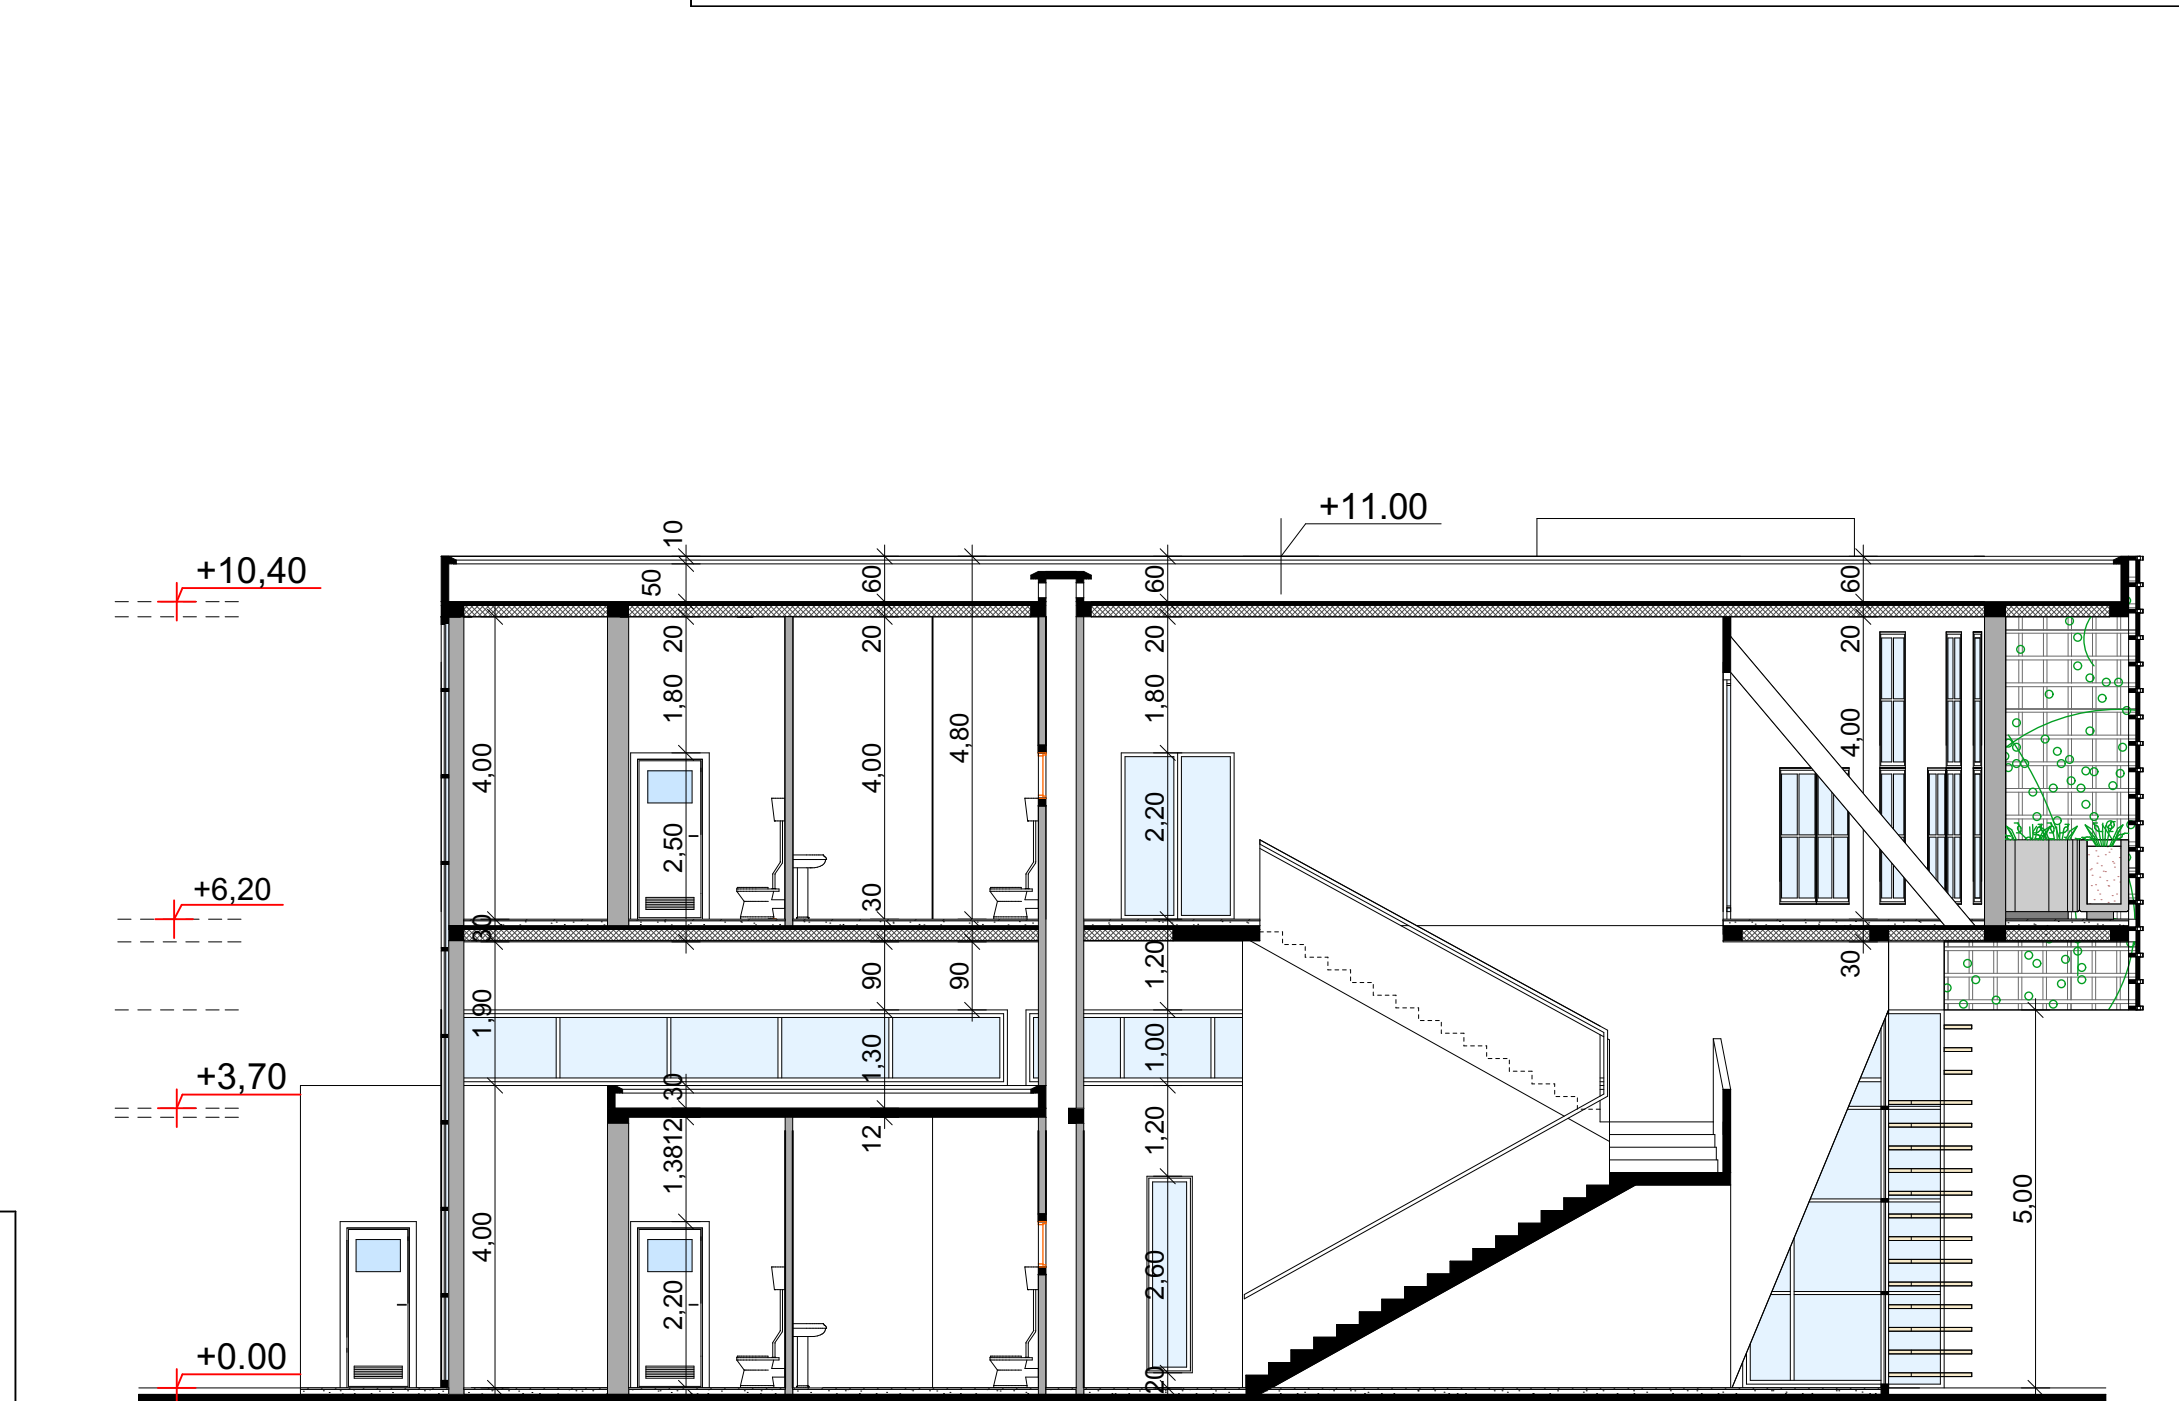

Coupe B-B

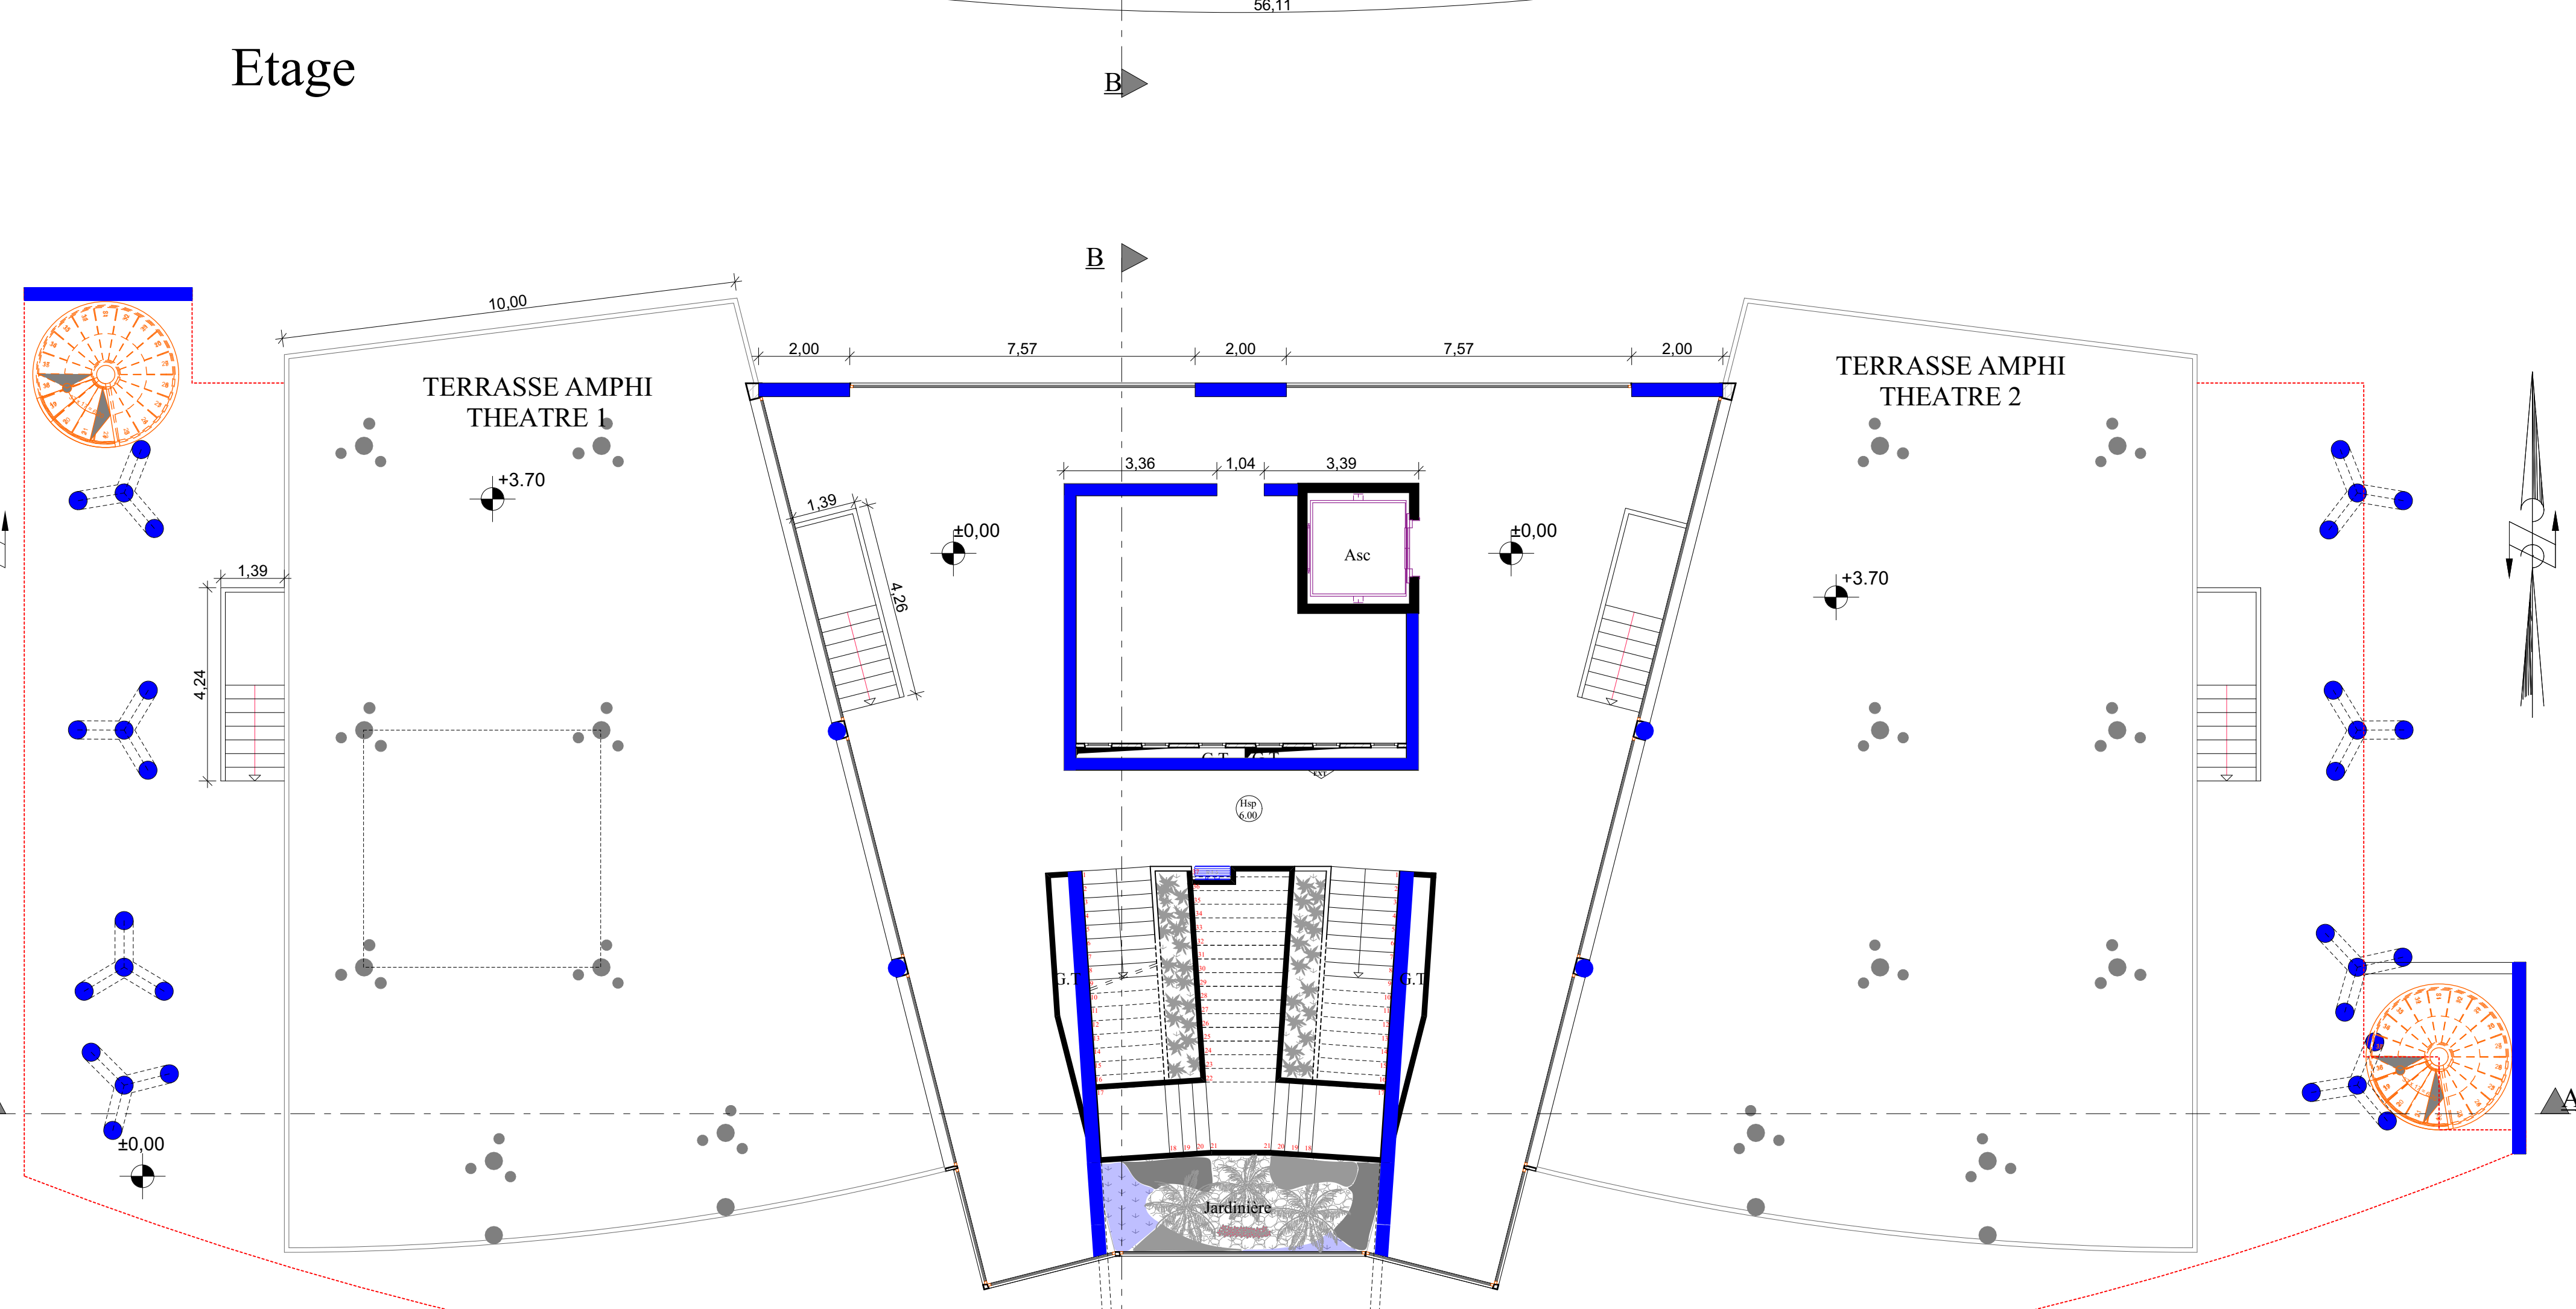

Terrasse Amphi




Rez de chaussée

LEGENDE D'INCENDIE

	BLOC AUTONOME D'ÉCLAIRAGE DE SÉCURITÉ
	ALARME SONORE (DETECTEUR DE FUMÉE)
	EXTINCTEUR
	PORTE COUPE FEU 1/2 h - FERMÉE
	MUR COUPE FEU 2h
	DALLE COUPE FEU 1h
	ROBINET D'INCENDIE ARMÉ


2-AMPHI-THEATRE & BIBLIOTHEQUE

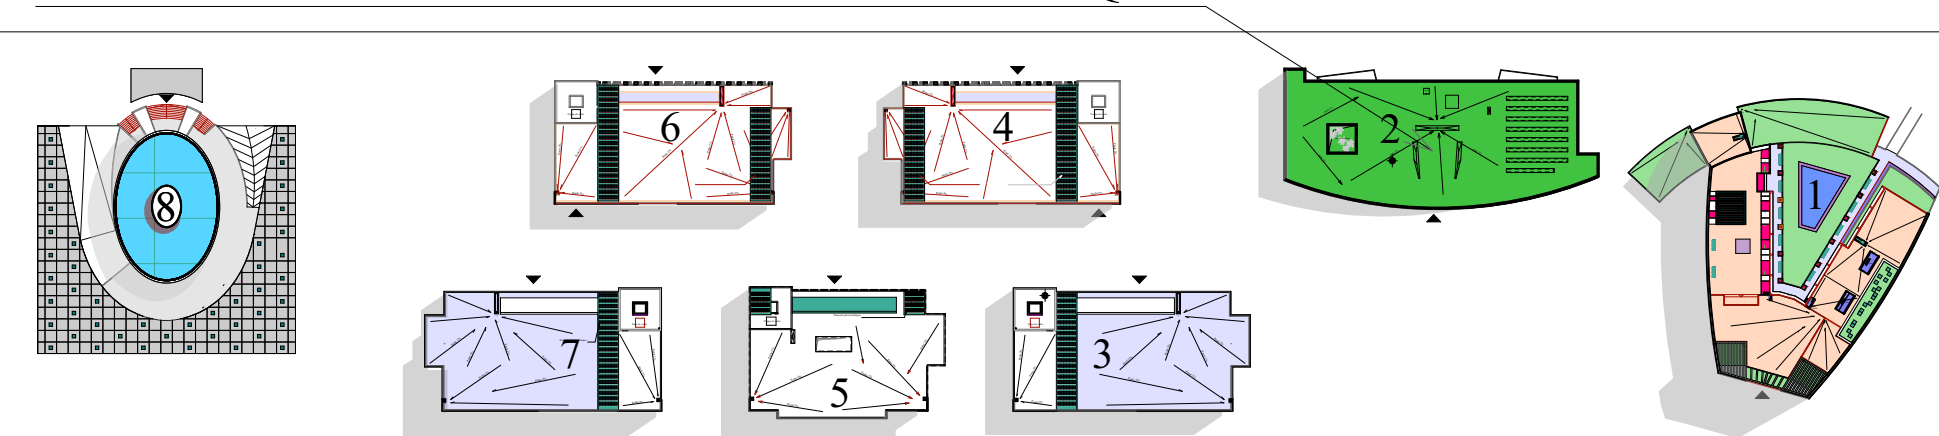


Plan de masse global

PREFECTURE DE SKHIRAT TEMARA
COMMUNE DE SIDI YAHIA ZAËRS
VILLE DE TAMESNA


TAMESNA

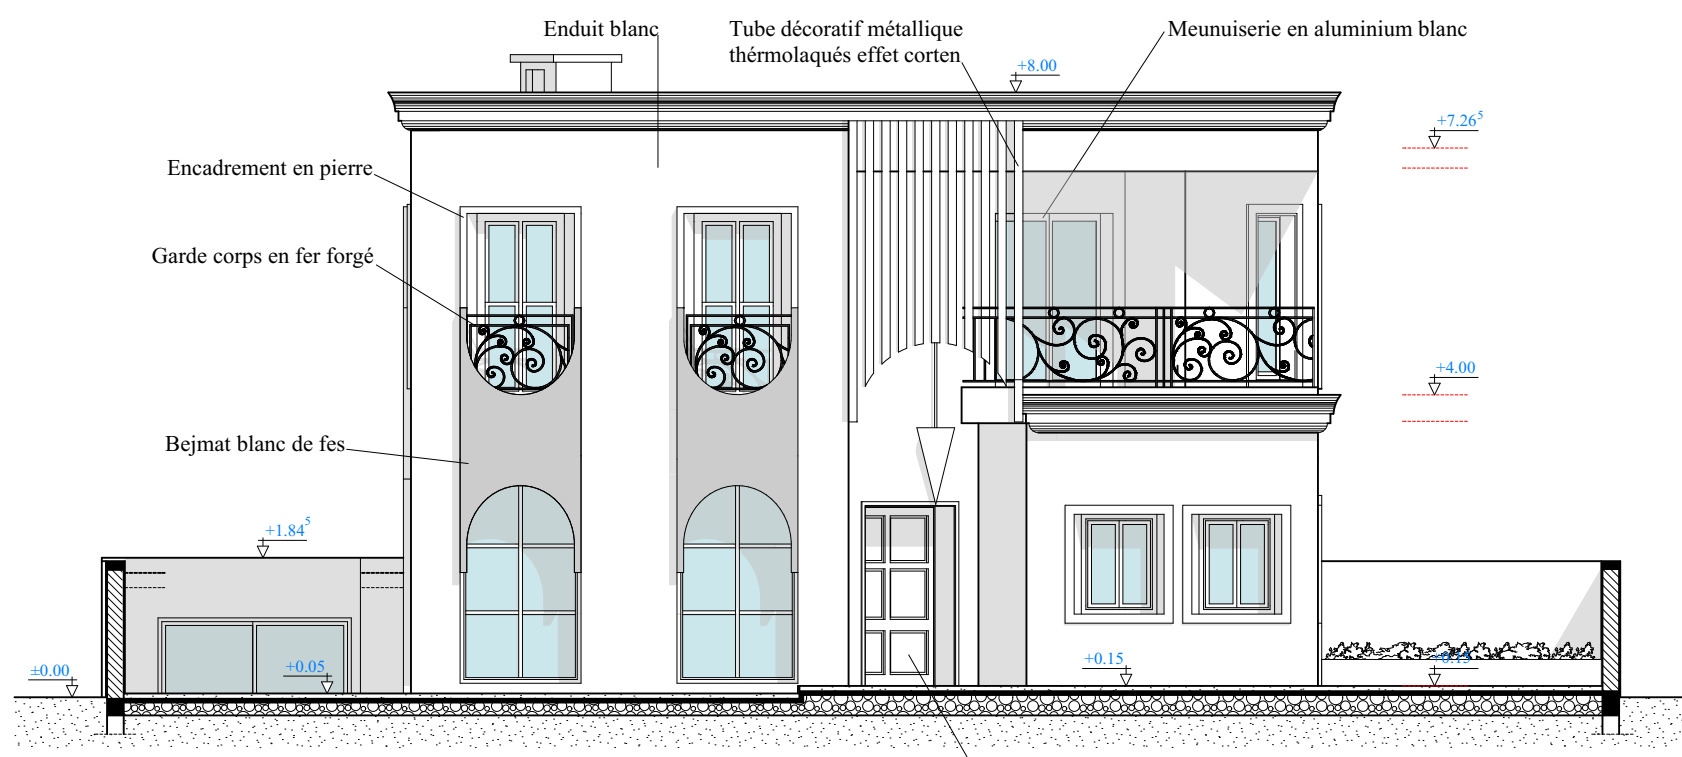


FACADE PRINCIPALE

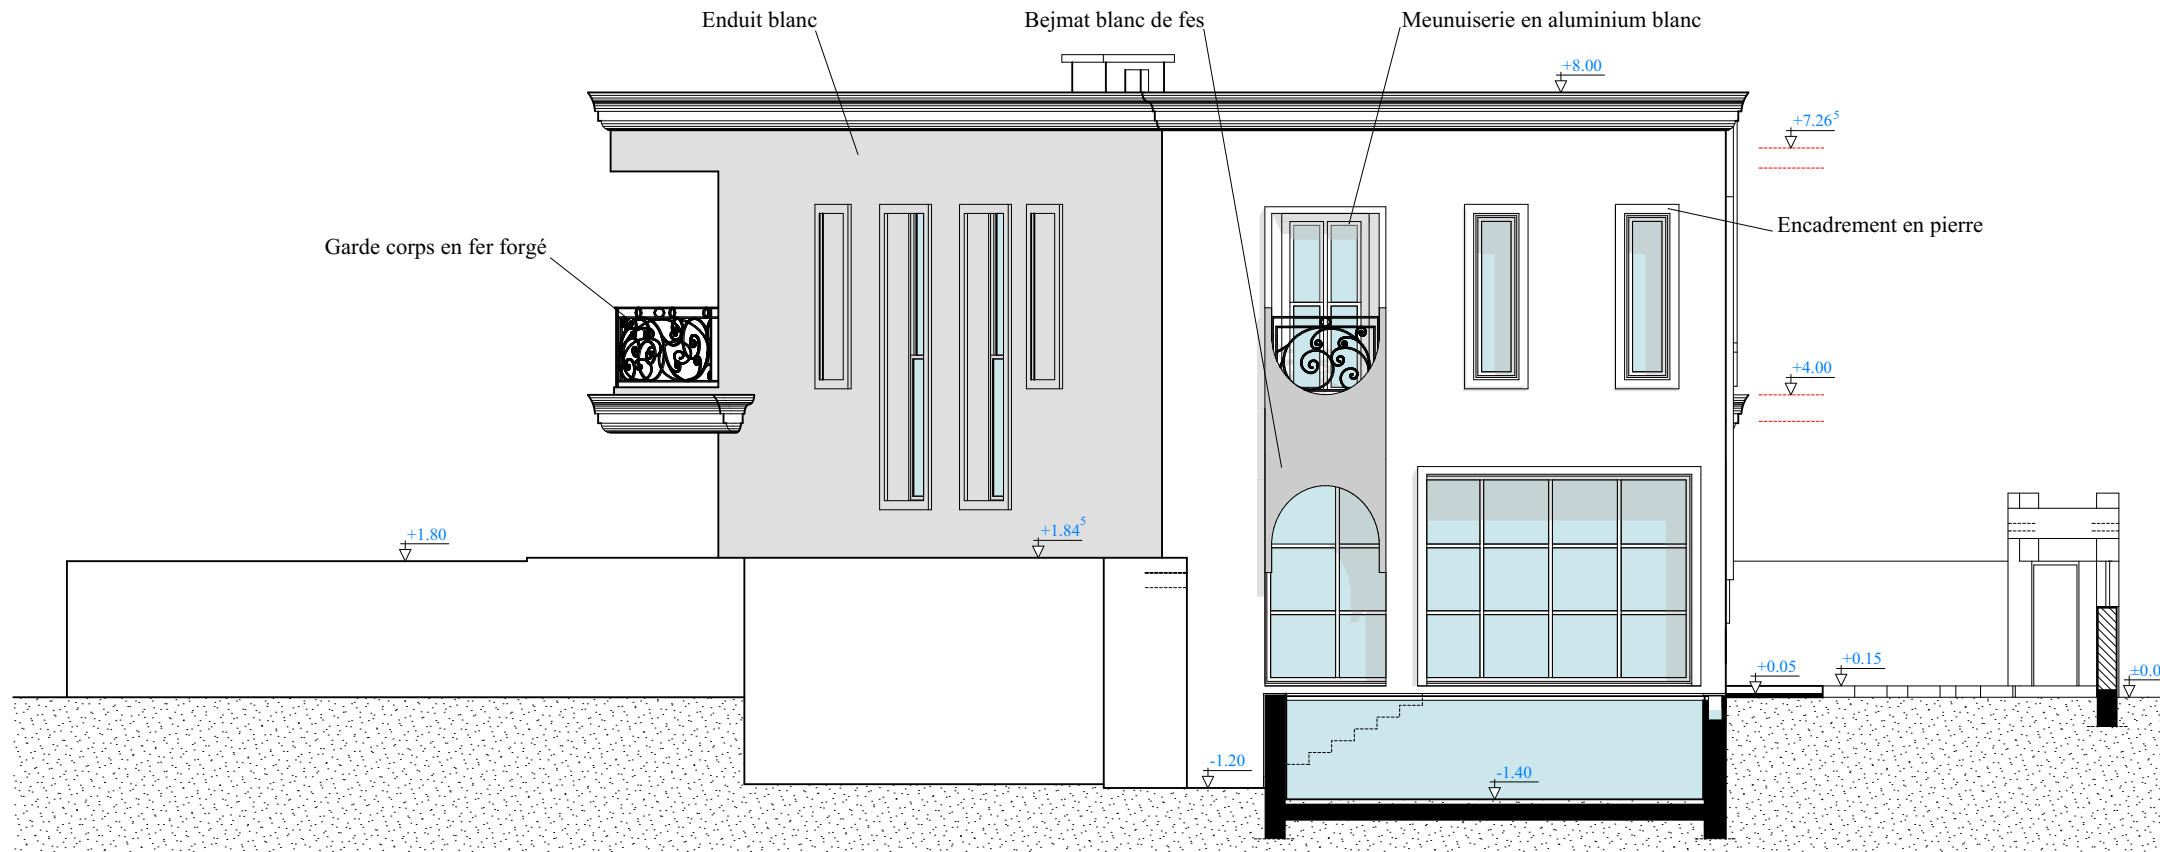


FACADE GAUCHE

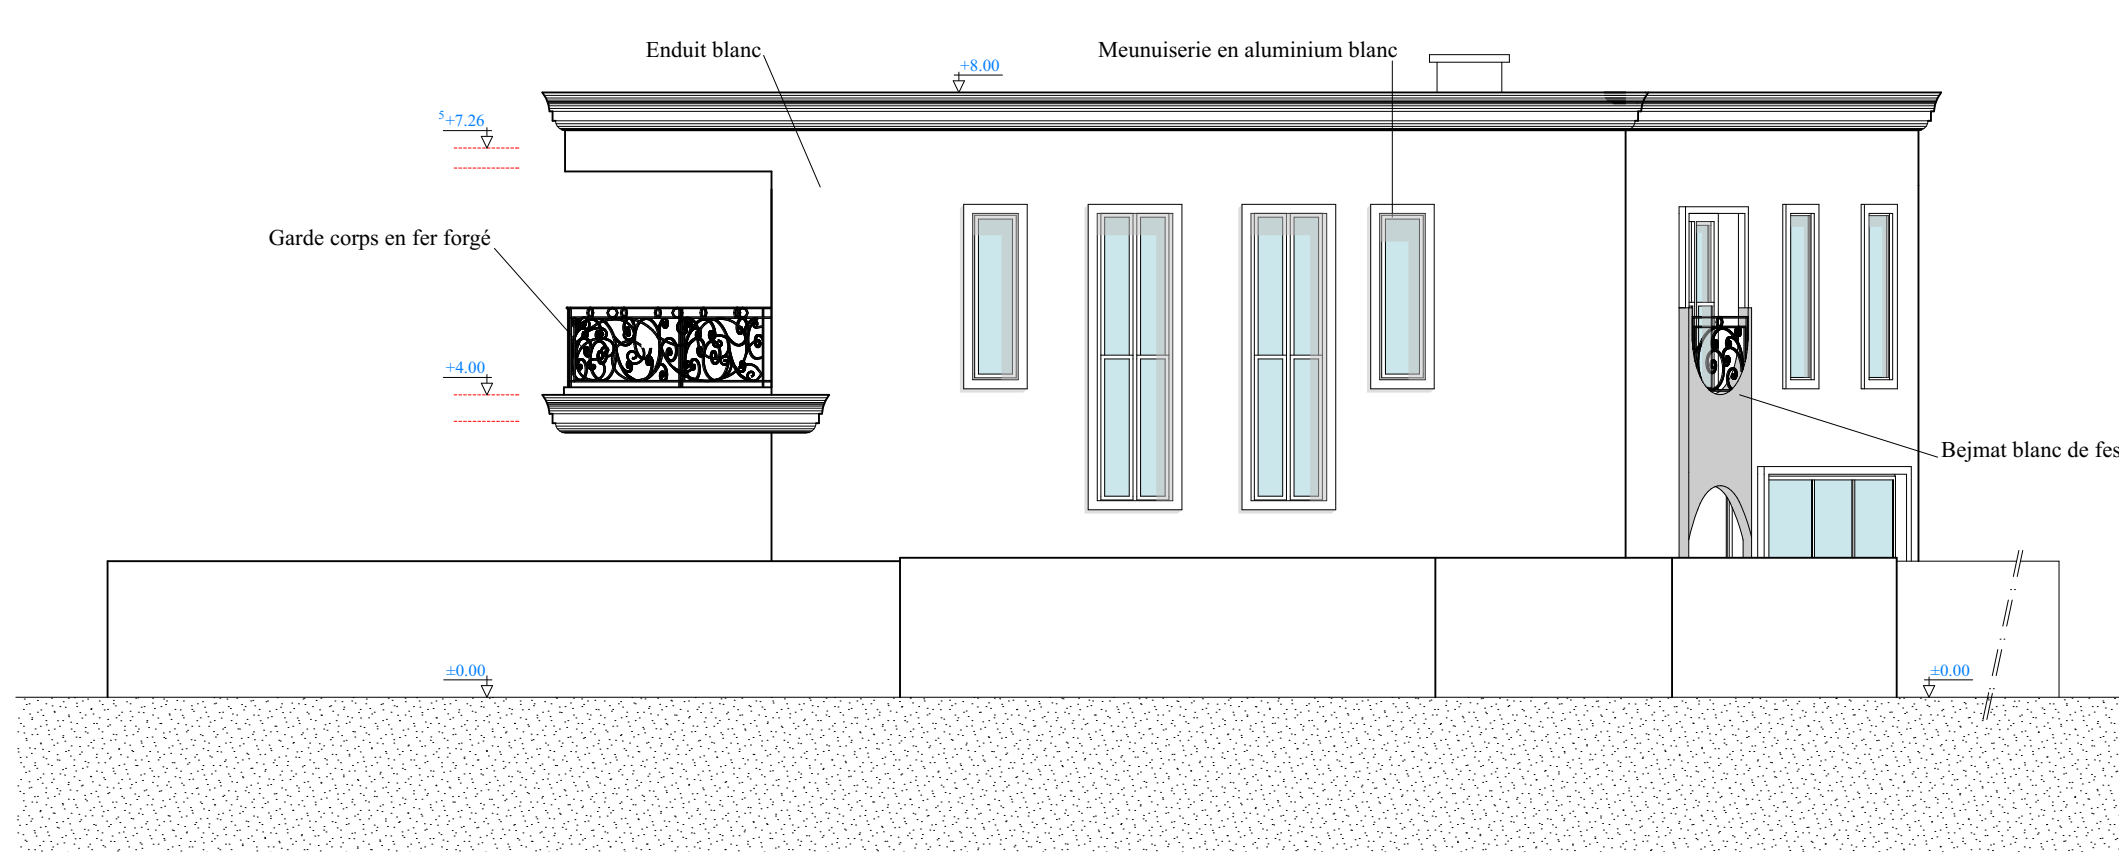


FACADE ARRIERE

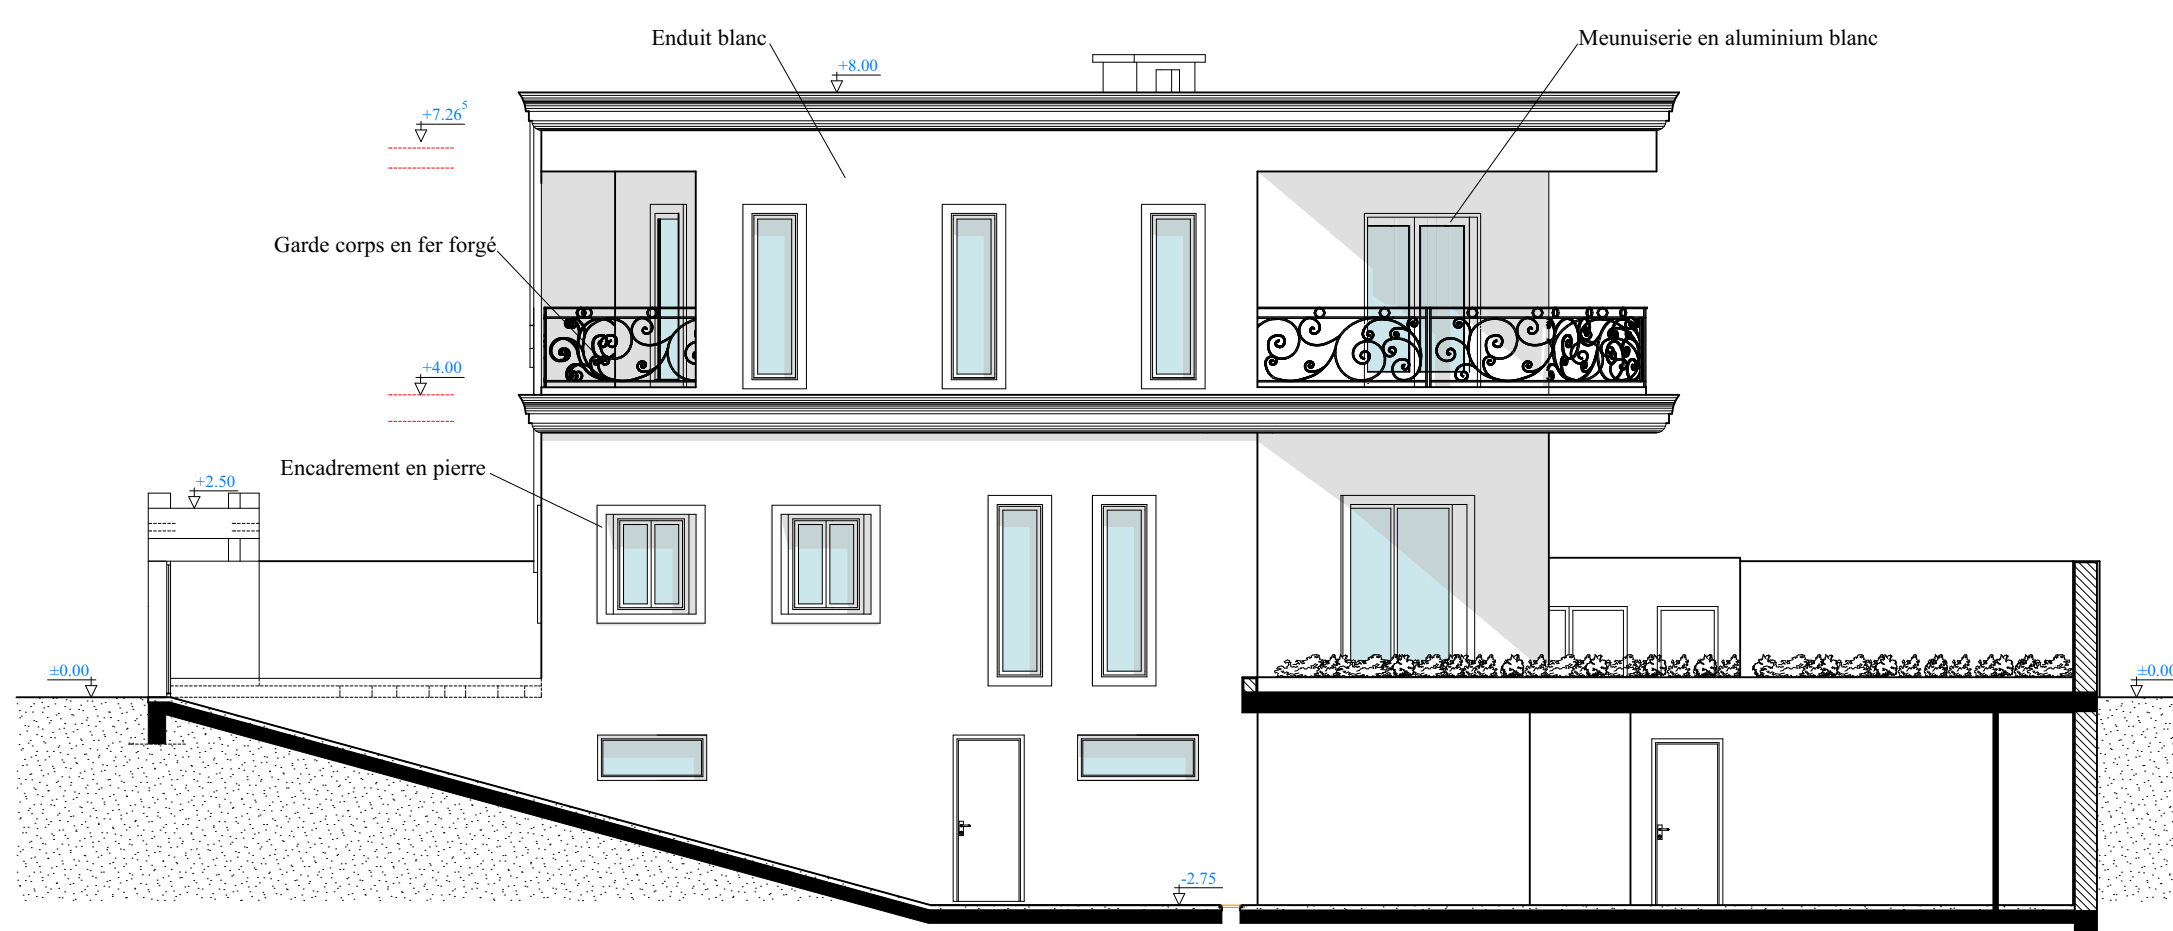

FACADE DROITE

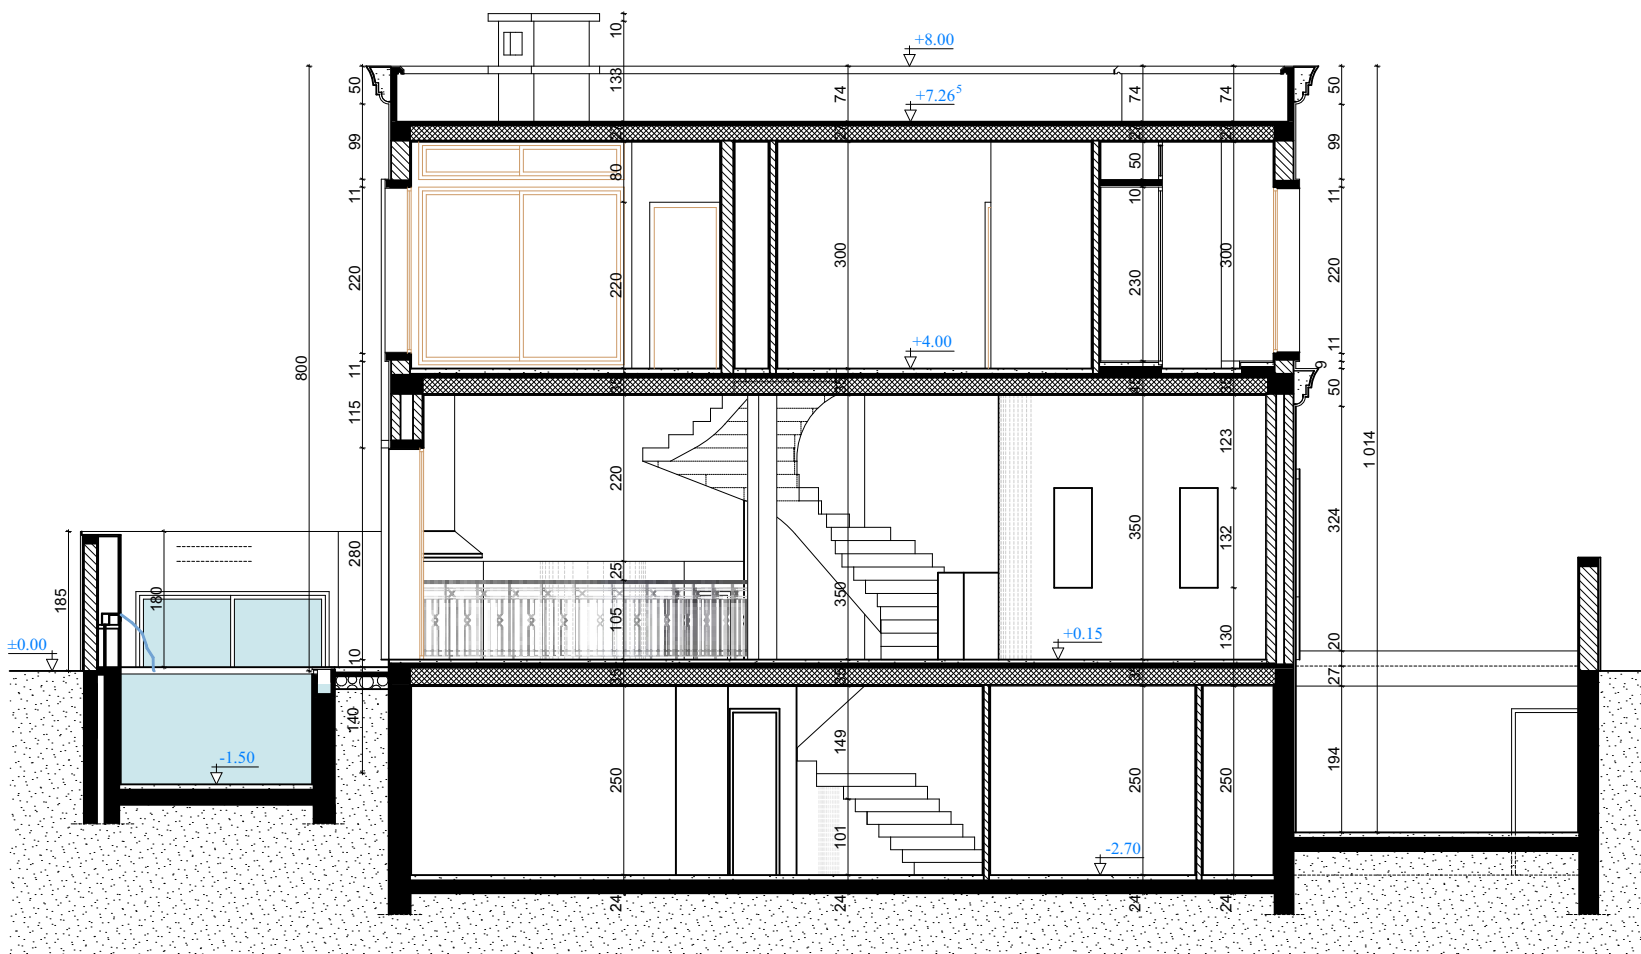




COUPE A-A

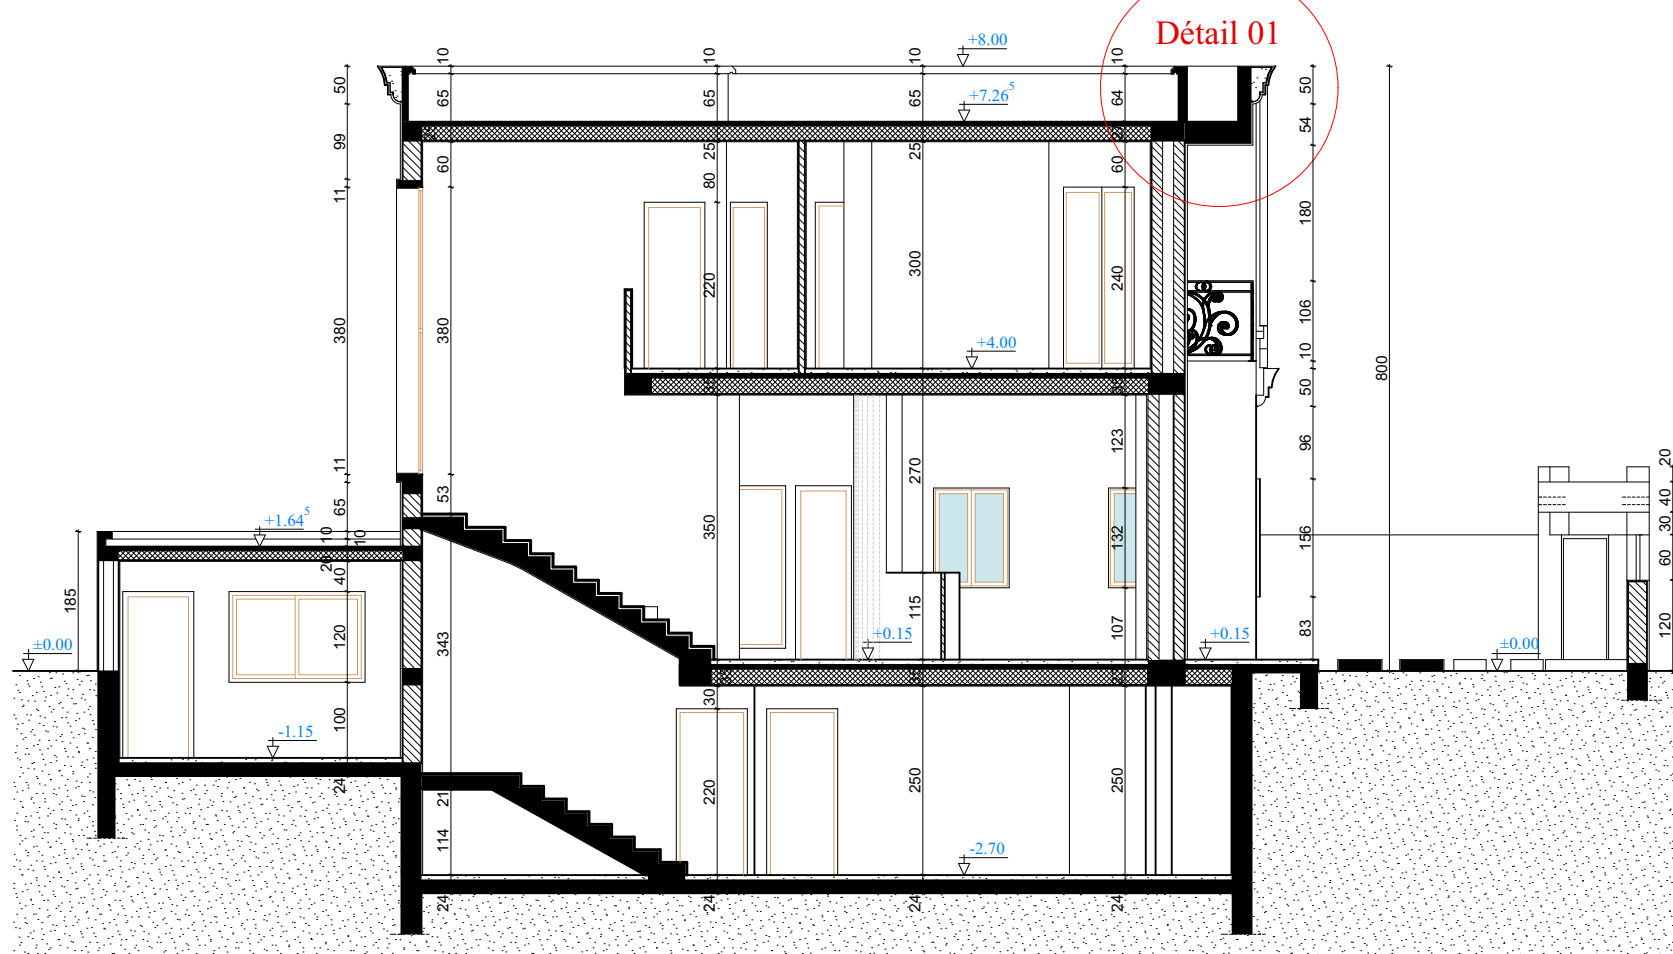


COUPE B-B




PLAN DE SITUATION

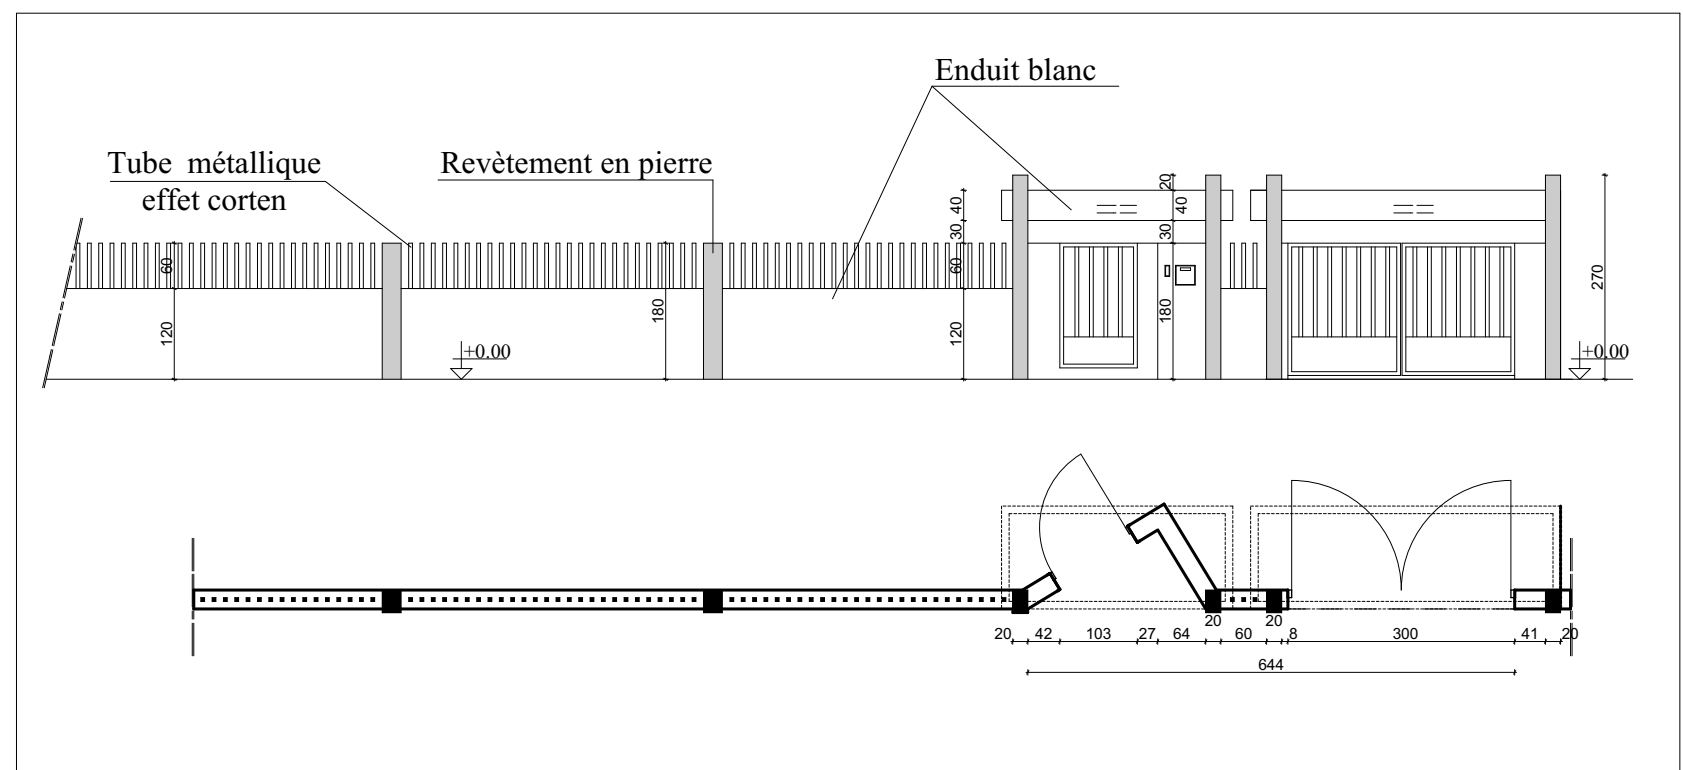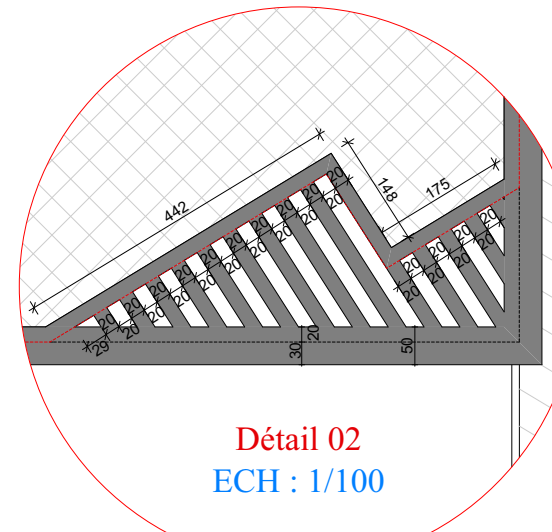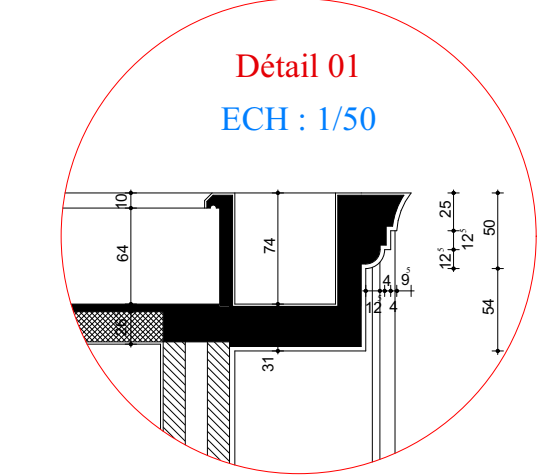


DETAIL MUR CLOTURE

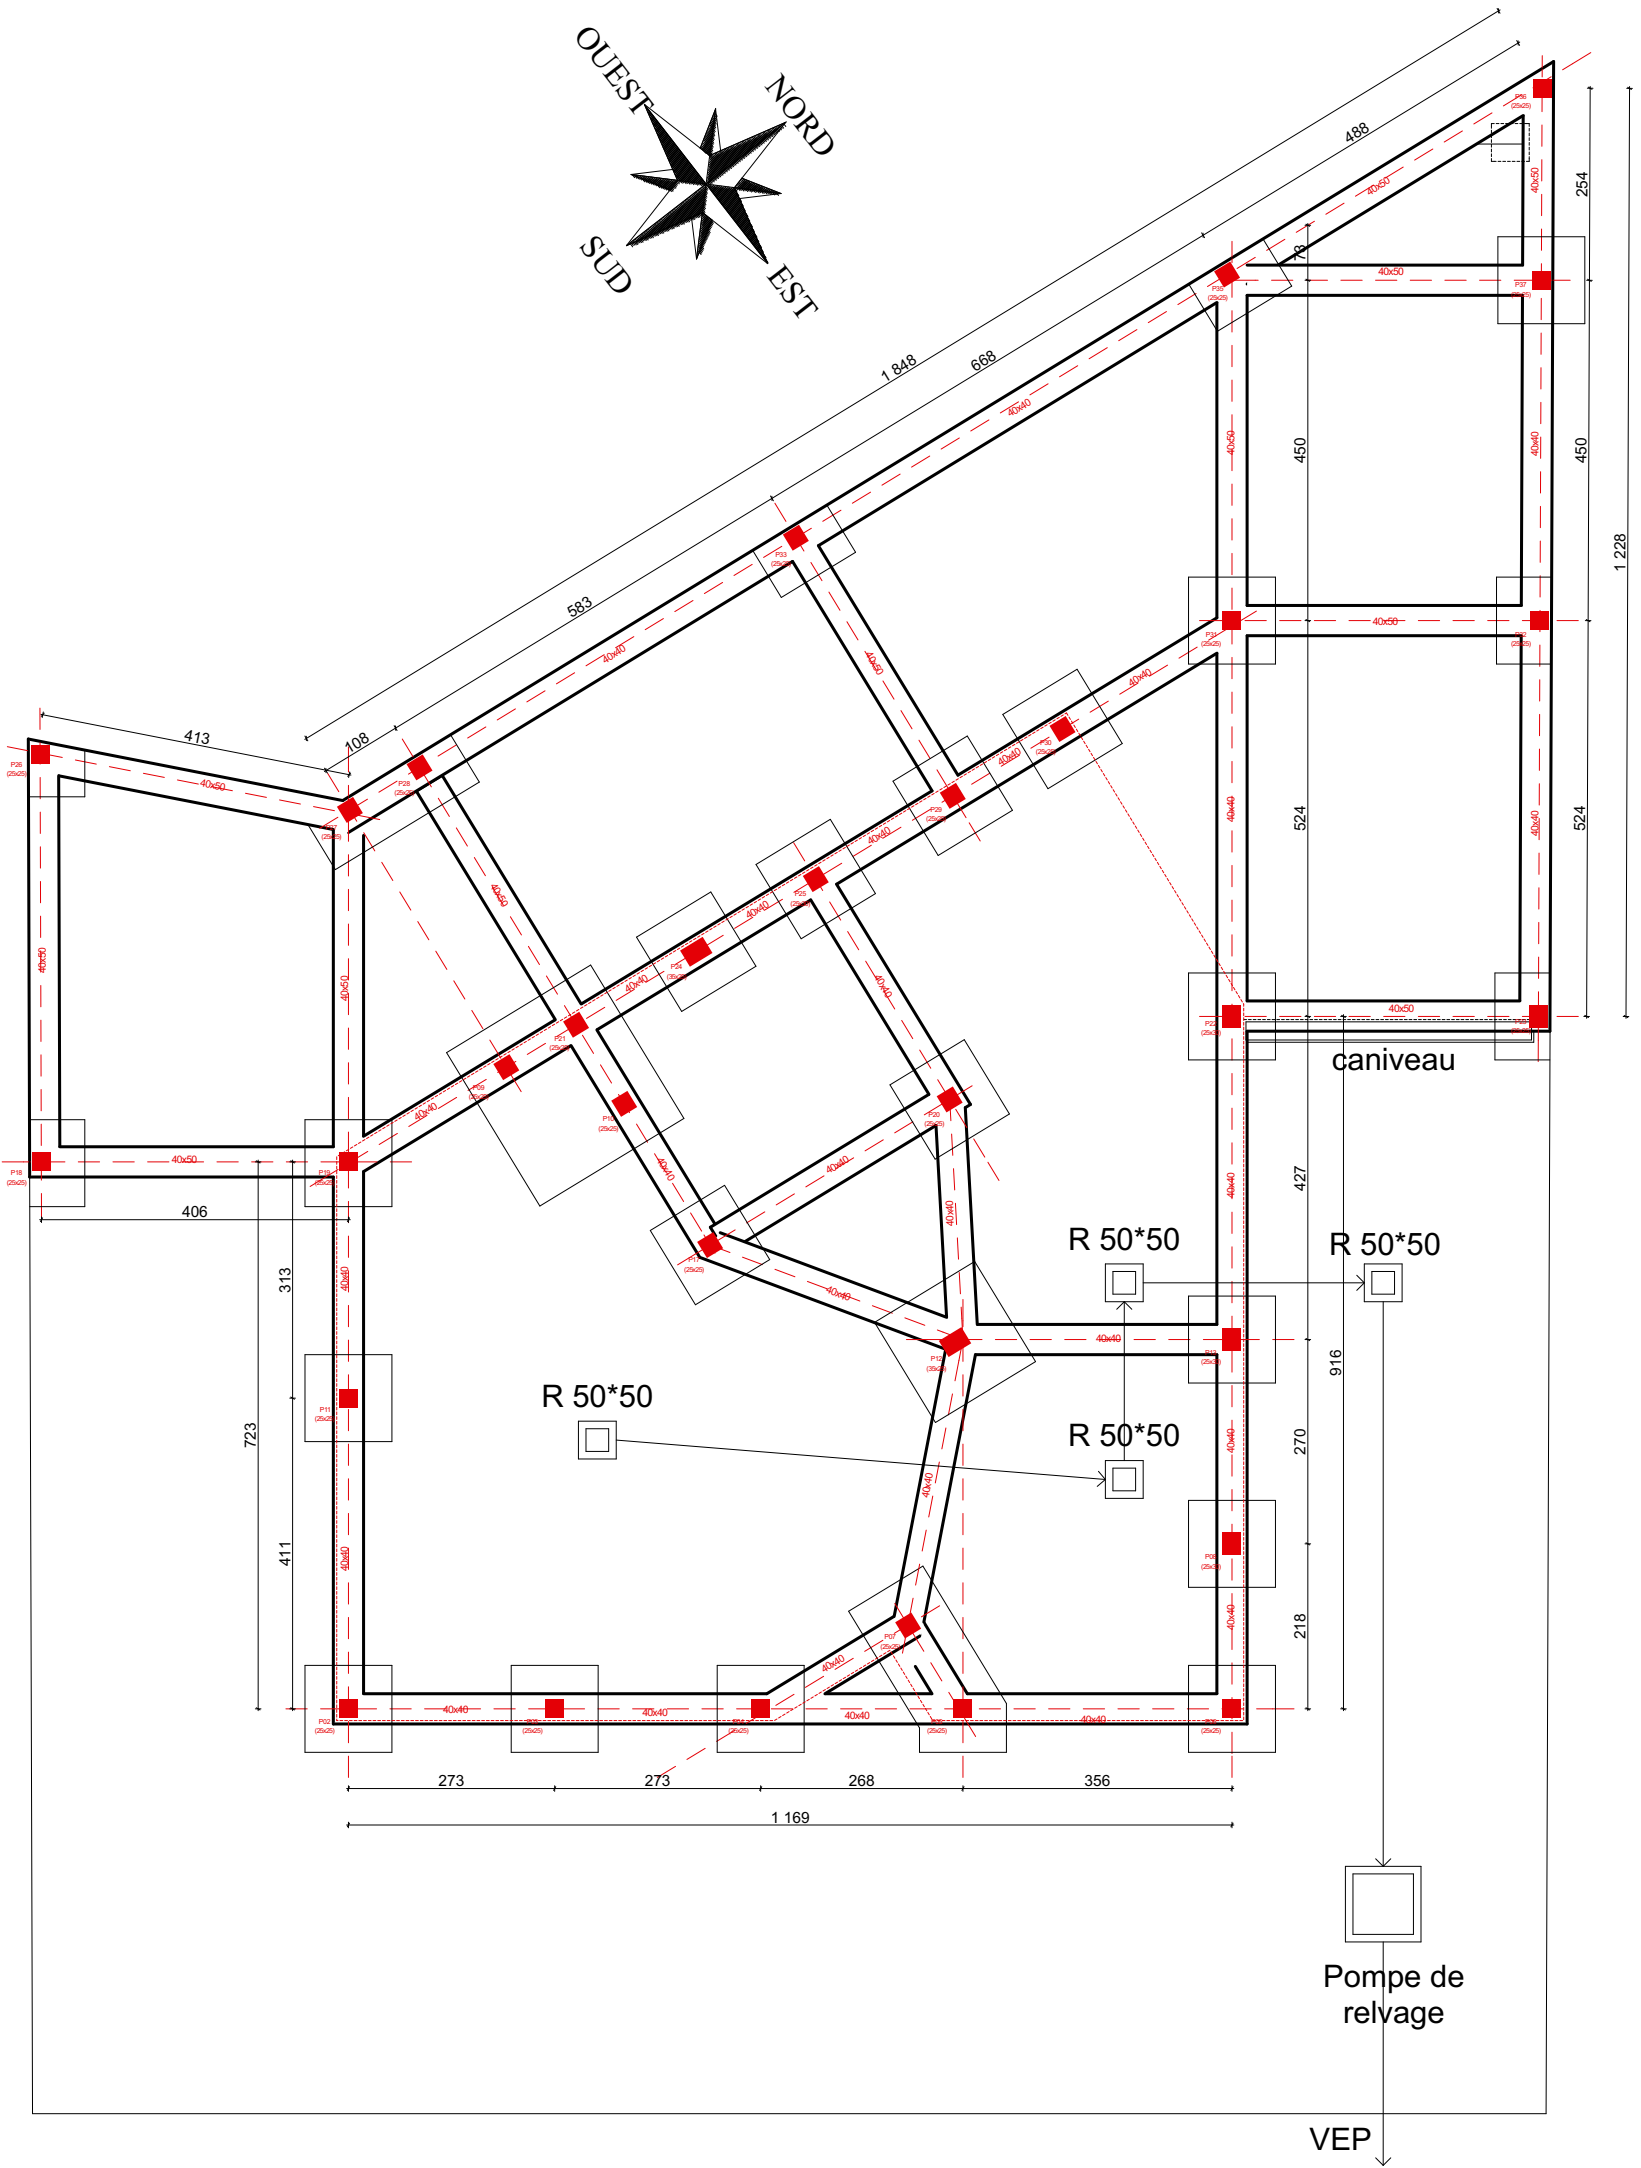


FONDATION

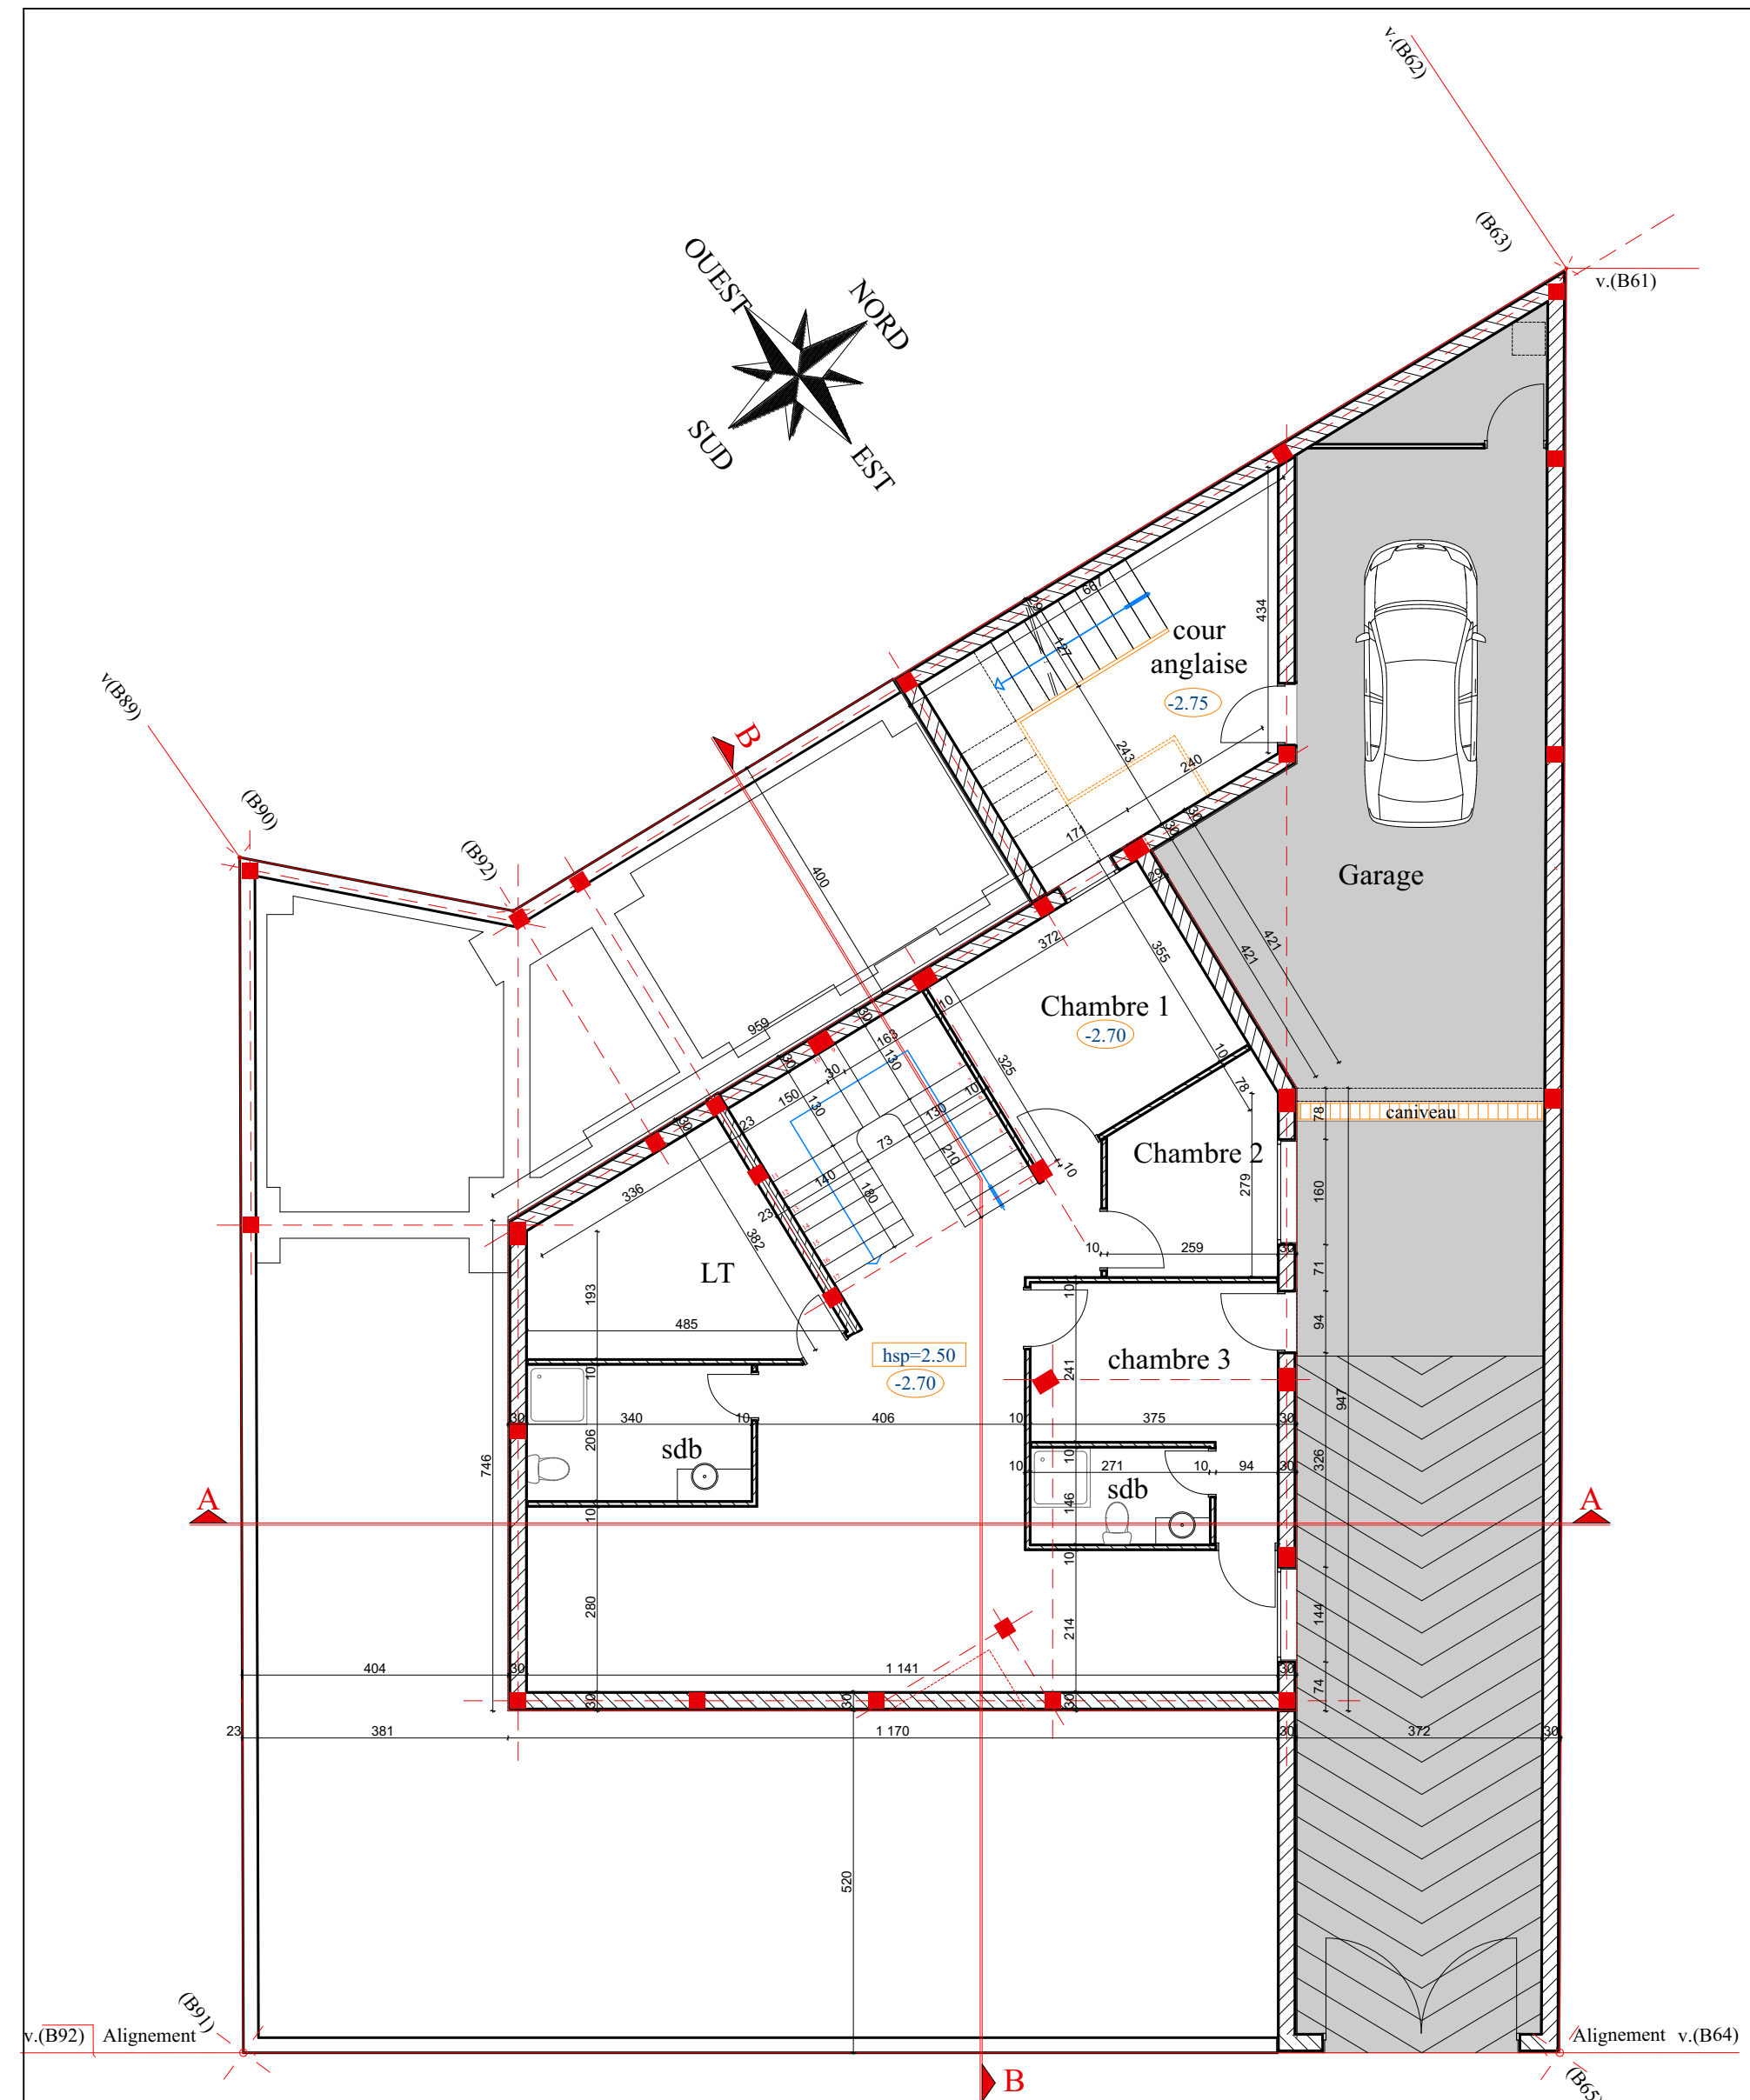


PLAN SOUS SOL

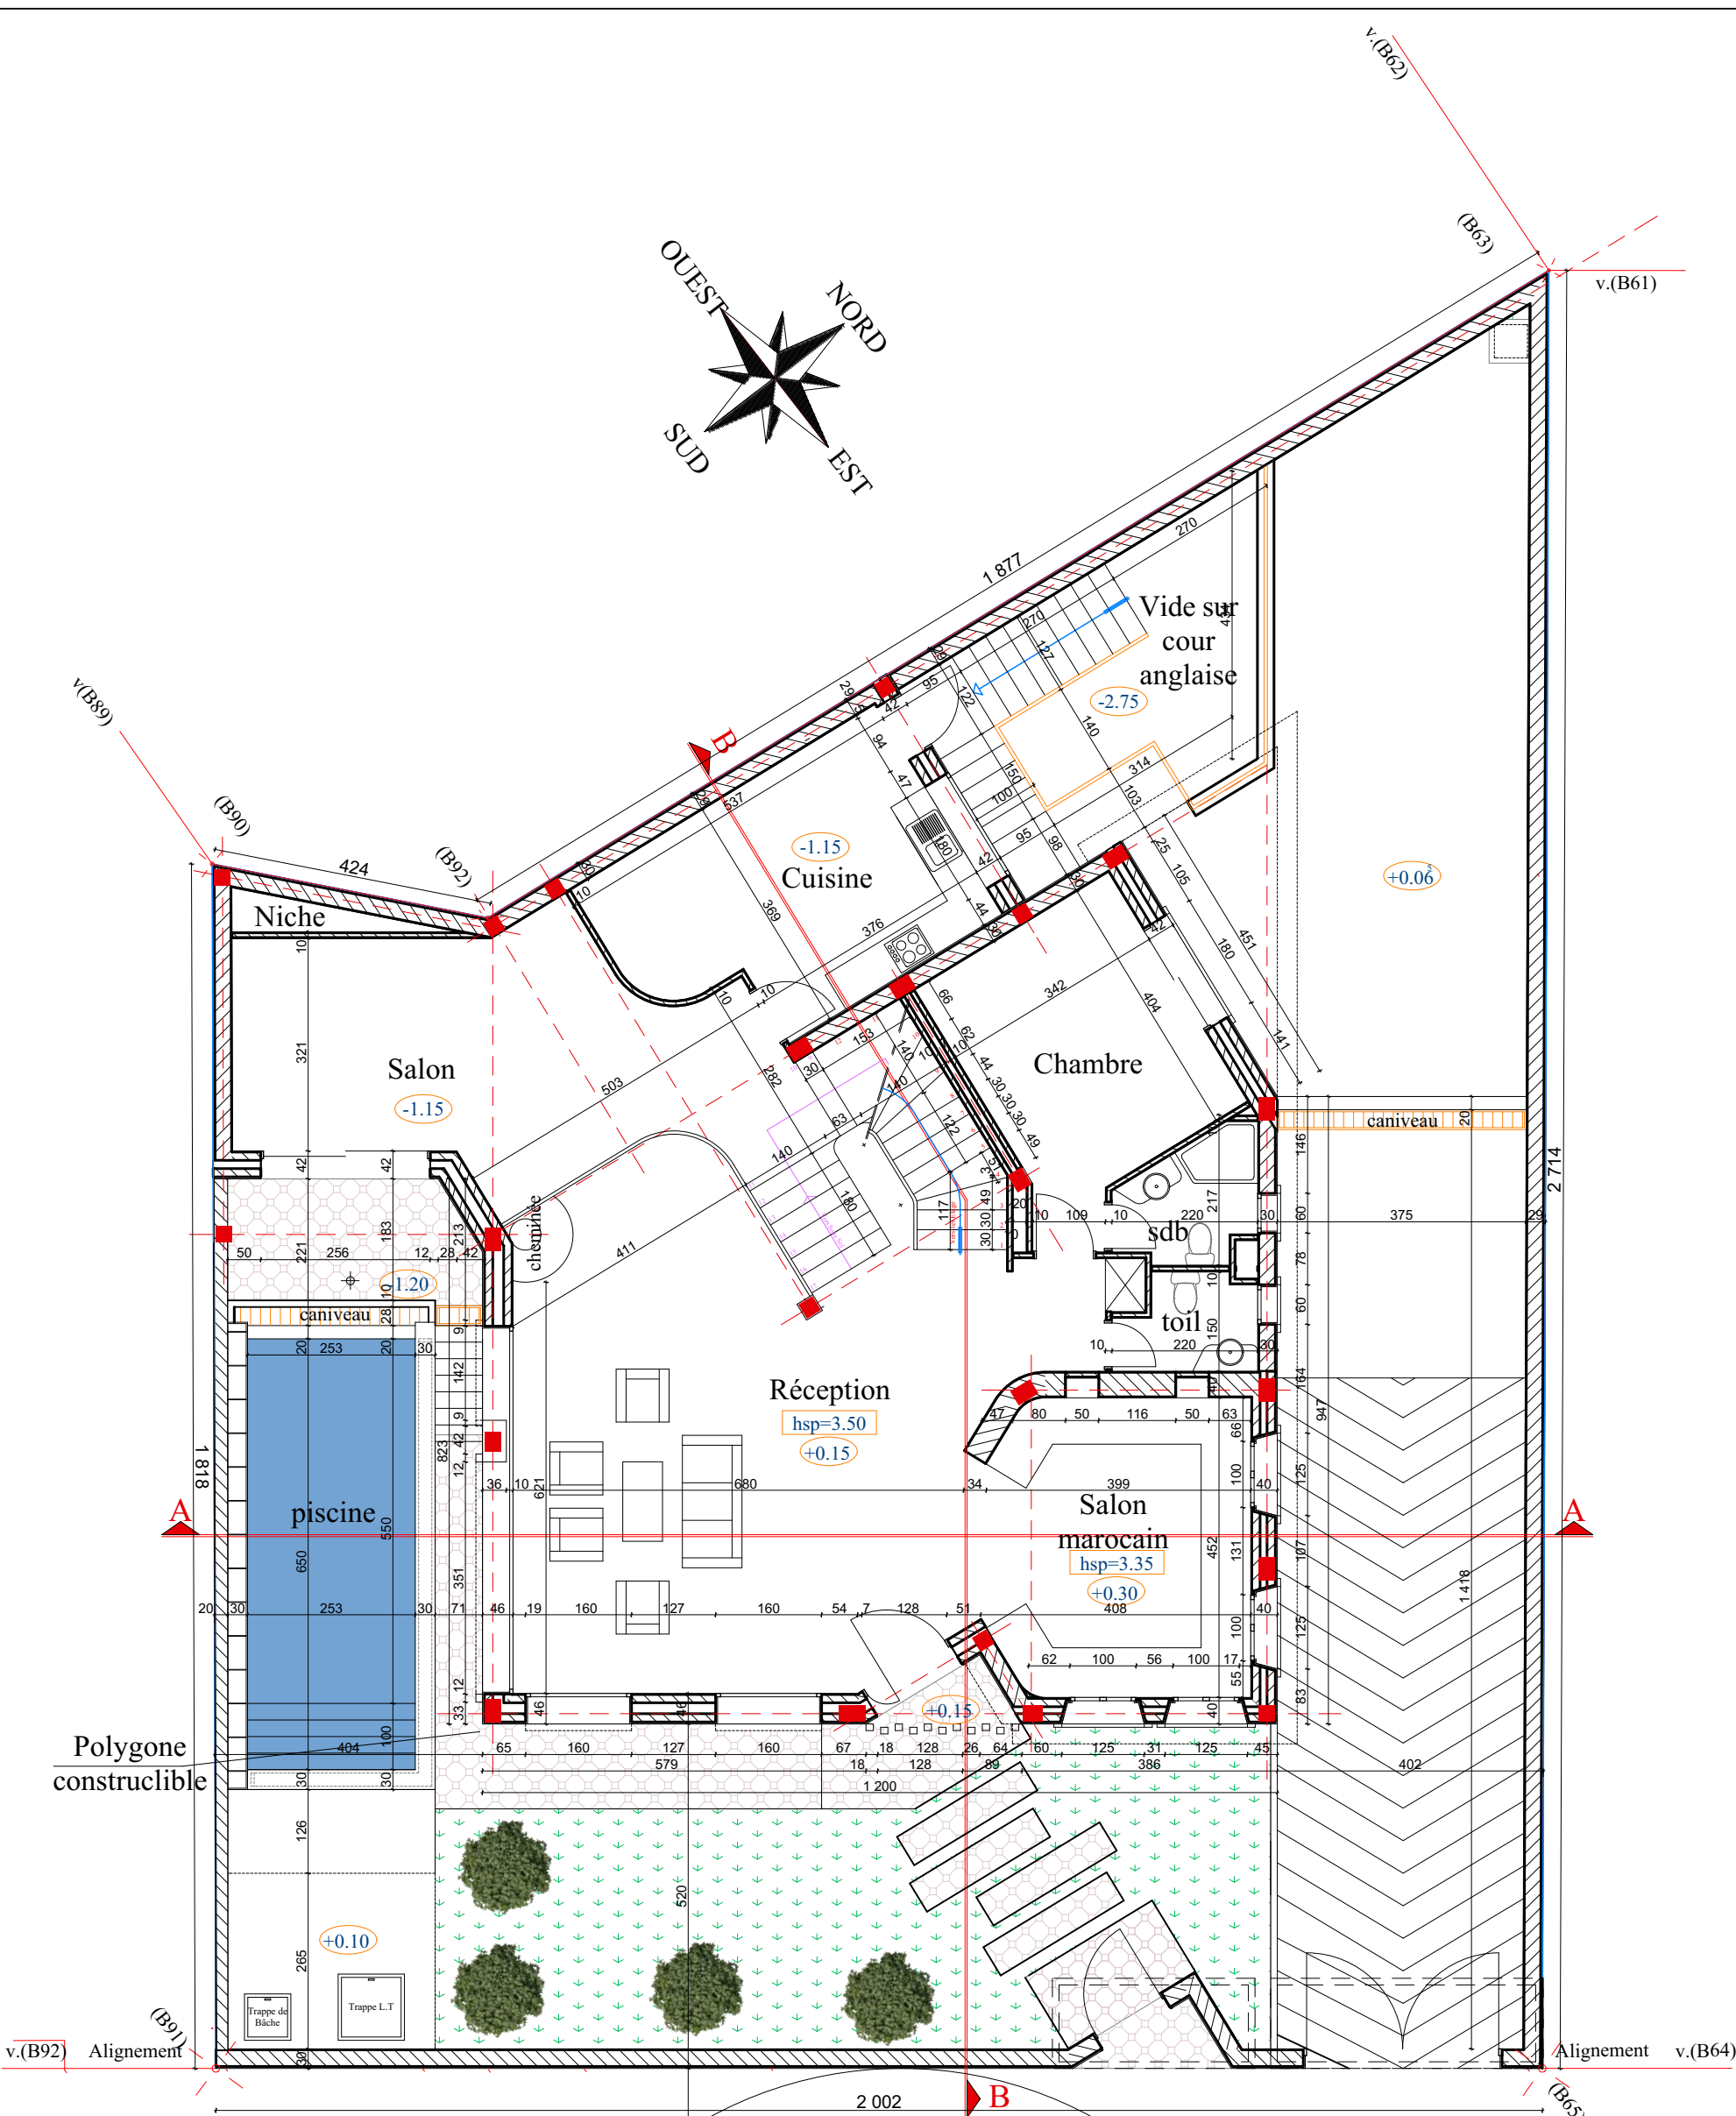

PLAN REZ DE CHAUSSEE

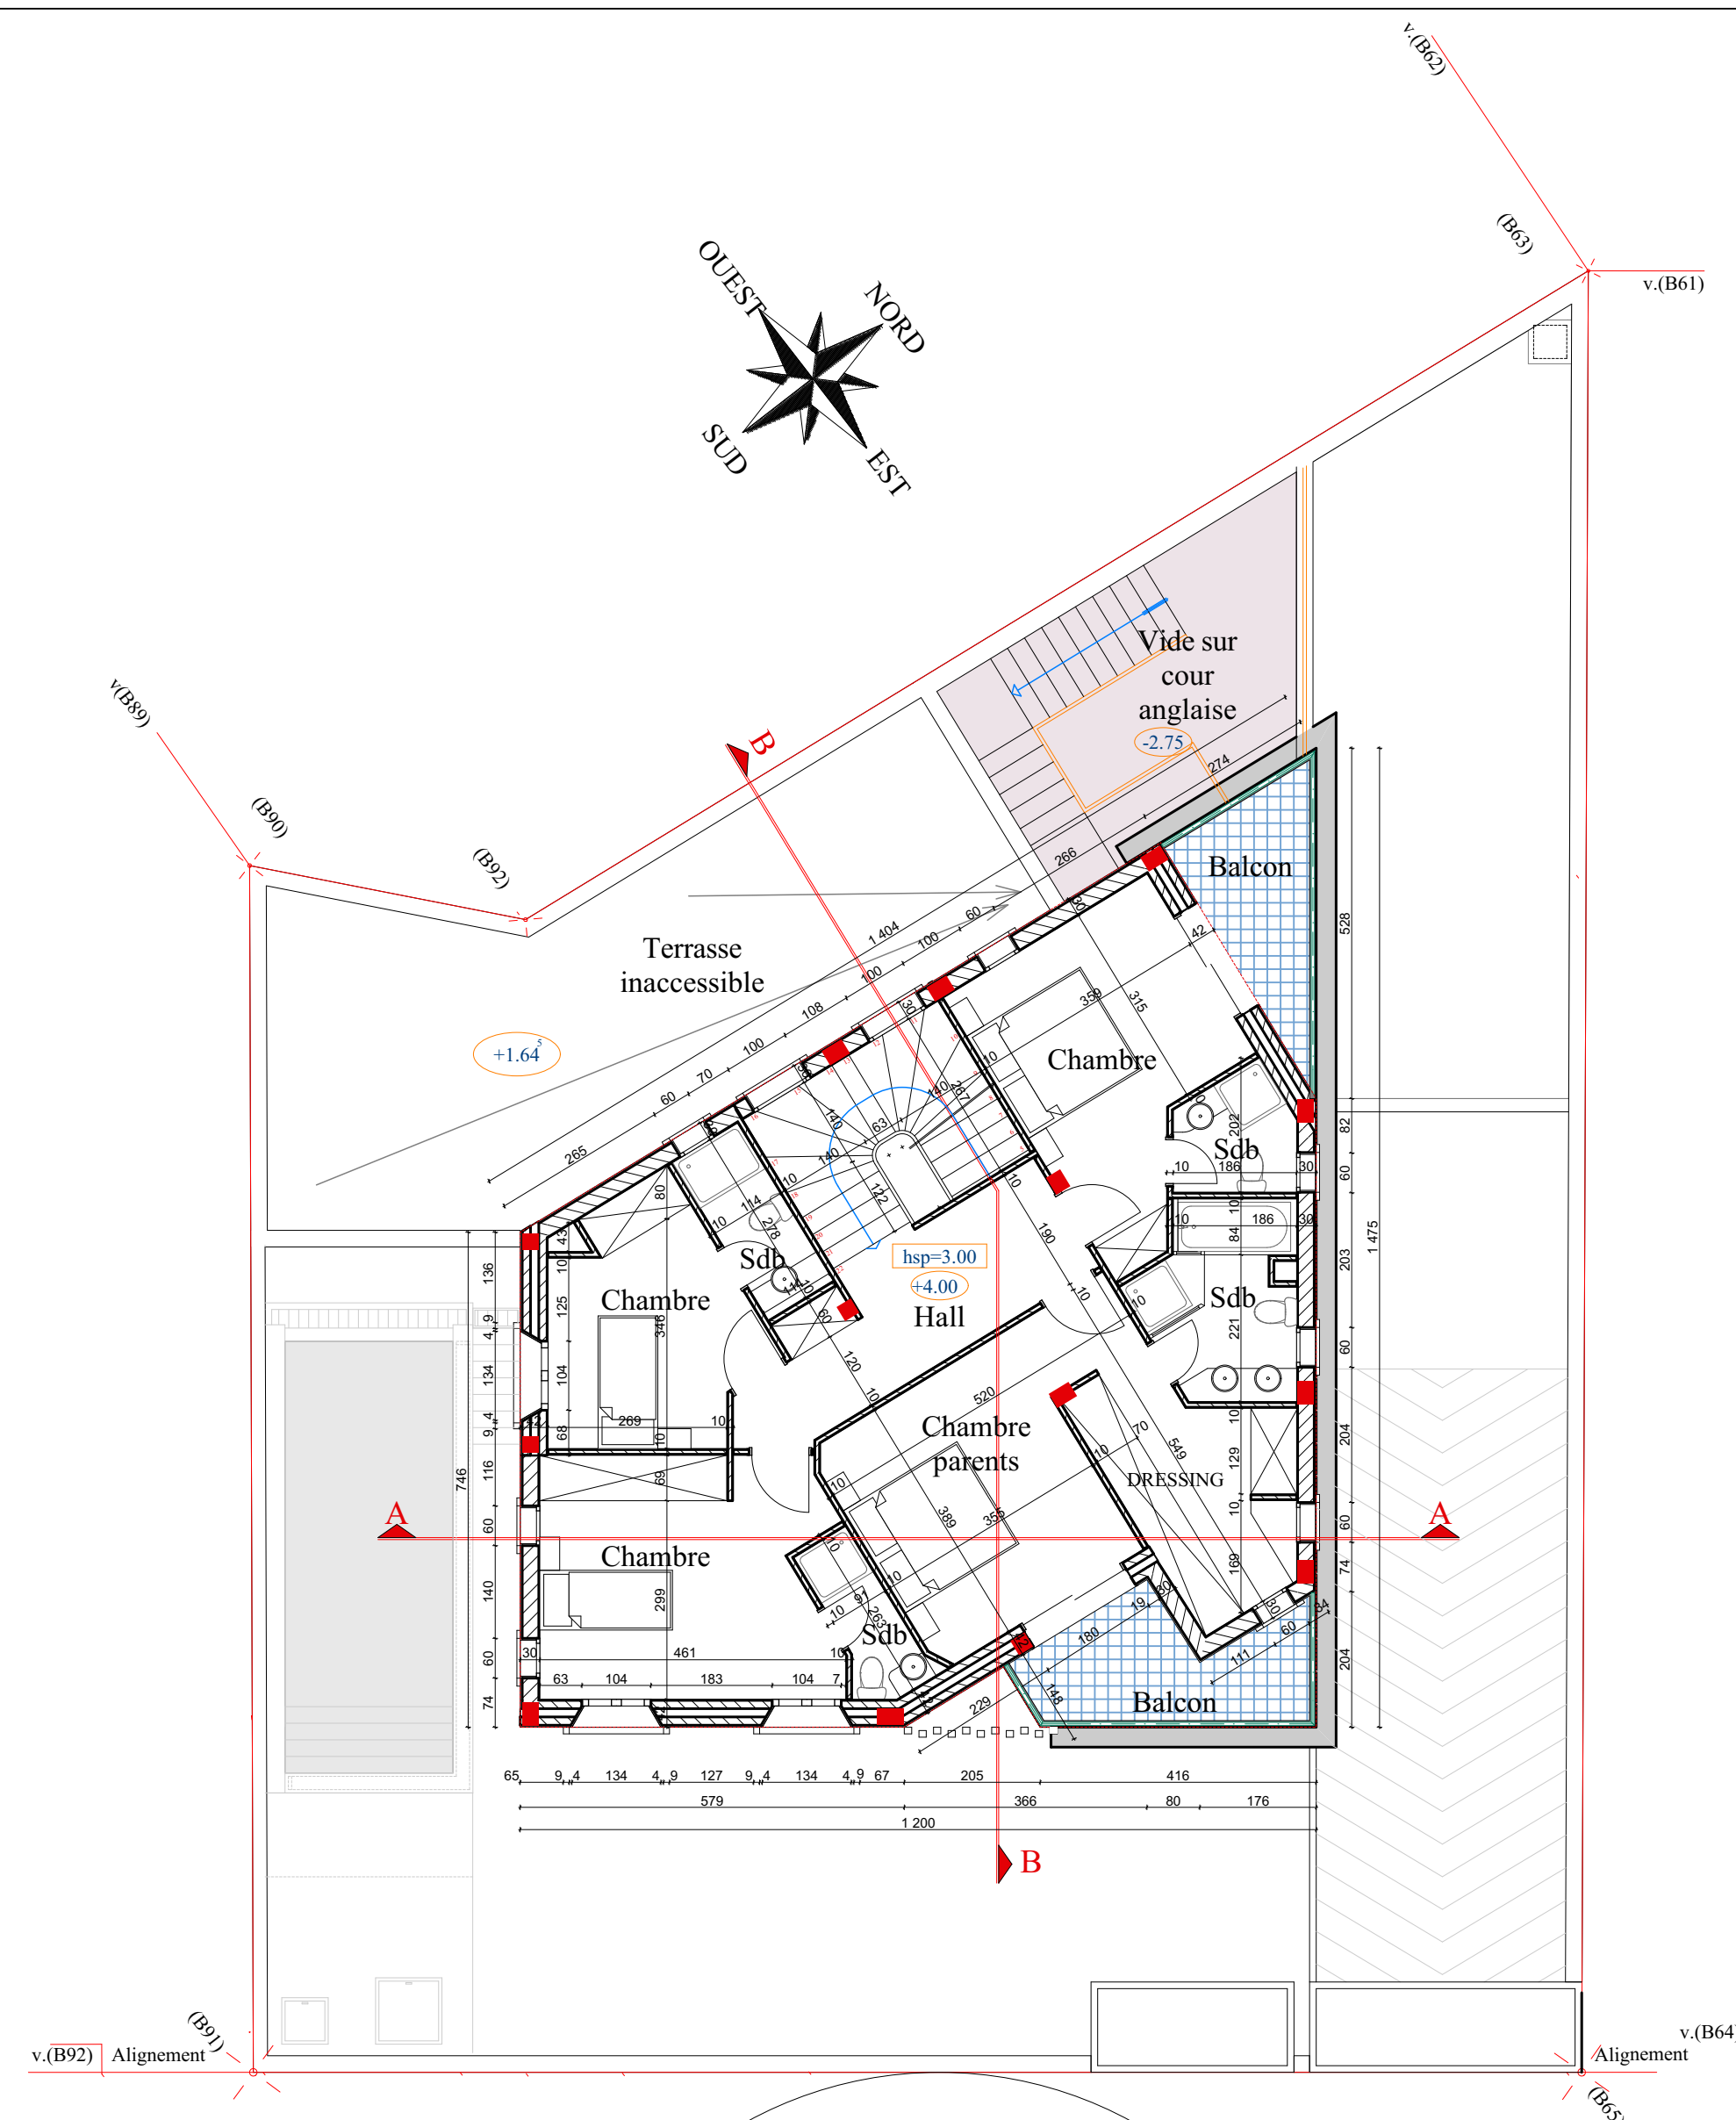


PLAN 1er ETAGE

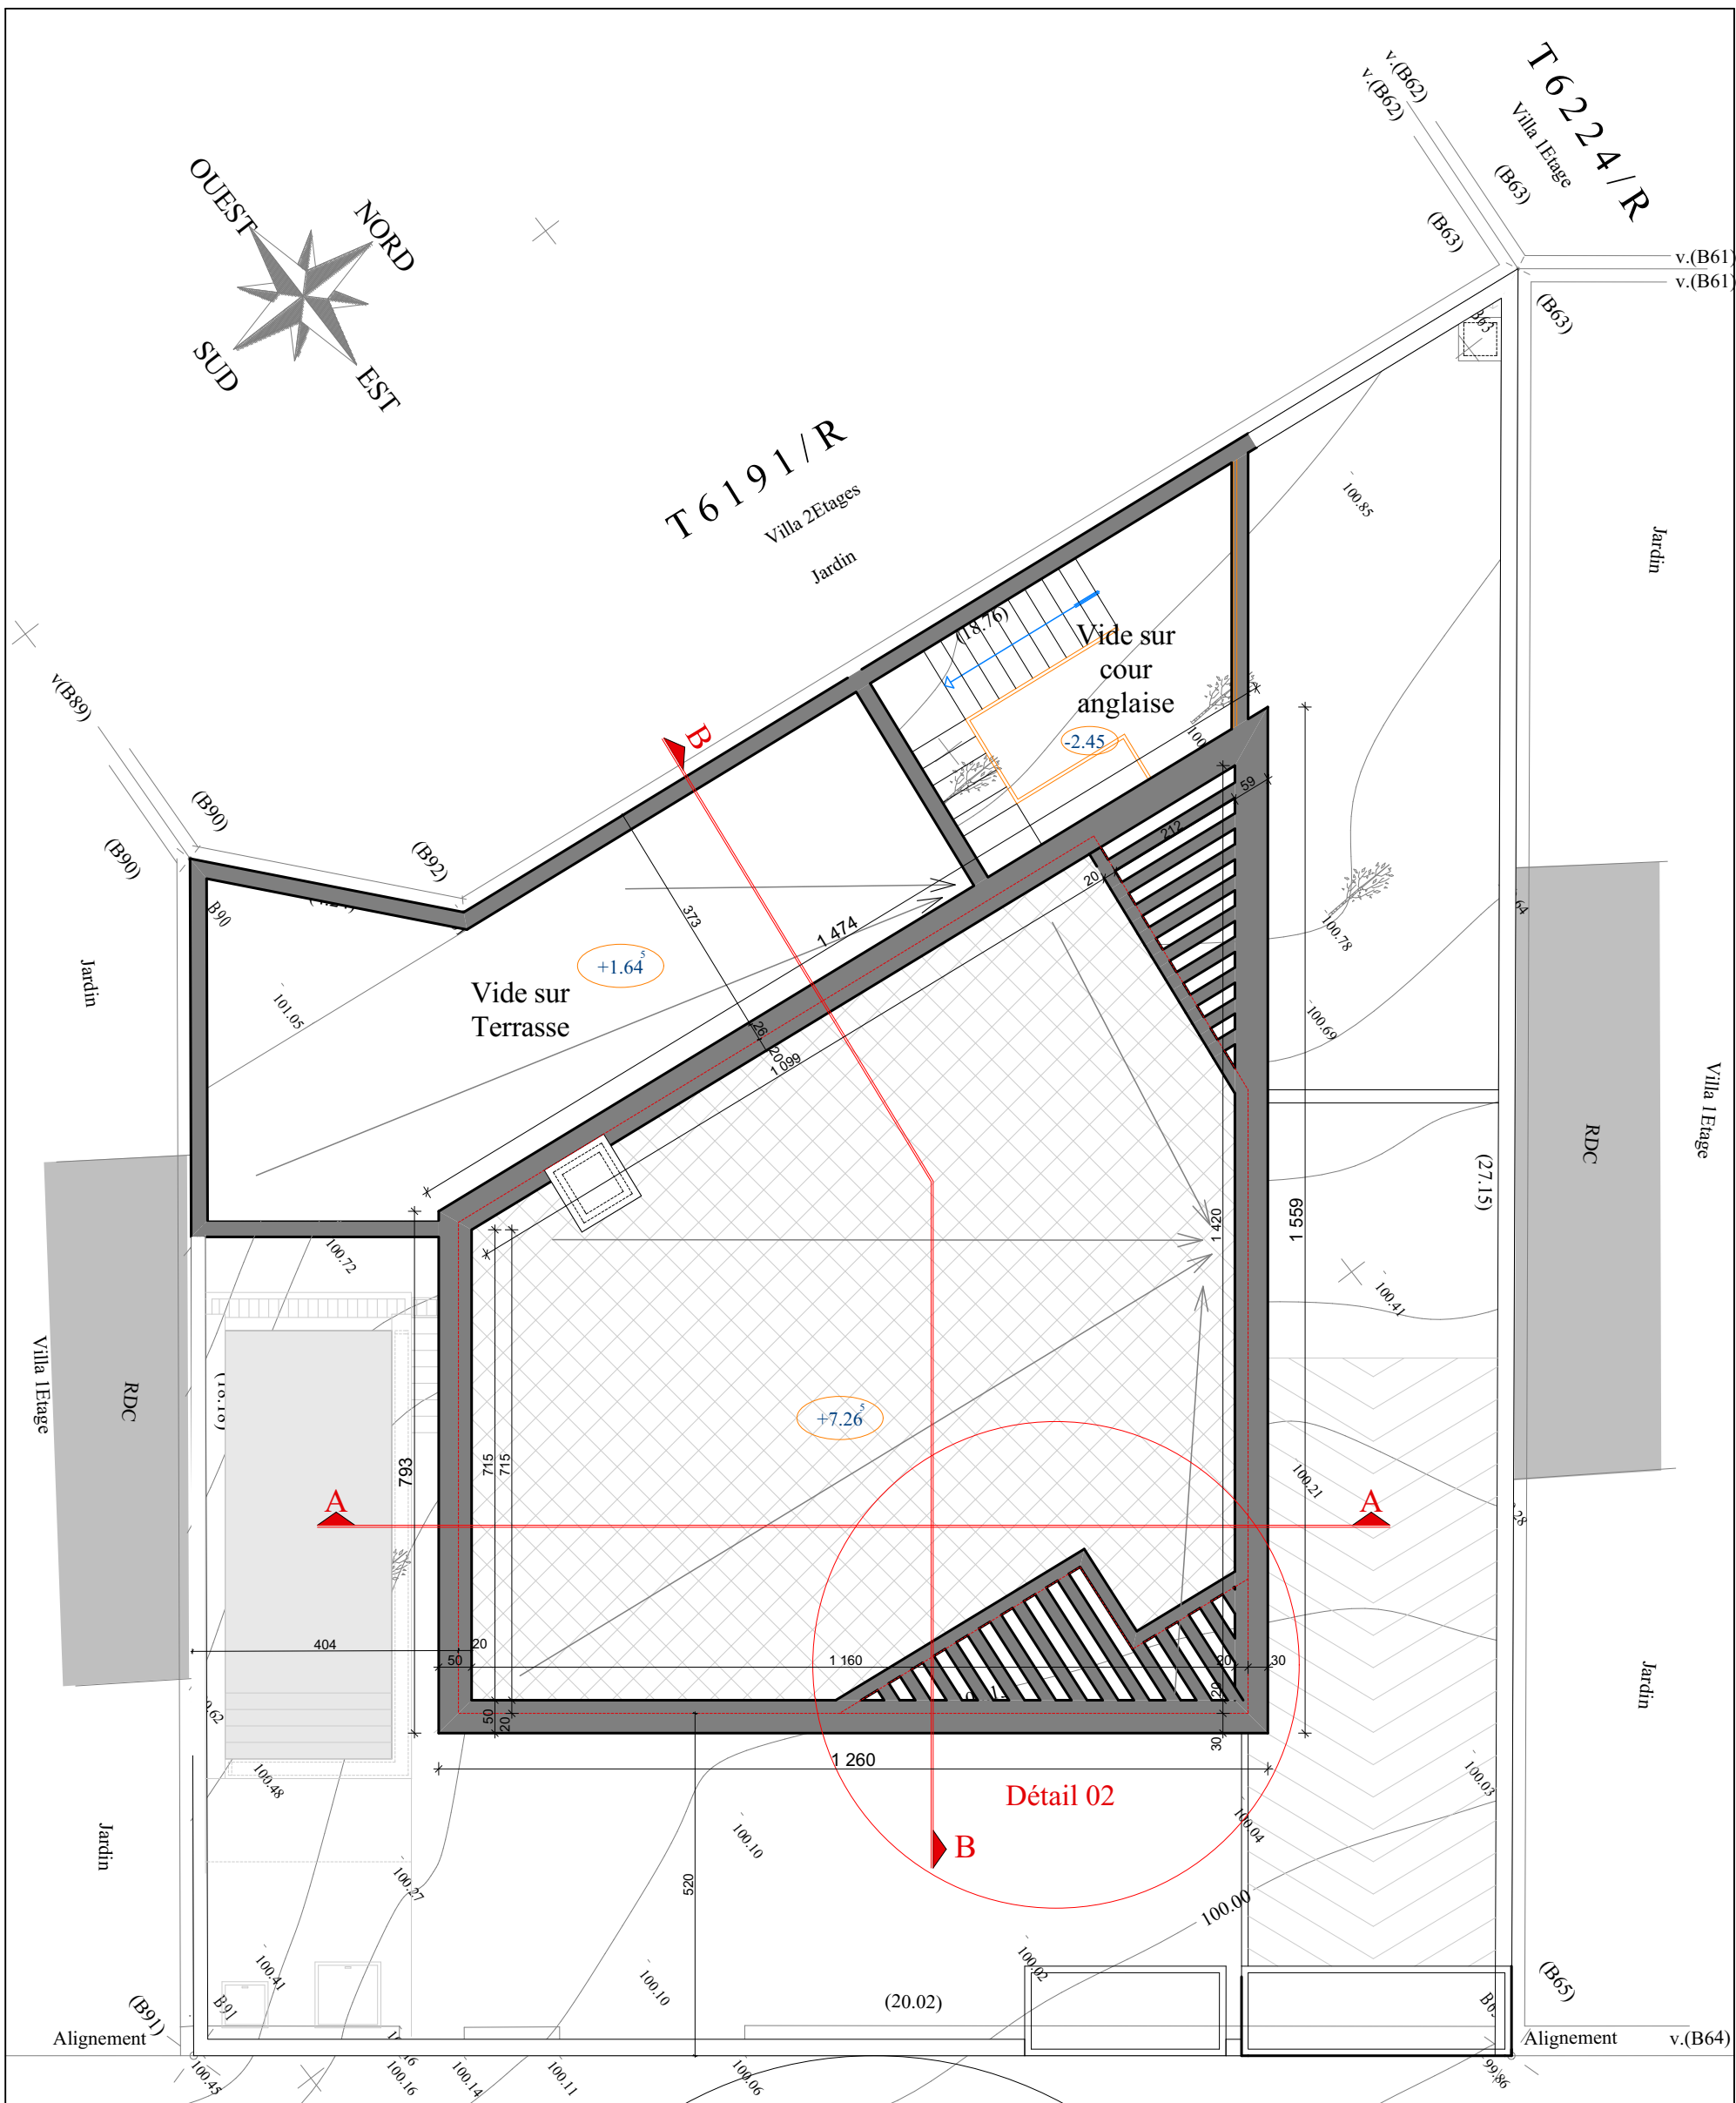


PLAN MASSE-TERRASSE


PROJET DE CONSTRUCTION D'UNE VILLA EN R+1

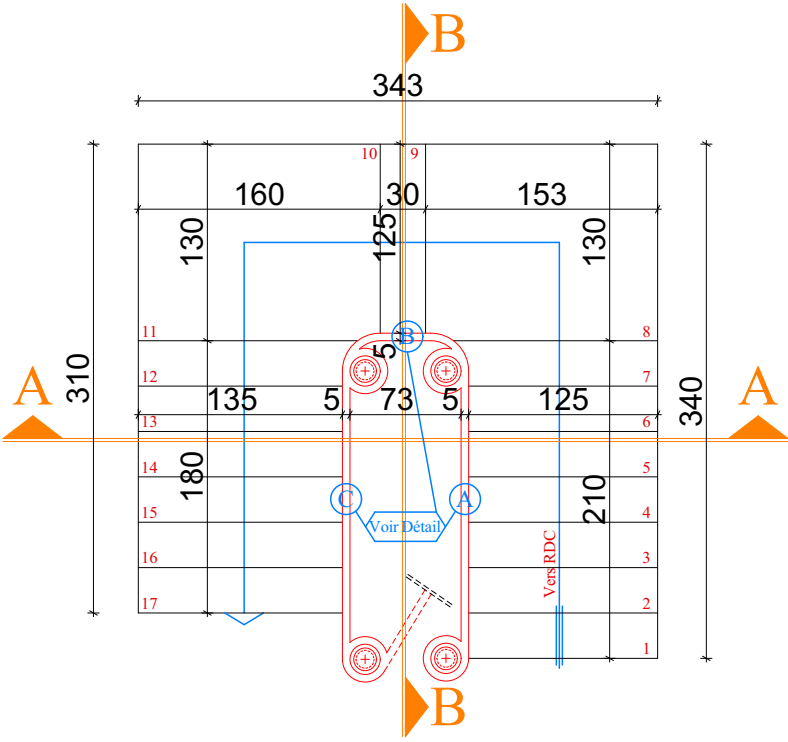


Plan escalier Sous Sol

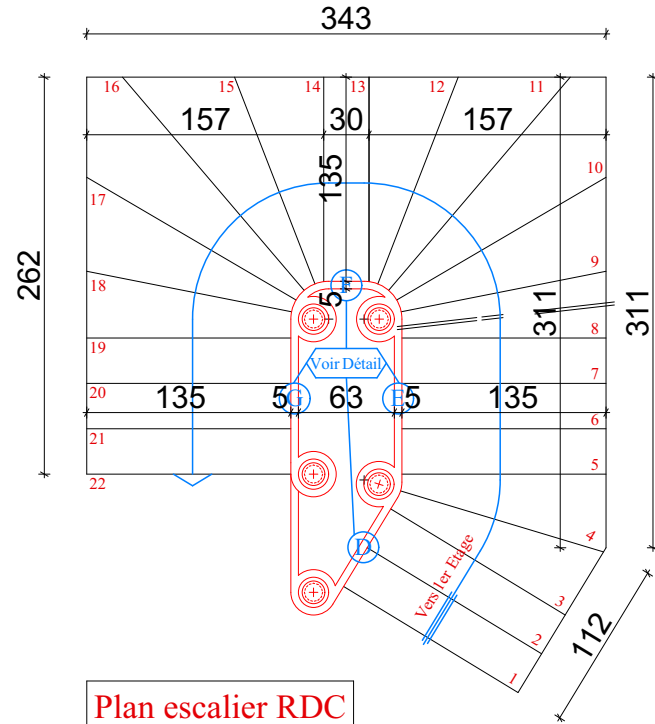


Plan escalier RDC

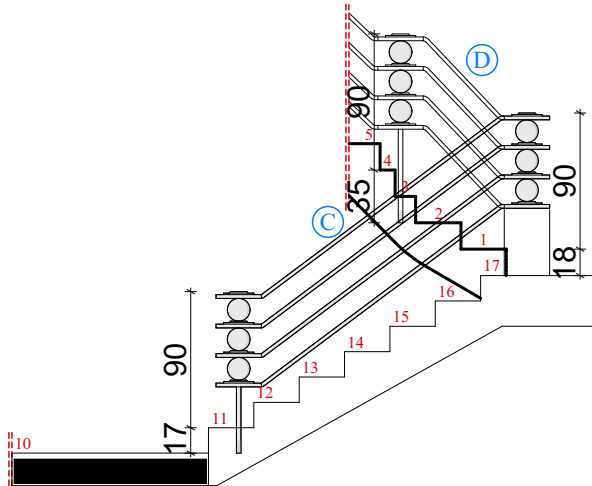


Détail C et D

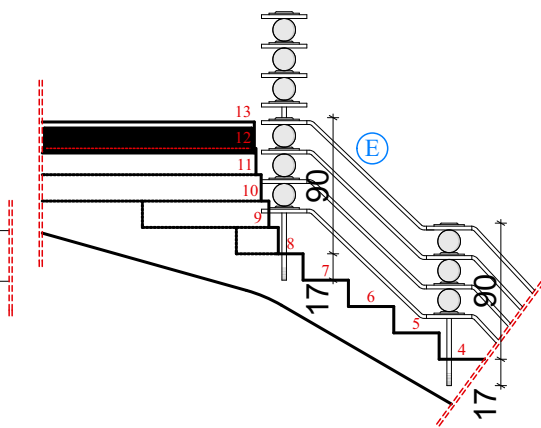


Détail E

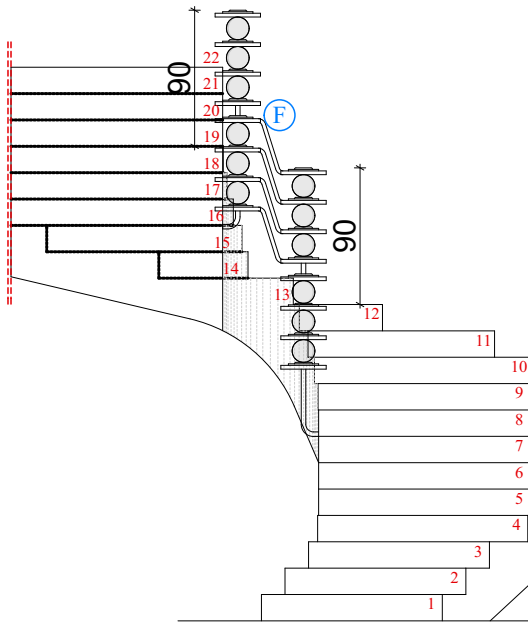

Détail F

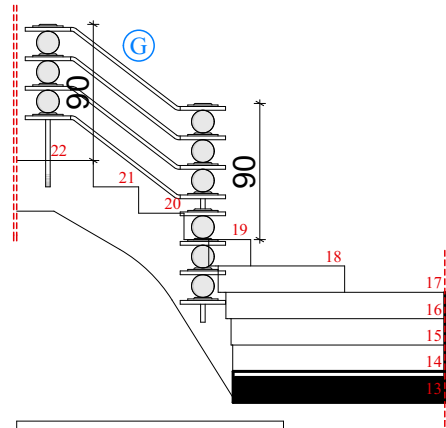


Détail G

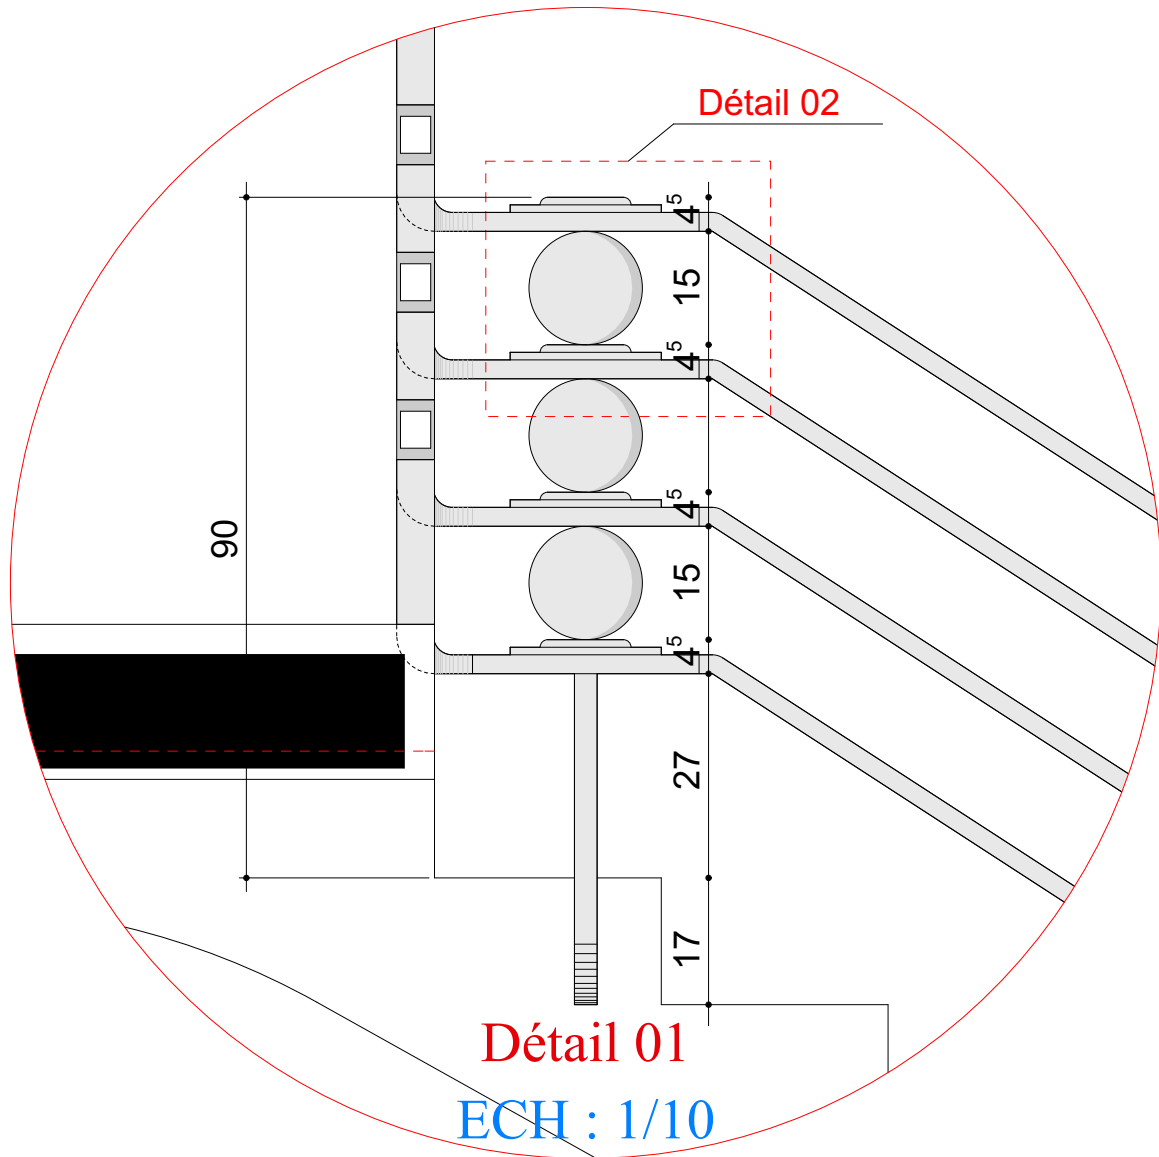

Détail 01

ECH : 1/10





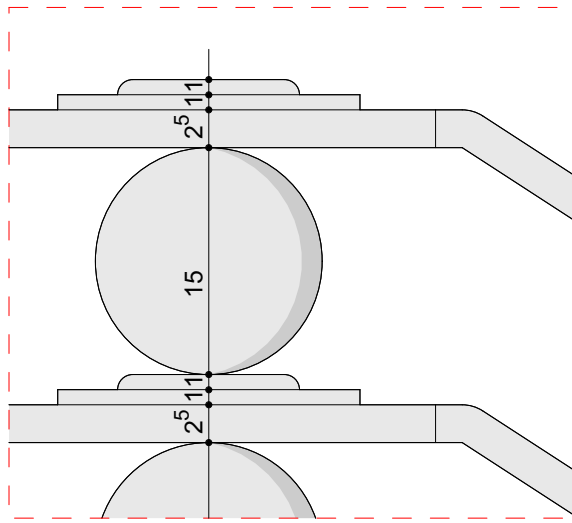



Détail 02

ECH : 1/5

ECH : 1/50

PB1	Spécifications Bois	Date : 04/08/2016
	PROJET DE CONSTRUCTION DE L'ENSEMBLE ARTISANAL DE LA VILLE D'OULMES	Echelle : 1/20
		S.sol: ☐ RDC: ☒ Etage: ☐ Terrasse ☐
		Faux Cadre: 120x30 mm
Porte type : PB1		Cadre : 150x55 mm
Dimensions: 180x220 hc		Chambranle: 100x20 mm
Type d'ouvrant : 2 vantaux ouvrant à la française		Quantité: 10
Panneau d'ouvrant : sebnya sur 2 faces		Localisation : ensemble artisanal RDC :magasins
Quincaillerie :		

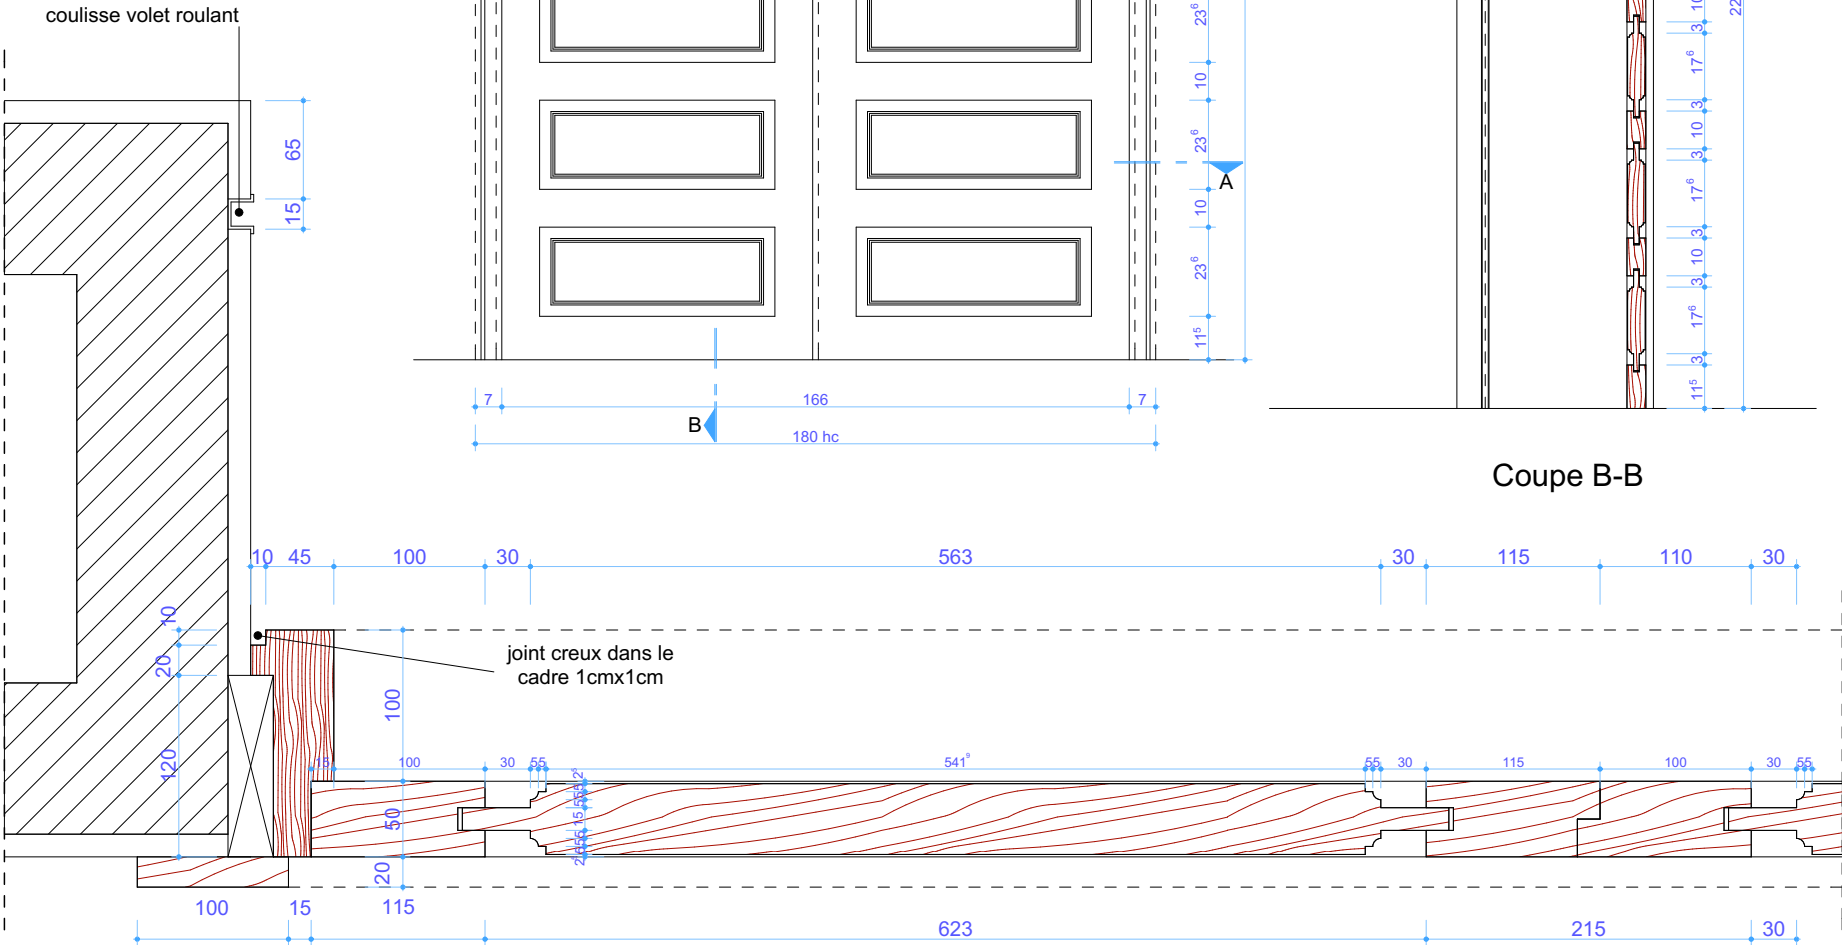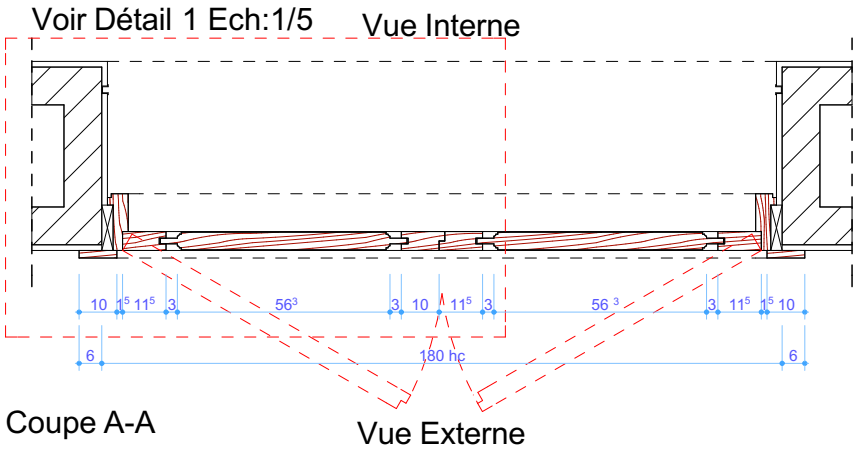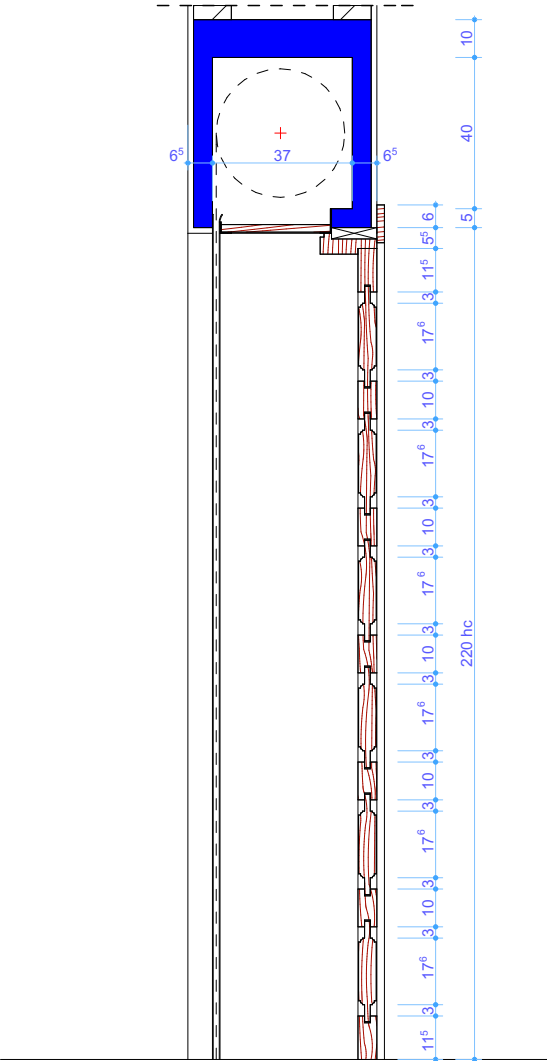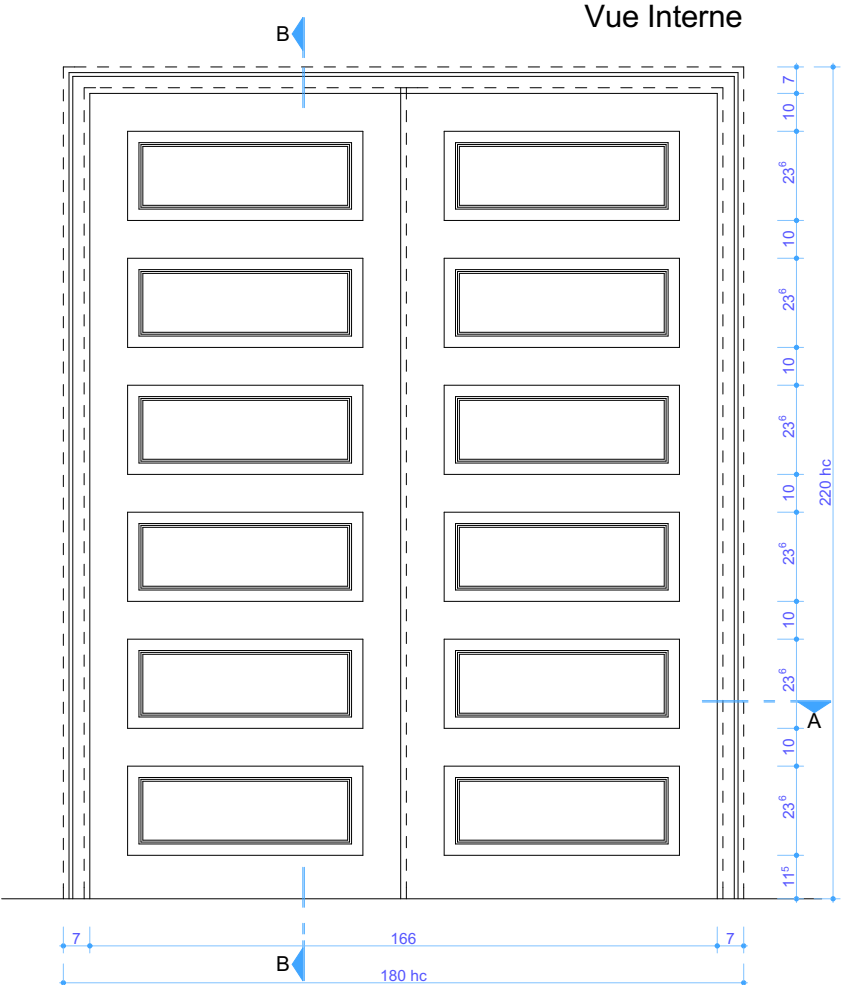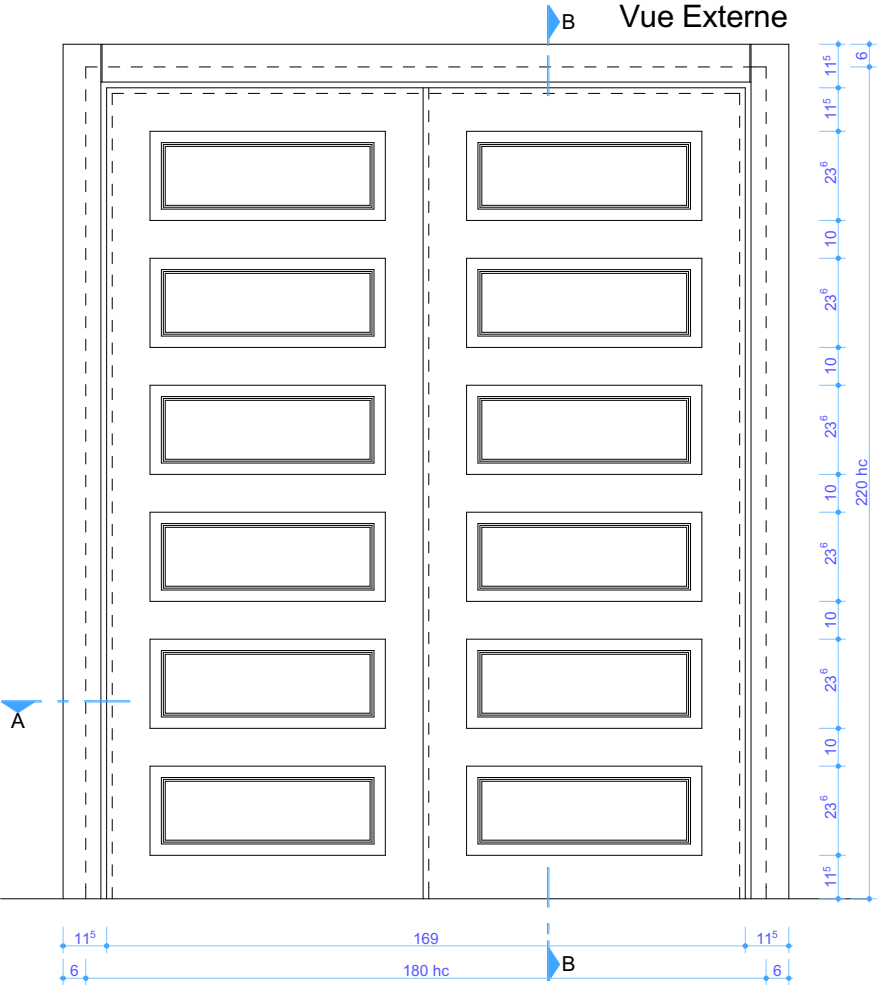

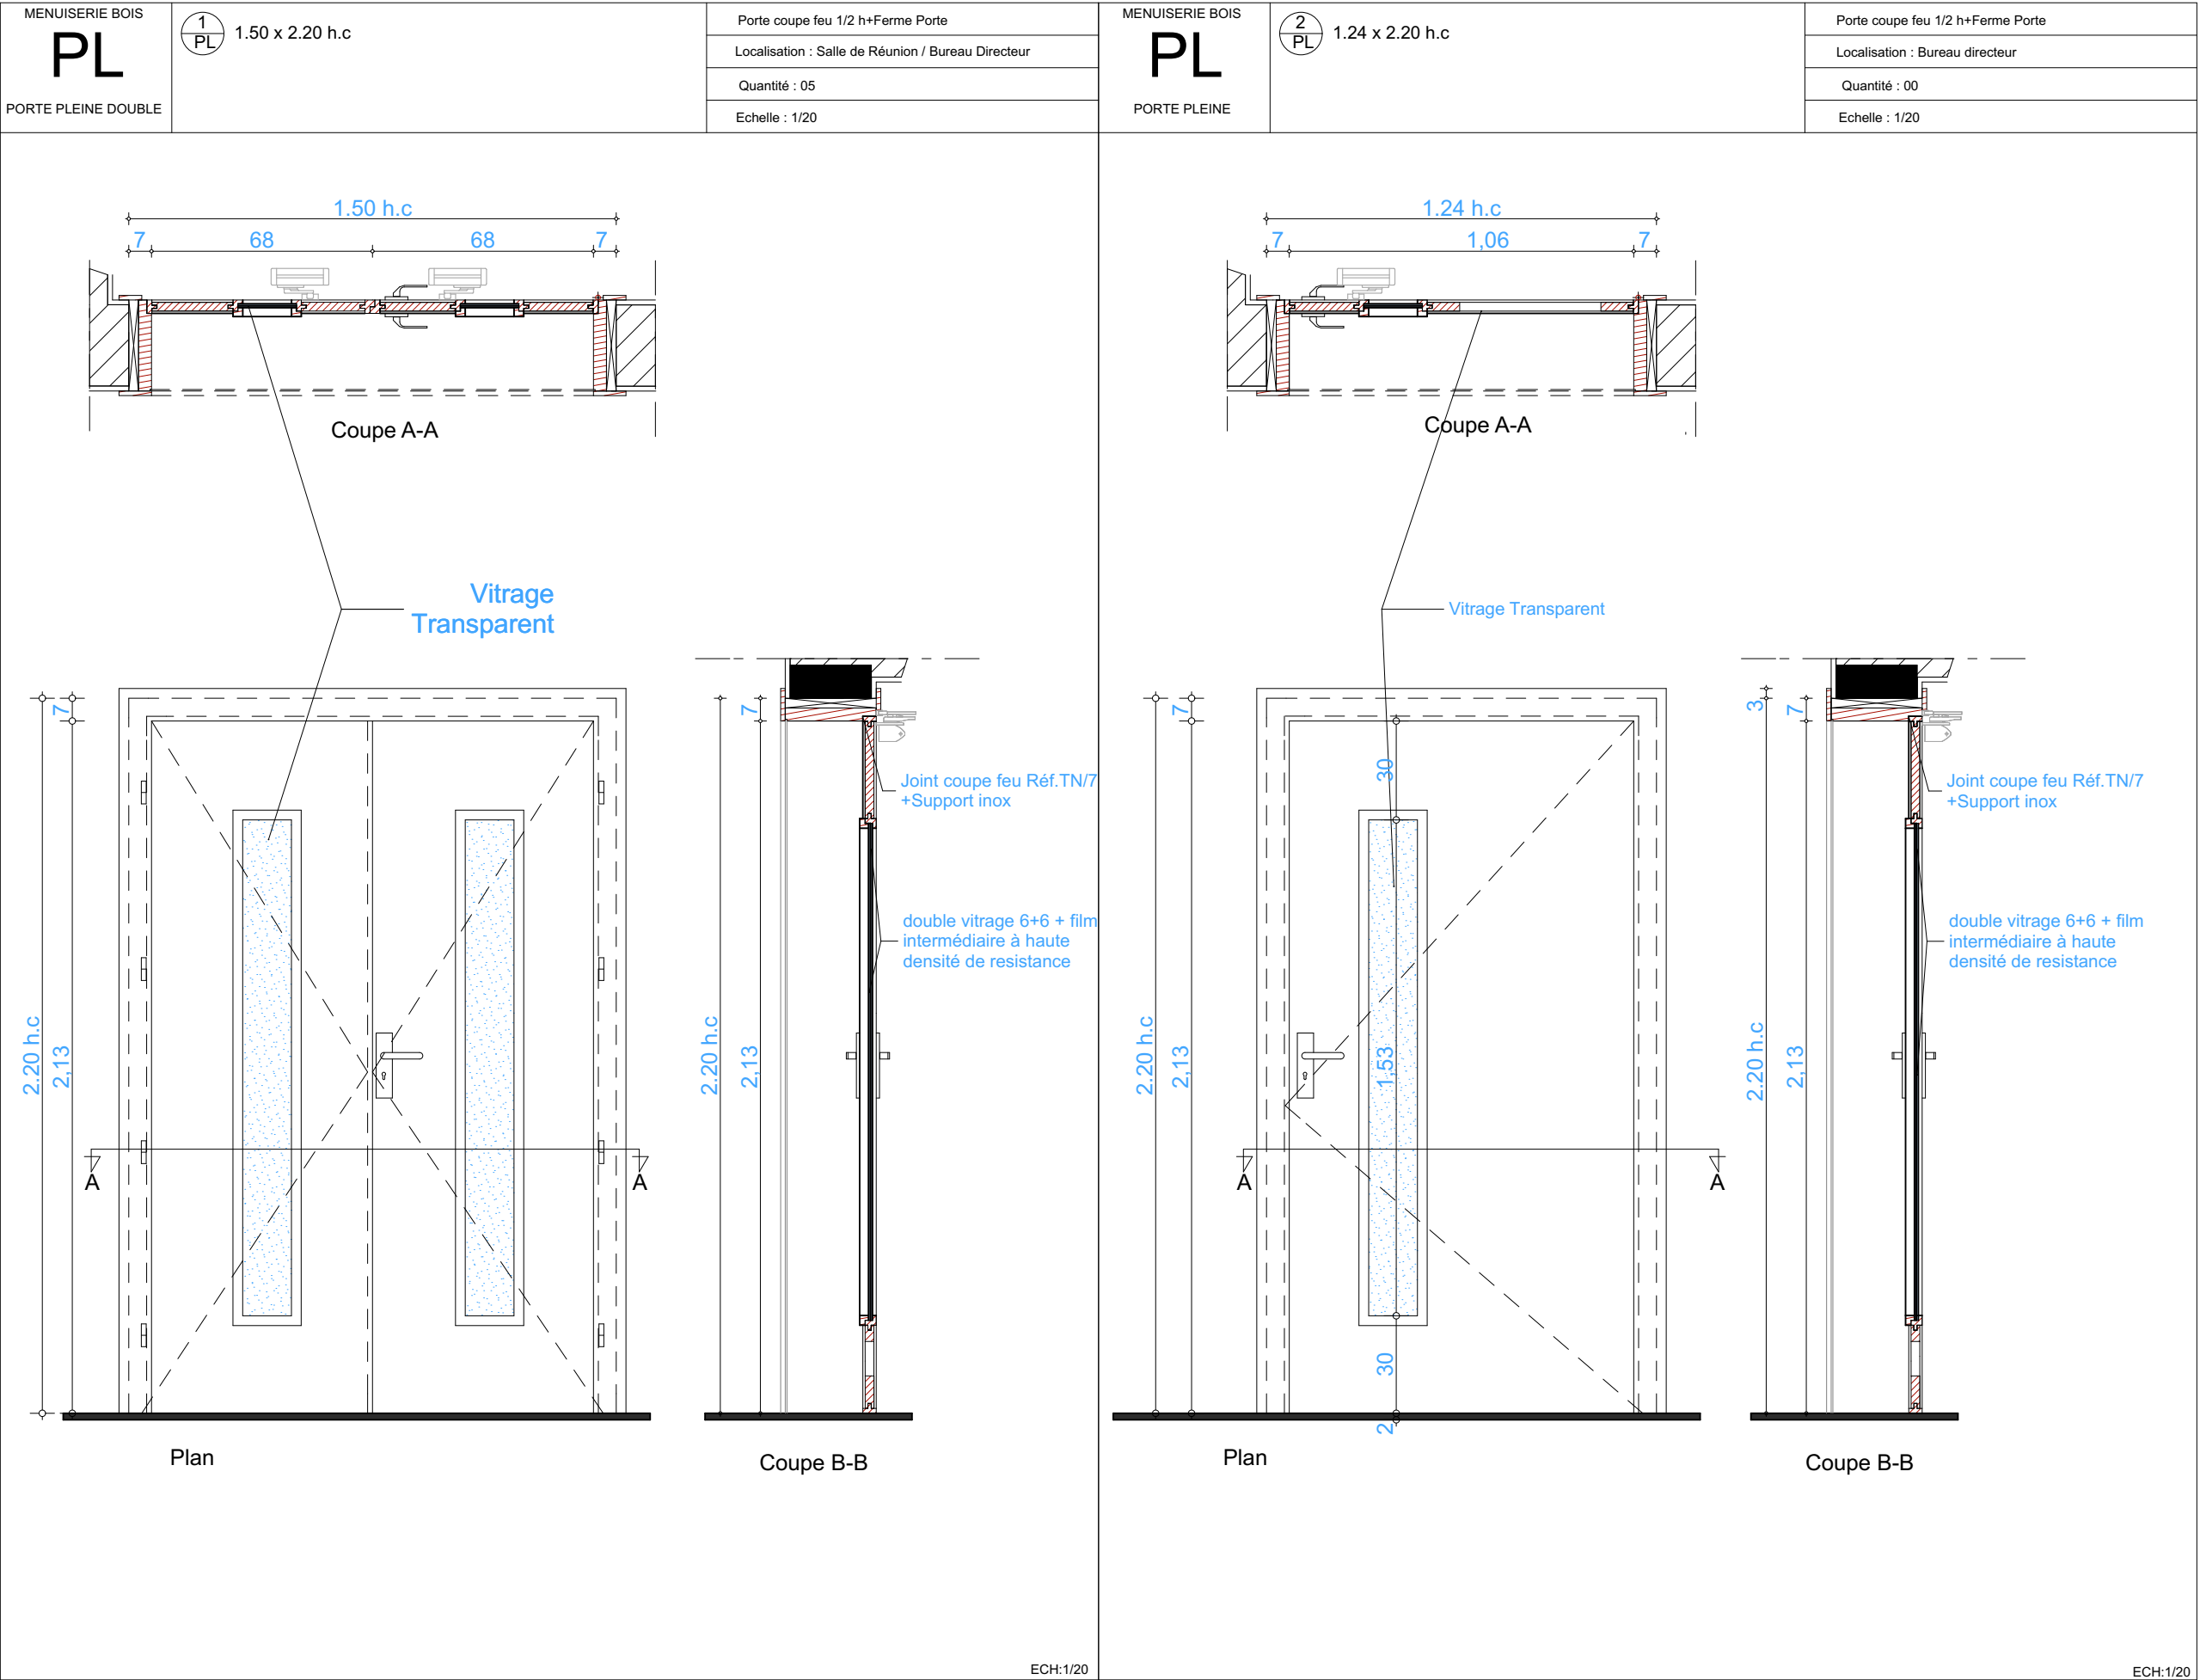

MENUISERIE BOIS

PS

1

PS

1.04 x 2.20 h.c

Porte coupe feu 1/2 h+Ferme Porte

Localisation : Coursive

Quantité : 01

Echelle : 1/20

PS

1

PS

Coupe A-A

1.04 h.c

7

90

7

Coupe B-B

2.20 h.c

7

2.13

Plan

1.04

7

90

7

30

30

1.22

13

15

soupirail en alu

Vitrage Transparent

Joint coupe feu Réf.TN/7 +Support inox

double vitrage 6+6 + film intermédiaire à haute densité de resistance

MENUISERIE BOIS

PS

2

PS

1.50 x 2.20 h.c

Porte coupe feu 1/2 h+Ferme Porte

Localisation : Coursive

Quantité : 03

Echelle : 1/20

PS

2

PS

Coupe A-A

1.50 h.c

7

68

68

7

Coupe B-B

2.20 h.c

7

2.13

Plan

1.50 h.c

7

68

68

7

30

30

1.22

13

15

soupirail en alu

Vitrage Transparent

Joint coupe feu Réf.TN/7 +Support inox

double vitrage 6+6 + film intermédiaire à haute densité de resistance

ECH:1/20

ECH:1/20

MENUISERIE BOIS

PS

1

PS

1.04 x 2.20 h.c

Porte coupe feu 1/2 h+Ferme Porte

Localisation : Coursive

Quantité : 01

Echelle : 1/20

Coupe A-A

1.04 h.c

7

90

7

Coupe B-B

2.20 h.c

7

2.13

1.22

30

30

13

15

soupirail en alu

Plan

1.04

7

90

7

Vitrage Transparent

double vitrage 6+6 + film intermédiaire à haute densité de résistance

Joint coupe feu Réf.TN/7 +Support inox

MENUISERIE BOIS

PS

2

PS

1.50 x 2.20 h.c

Porte coupe feu 1/2 h+Ferme Porte

Localisation : Coursive

Quantité : 03

Echelle : 1/20

Coupe A-A

1.50 h.c

7

68

68

7

Coupe B-B

2.20 h.c

7

2.13

1.22

30

30

13

15

soupirail en alu

Plan

1.50

7

68

68


Vitrage Transparent


double vitrage 6+6 + film intermédiaire à haute densité de résistance

Joint coupe feu Réf.TN/7 +Support inox

ECH:1/20

ECH:1/20

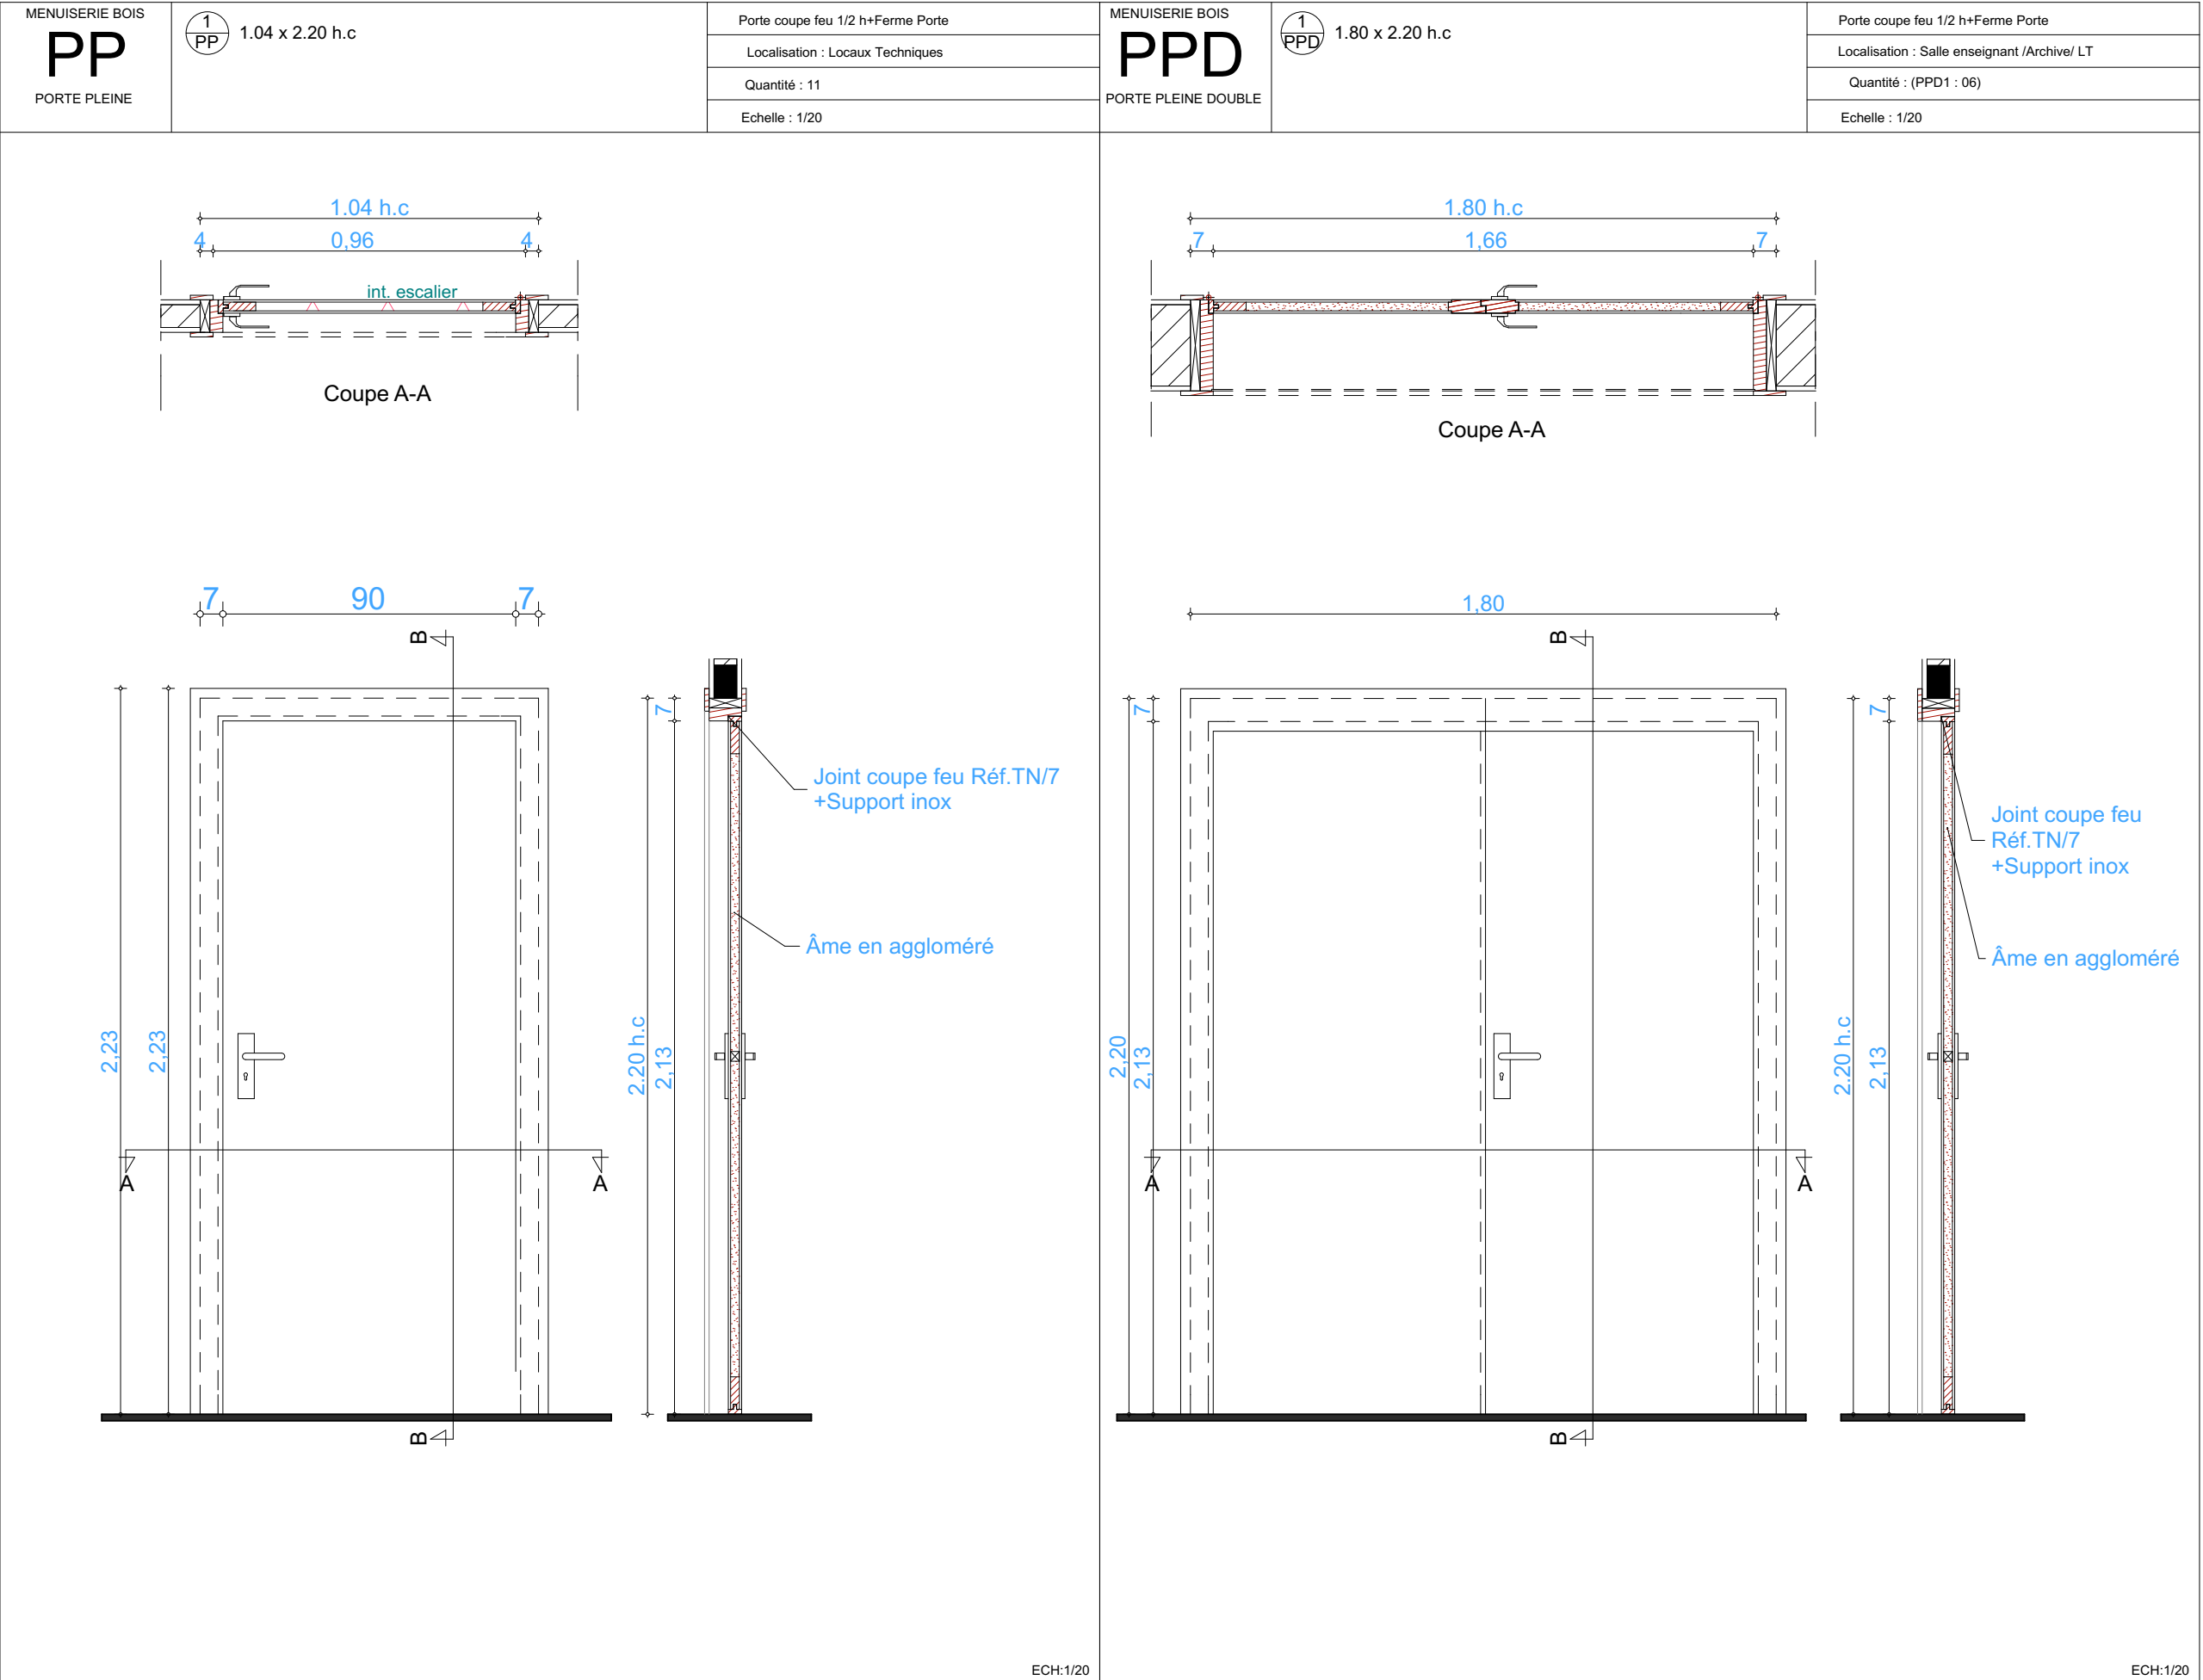

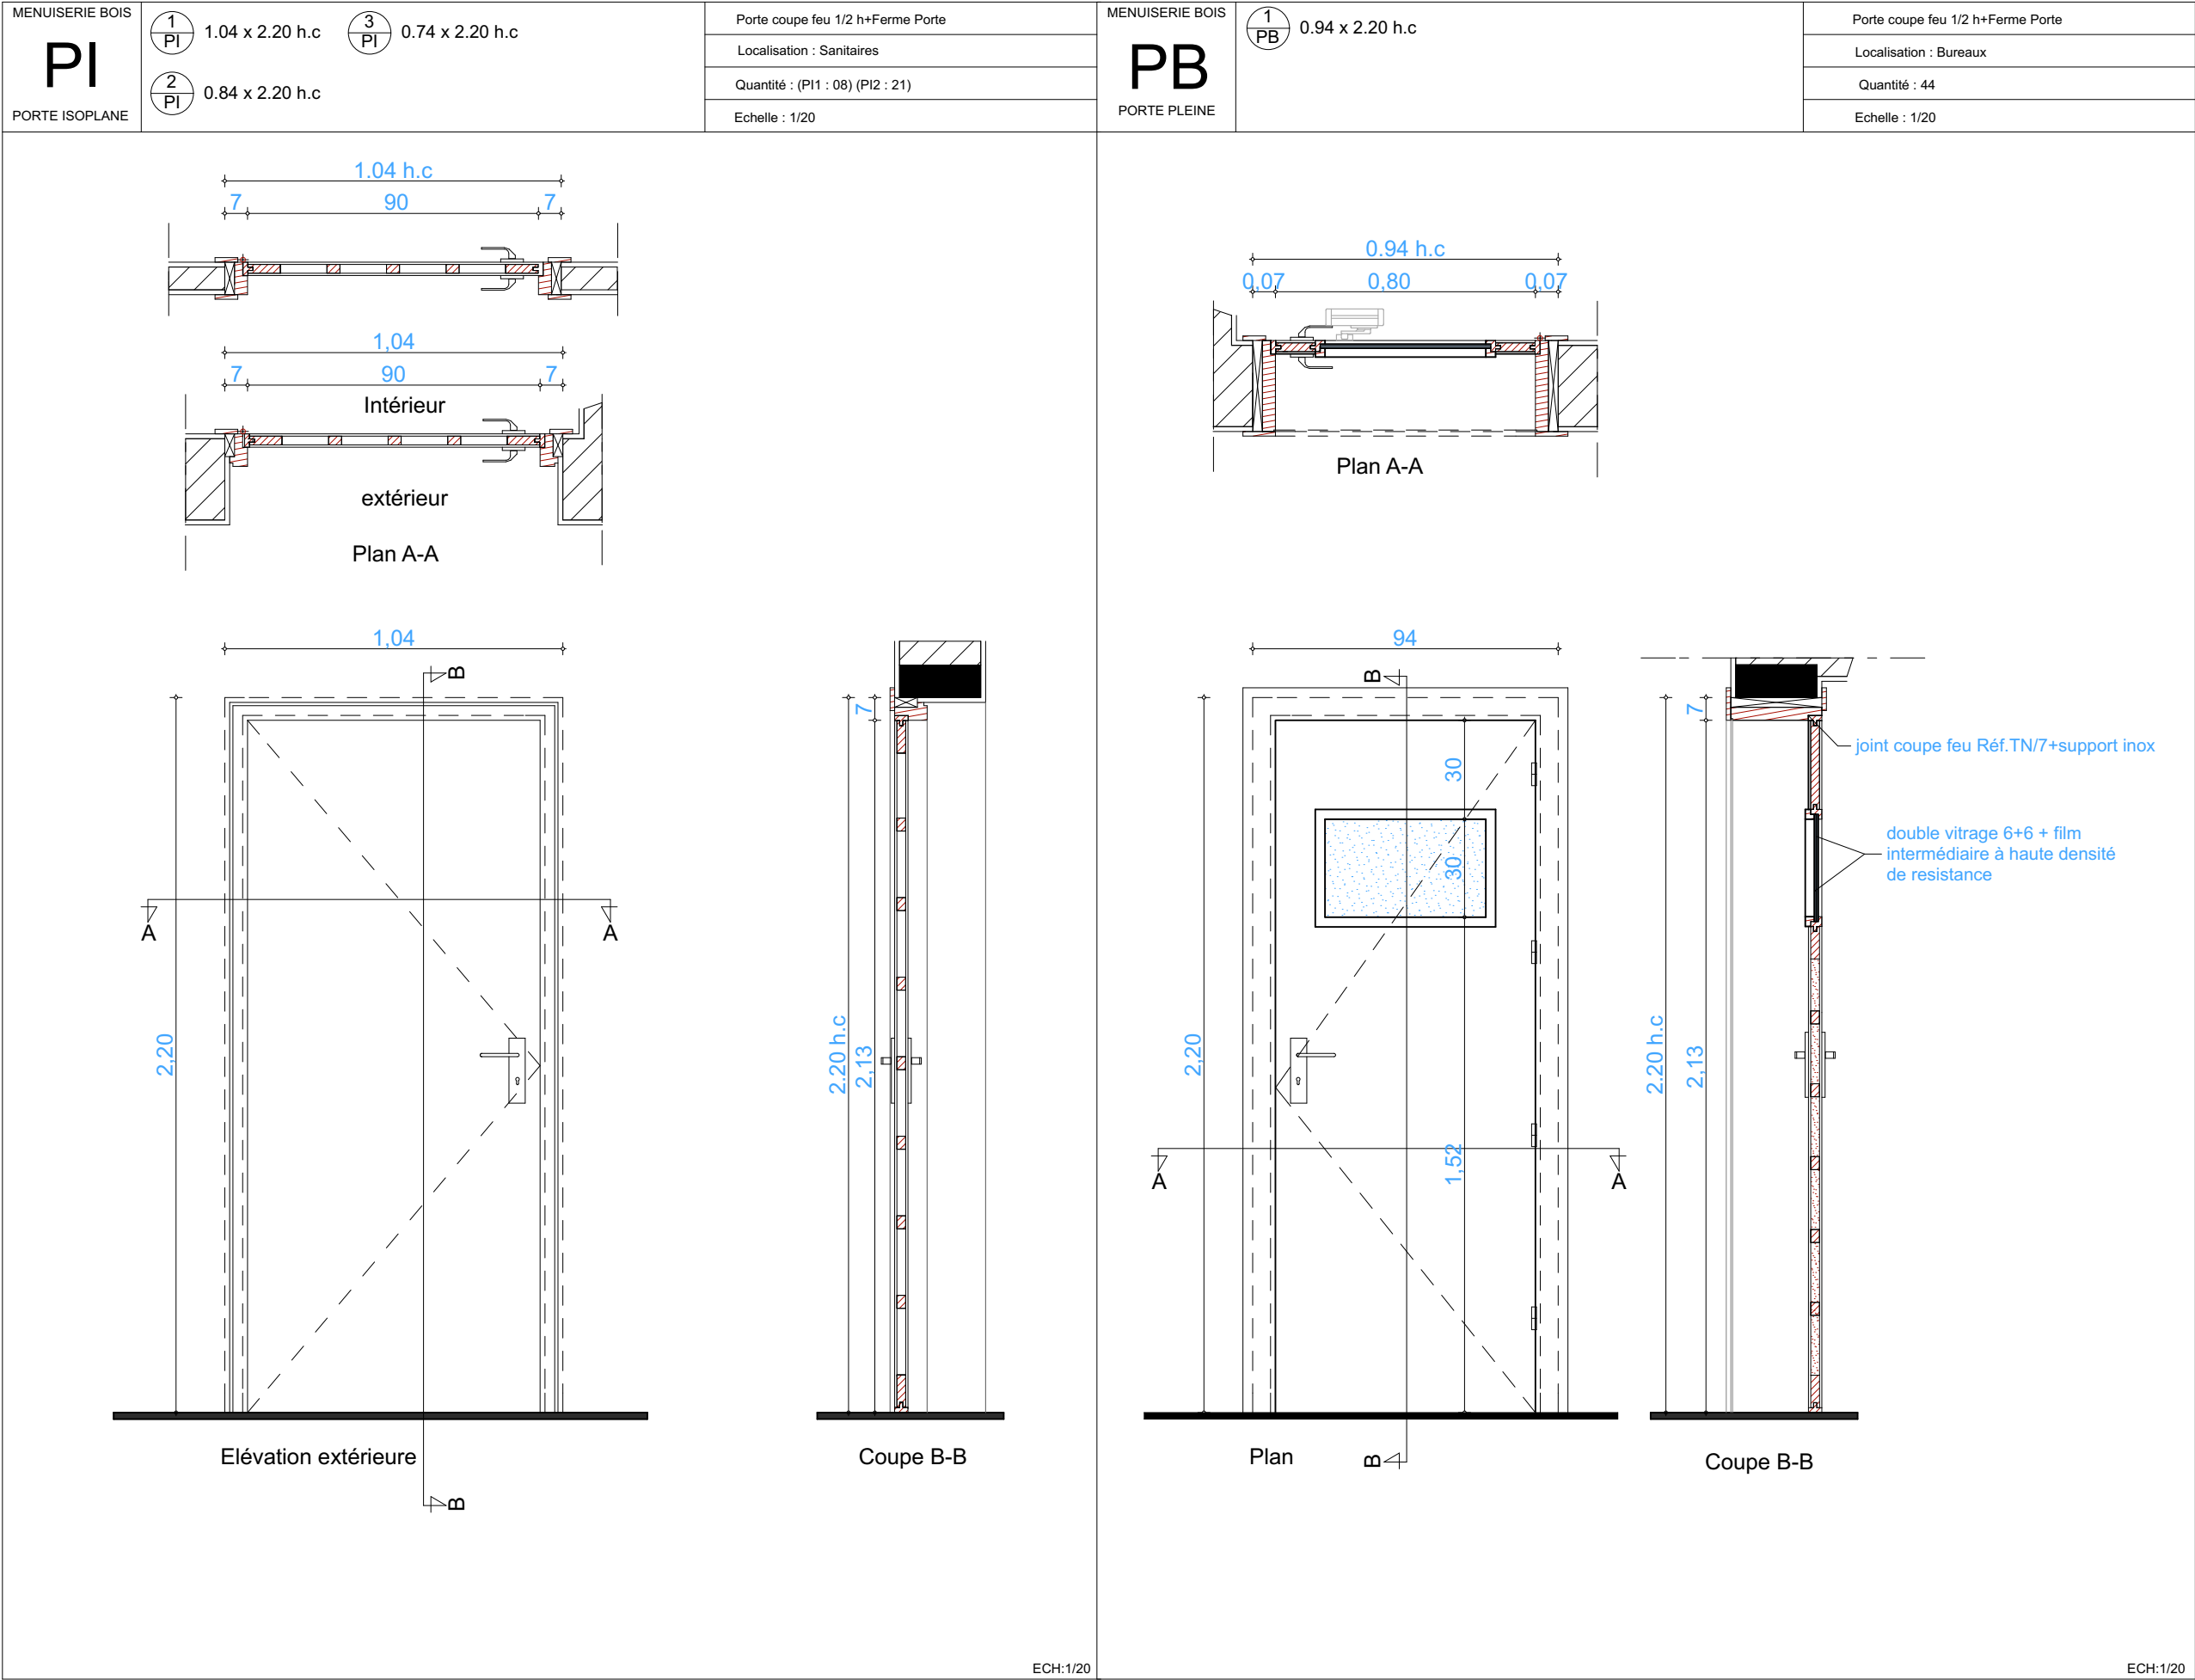

MENUISERIE BOIS

PL

1
PL

1.50 x 2.20 h.c

Porte coupe feu 1/2 h+Ferme Porte

Localisation : Salle de Réunion / Bureau Directeur

Quantité : 05

Echelle : 1/20

Porte coupe feu 1/2 h+Ferme Porte

Localisation : Bureau directeur

Quantité : 01

Echelle : 1/20

Coupe A-A

1.50 h.c

7 68 68 7

Vitrage Transparent

Plan

2.20 h.c

2.13

7

A

A

Coupe B-B

2.20 h.c

2.13

7

Joint coupe feu Réf.TN/7
+Support inox

double vitrage 6+6 + film
intermédiaire à haute
densité de resistance

Coupe A-A

1.24 h.c

7 1.06 7

Vitrage Transparent

Plan

2.20 h.c

2.13

7

A

A

Coupe B-B

2.20 h.c

2.13


3 7

Joint coupe feu Réf.TN/7
+Support inox

double vitrage 6+6 + film
intermédiaire à haute
densité de resistance

ECH:1/20

ECH:1/20

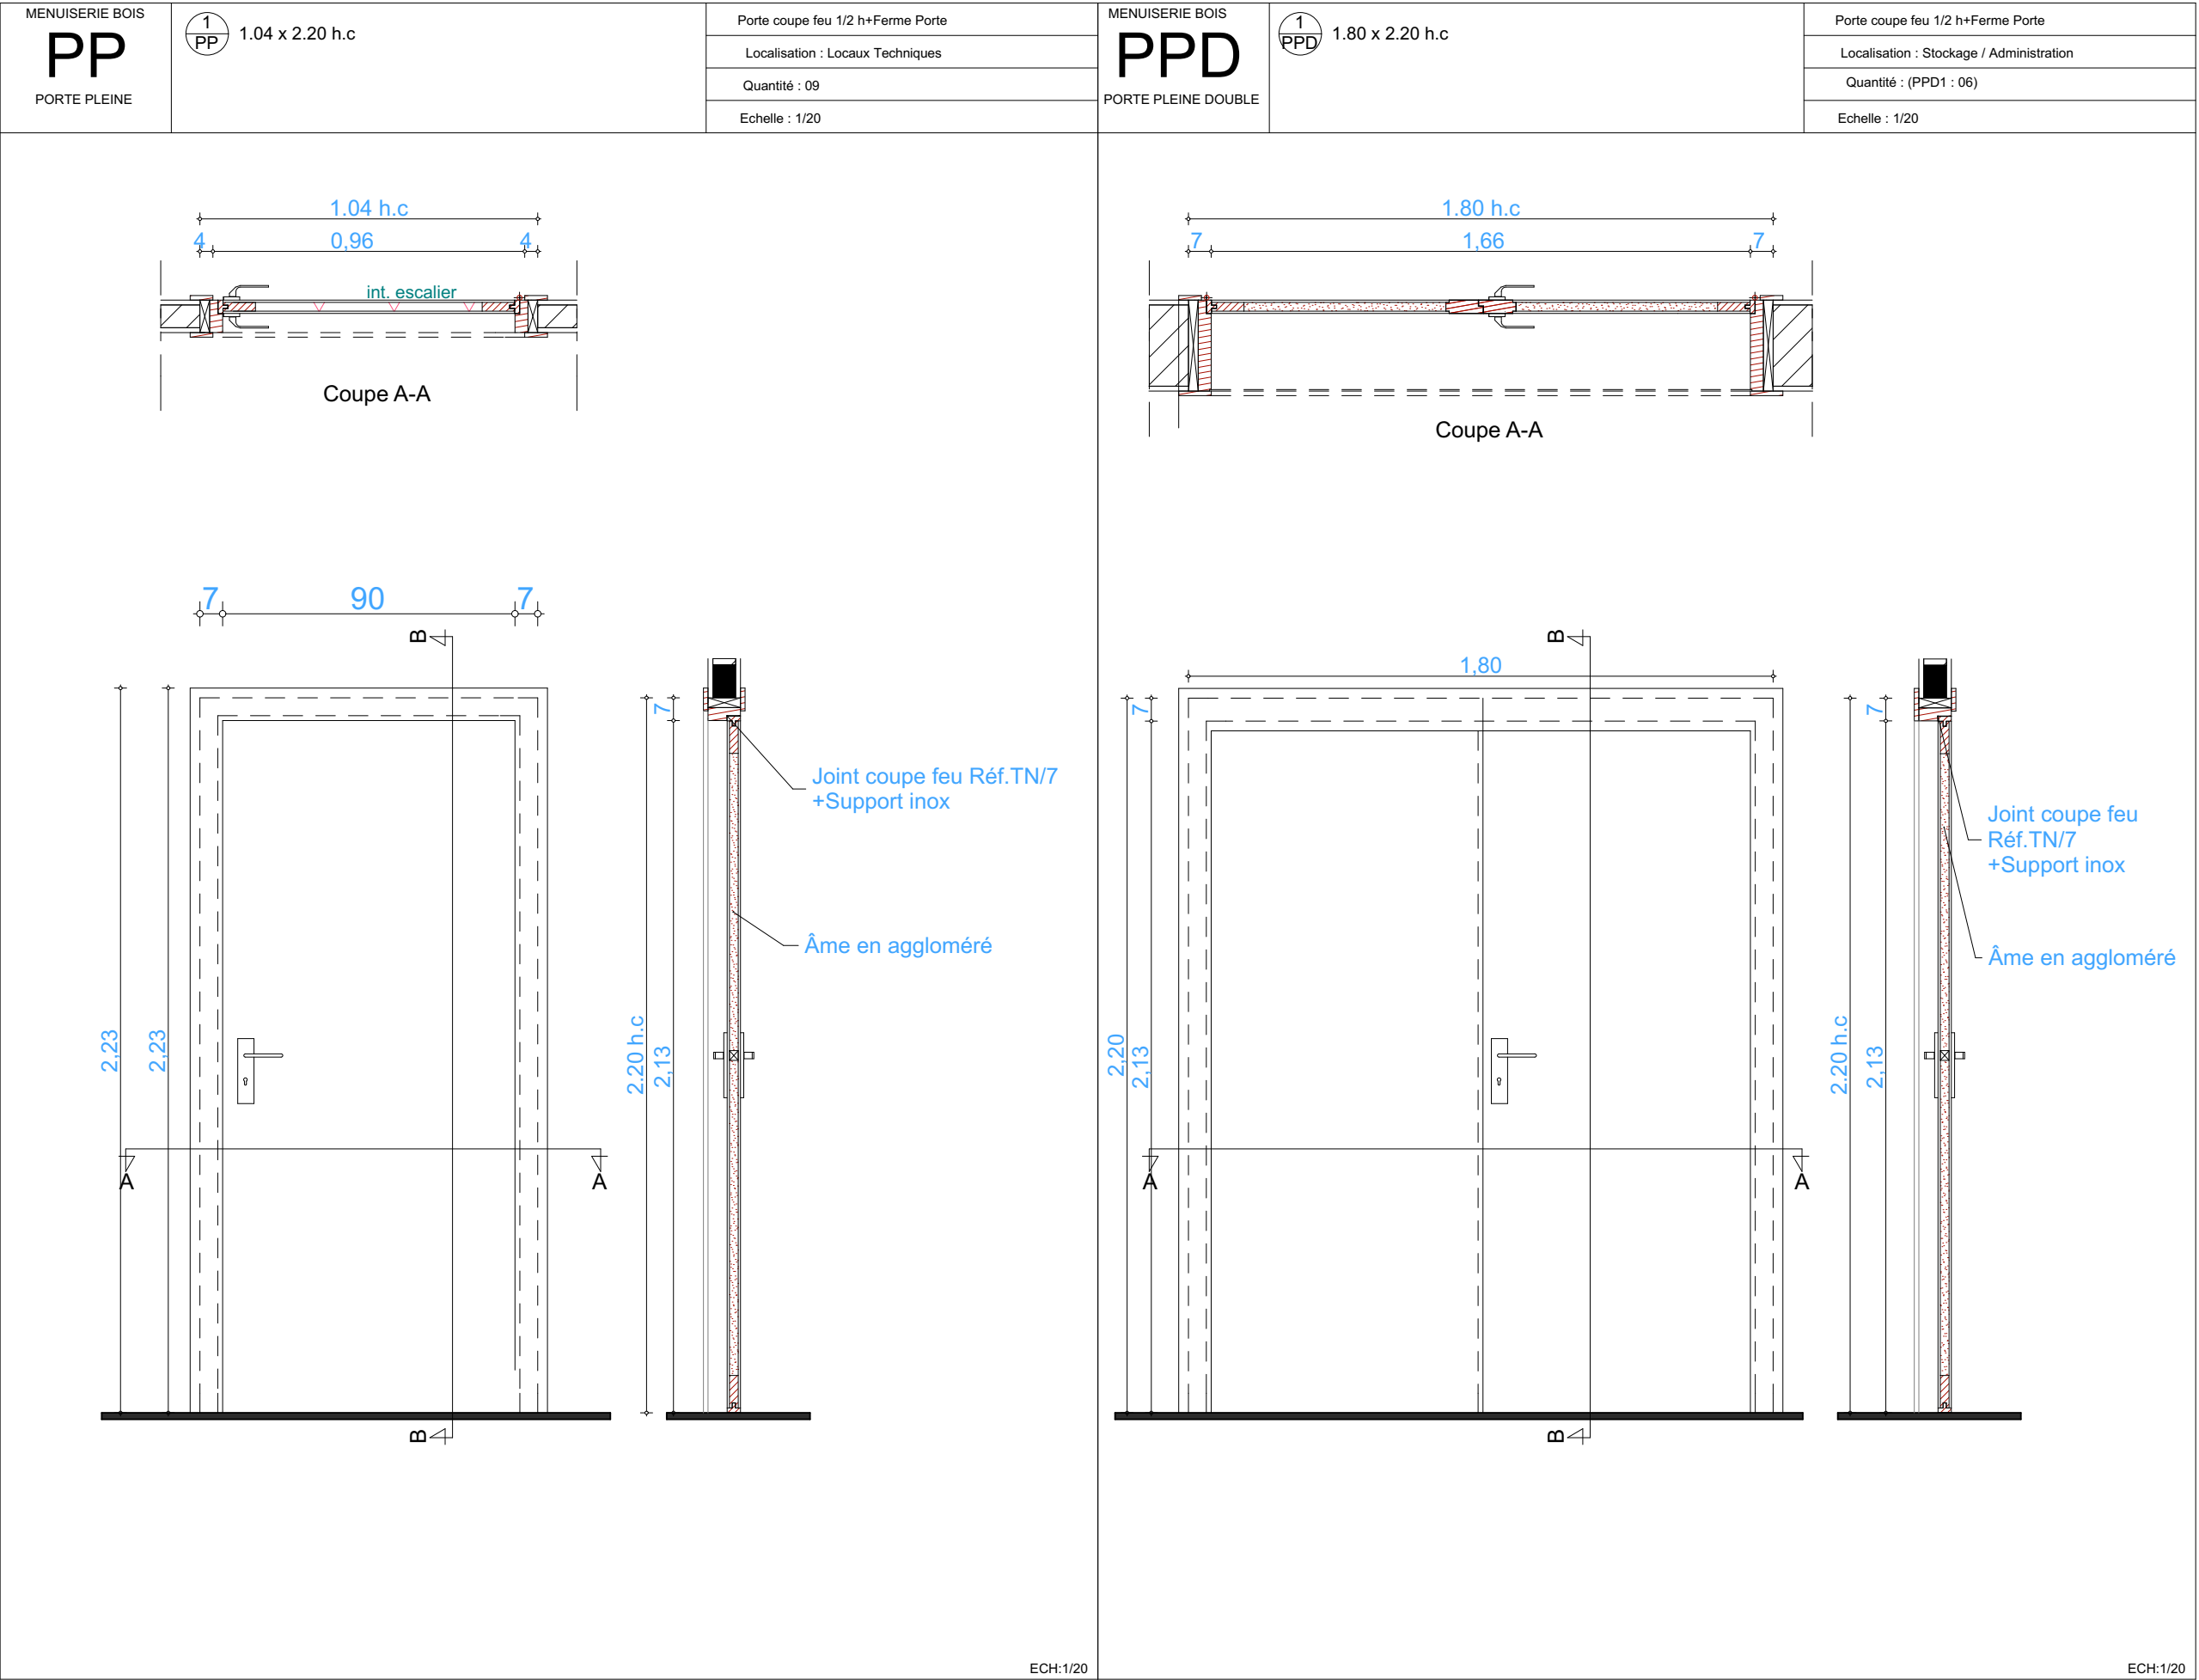

MENUISERIE BOIS

PS

1

PS

1.04 x 2.20 h.c

Porte coupe feu 1/2 h+Ferme Porte

Localisation : Coursive

Quantité : 01

Echelle : 1/20


Coupe A-A

1.04 h.c

7

90

7

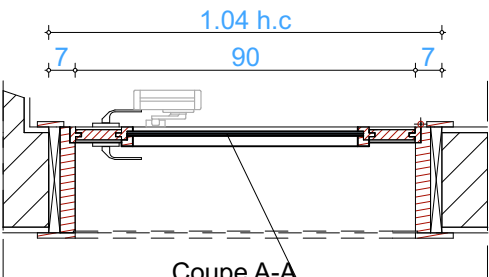

Plan

2.20

2.13

7

1.04

7

90

7


1.22

30

30

13

15

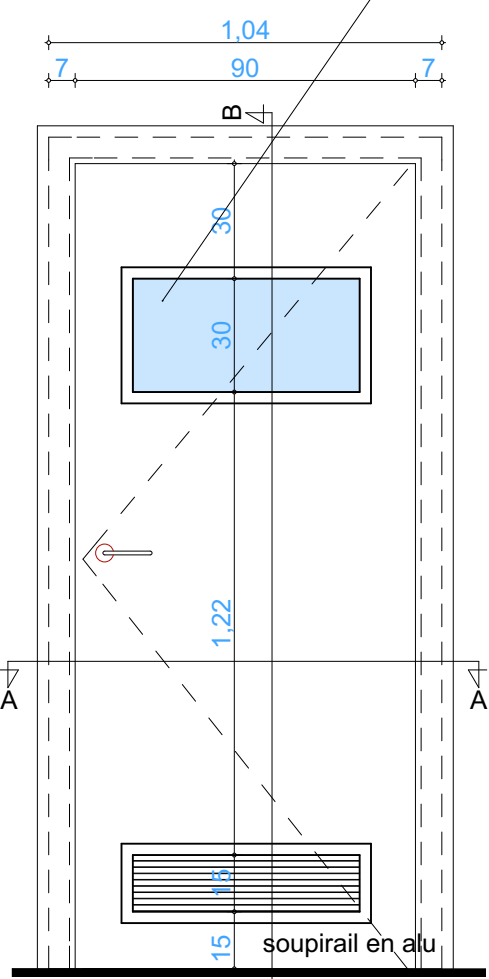

Coupe B-B


2.20 h.c

2.13

7

Joint coupe feu Réf.TN/7 +Support inox

double vitrage 6+6 + film intermédiaire à haute densité de resistance

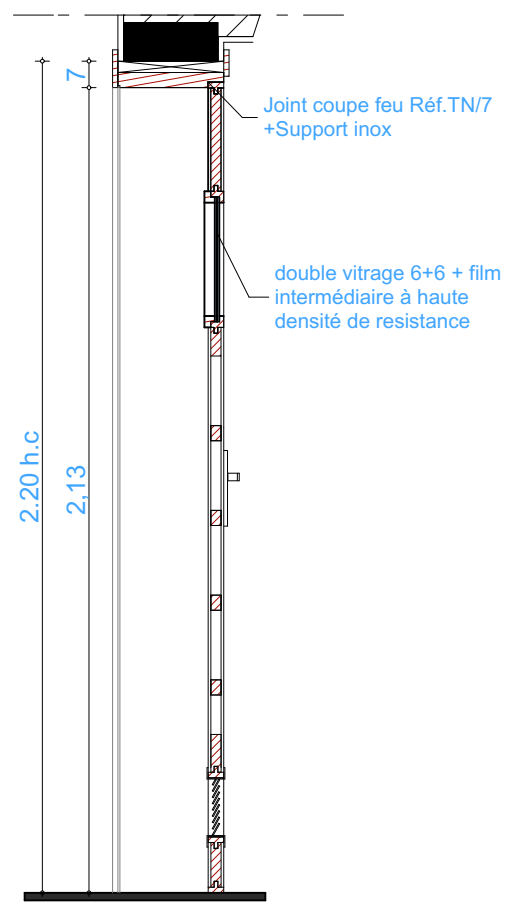

MENUISERIE BOIS

PS

2

PS

1.50 x 2.20 h.c

Porte coupe feu 1/2 h+Ferme Porte

Localisation : Coursive

Quantité : 03

Echelle : 1/20

Coupe A-A


1.50 h.c

7

68

68

7

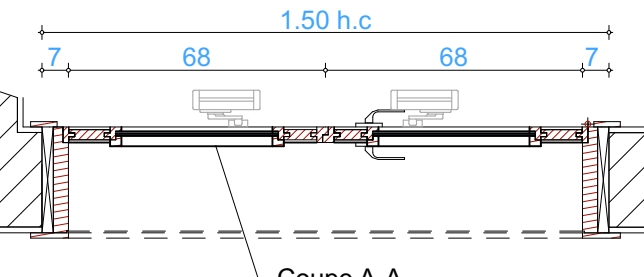

Plan

2.20 h.c

2.13

7

1.50

7

68

68

7


1.22

30

30

13

15

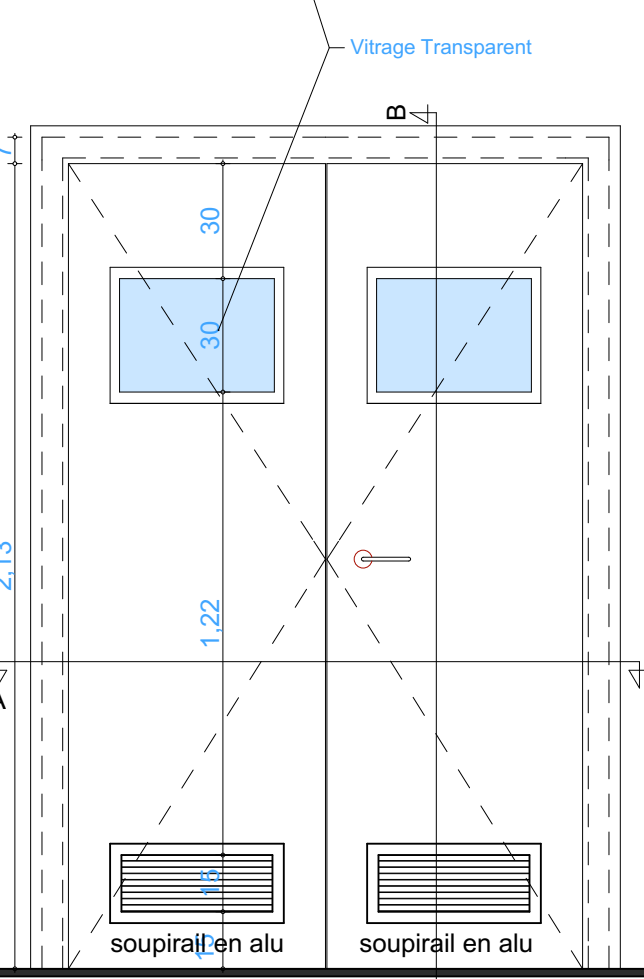

Coupe B-B


2.20 h.c

2.13

7

Joint coupe feu Réf.TN/7 +Support inox

double vitrage 6+6 + film intermédiaire à haute densité de resistance

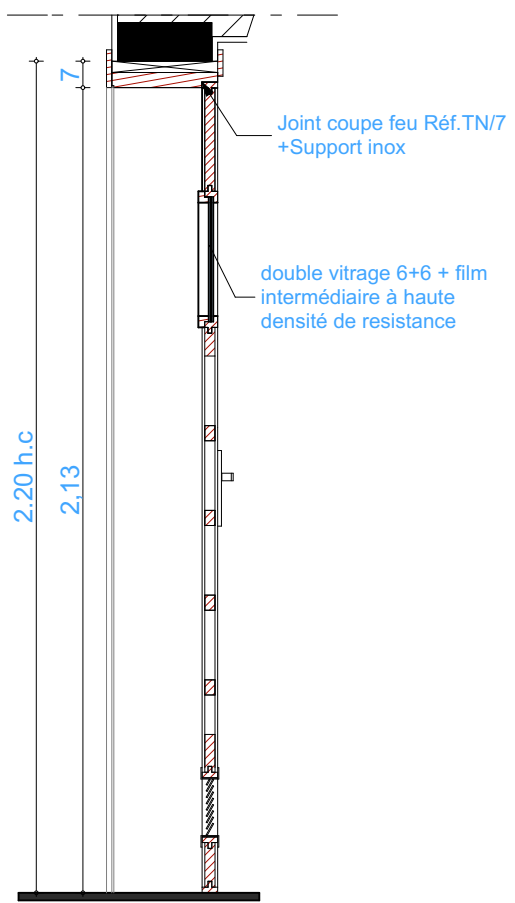

ECH: 1/20

ECH: 1/20

MENUISERIE BOIS		Porte coupe feu 1/2 h+Ferme Porte	MENUISERIE BOIS		Porte coupe feu 1/2 h+Ferme Porte
PS	1 PS	Localisation : Coursive	PS	2 PS	Localisation : Coursive
1.04 x 2.20 h.c		Quantité : 01	1.50 x 2.20 h.c		Quantité : 03
PORTE DE SECOURS		Echelle : 1/20	PORTE DE SECOURS		Echelle : 1/20


The figure displays technical specifications and cross-sections for two types of fire-rated doors (Coupe A-A and Coupe B-B) and their plans.

Model 1: 1.04 x 2.20 h.c


- Coupe A-A:** Shows the door's profile with dimensions: total width 1.04 m, opening width 90 cm, and side clearances of 7 cm each. The height is 2.20 m.
- Coupe B-B:** Shows the vertical section with dimensions: total height 2.20 m, opening height 2.13 m, and top/bottom clearances of 7 cm each. It labels the "Joint coupe feu Réf.TN/7 +Support inox" and "double vitrage 6+6 + film intermédiaire à haute densité de résistance".
- Plan:** Shows the door's footprint with dimensions: total width 1.04 m, opening width 90 cm, and side clearances of 7 cm each. The height is 2.20 m. It indicates the "Vitrage Transparent" area (30 cm wide) and the "soudrail en alu" (aluminum extrusion).

Model 2: 1.50 x 2.20 h.c


- Coupe A-A:** Shows the door's profile with dimensions: total width 1.50 m, opening width 1.30 m, and side clearances of 7 cm each. The height is 2.20 m.
- Coupe B-B:** Shows the vertical section with dimensions: total height 2.20 m, opening height 2.13 m, and top/bottom clearances of 7 cm each. It labels the "Joint coupe feu Réf.TN/7 +Support inox" and "double vitrage 6+6 + film intermédiaire à haute densité de résistance".
- Plan:** Shows the door's footprint with dimensions: total width 1.50 m, opening width 1.30 m, and side clearances of 7 cm each. The height is 2.20 m. It indicates the "Vitrage Transparent" area (30 cm wide) and the "soudrail en alu" (aluminum extrusion).

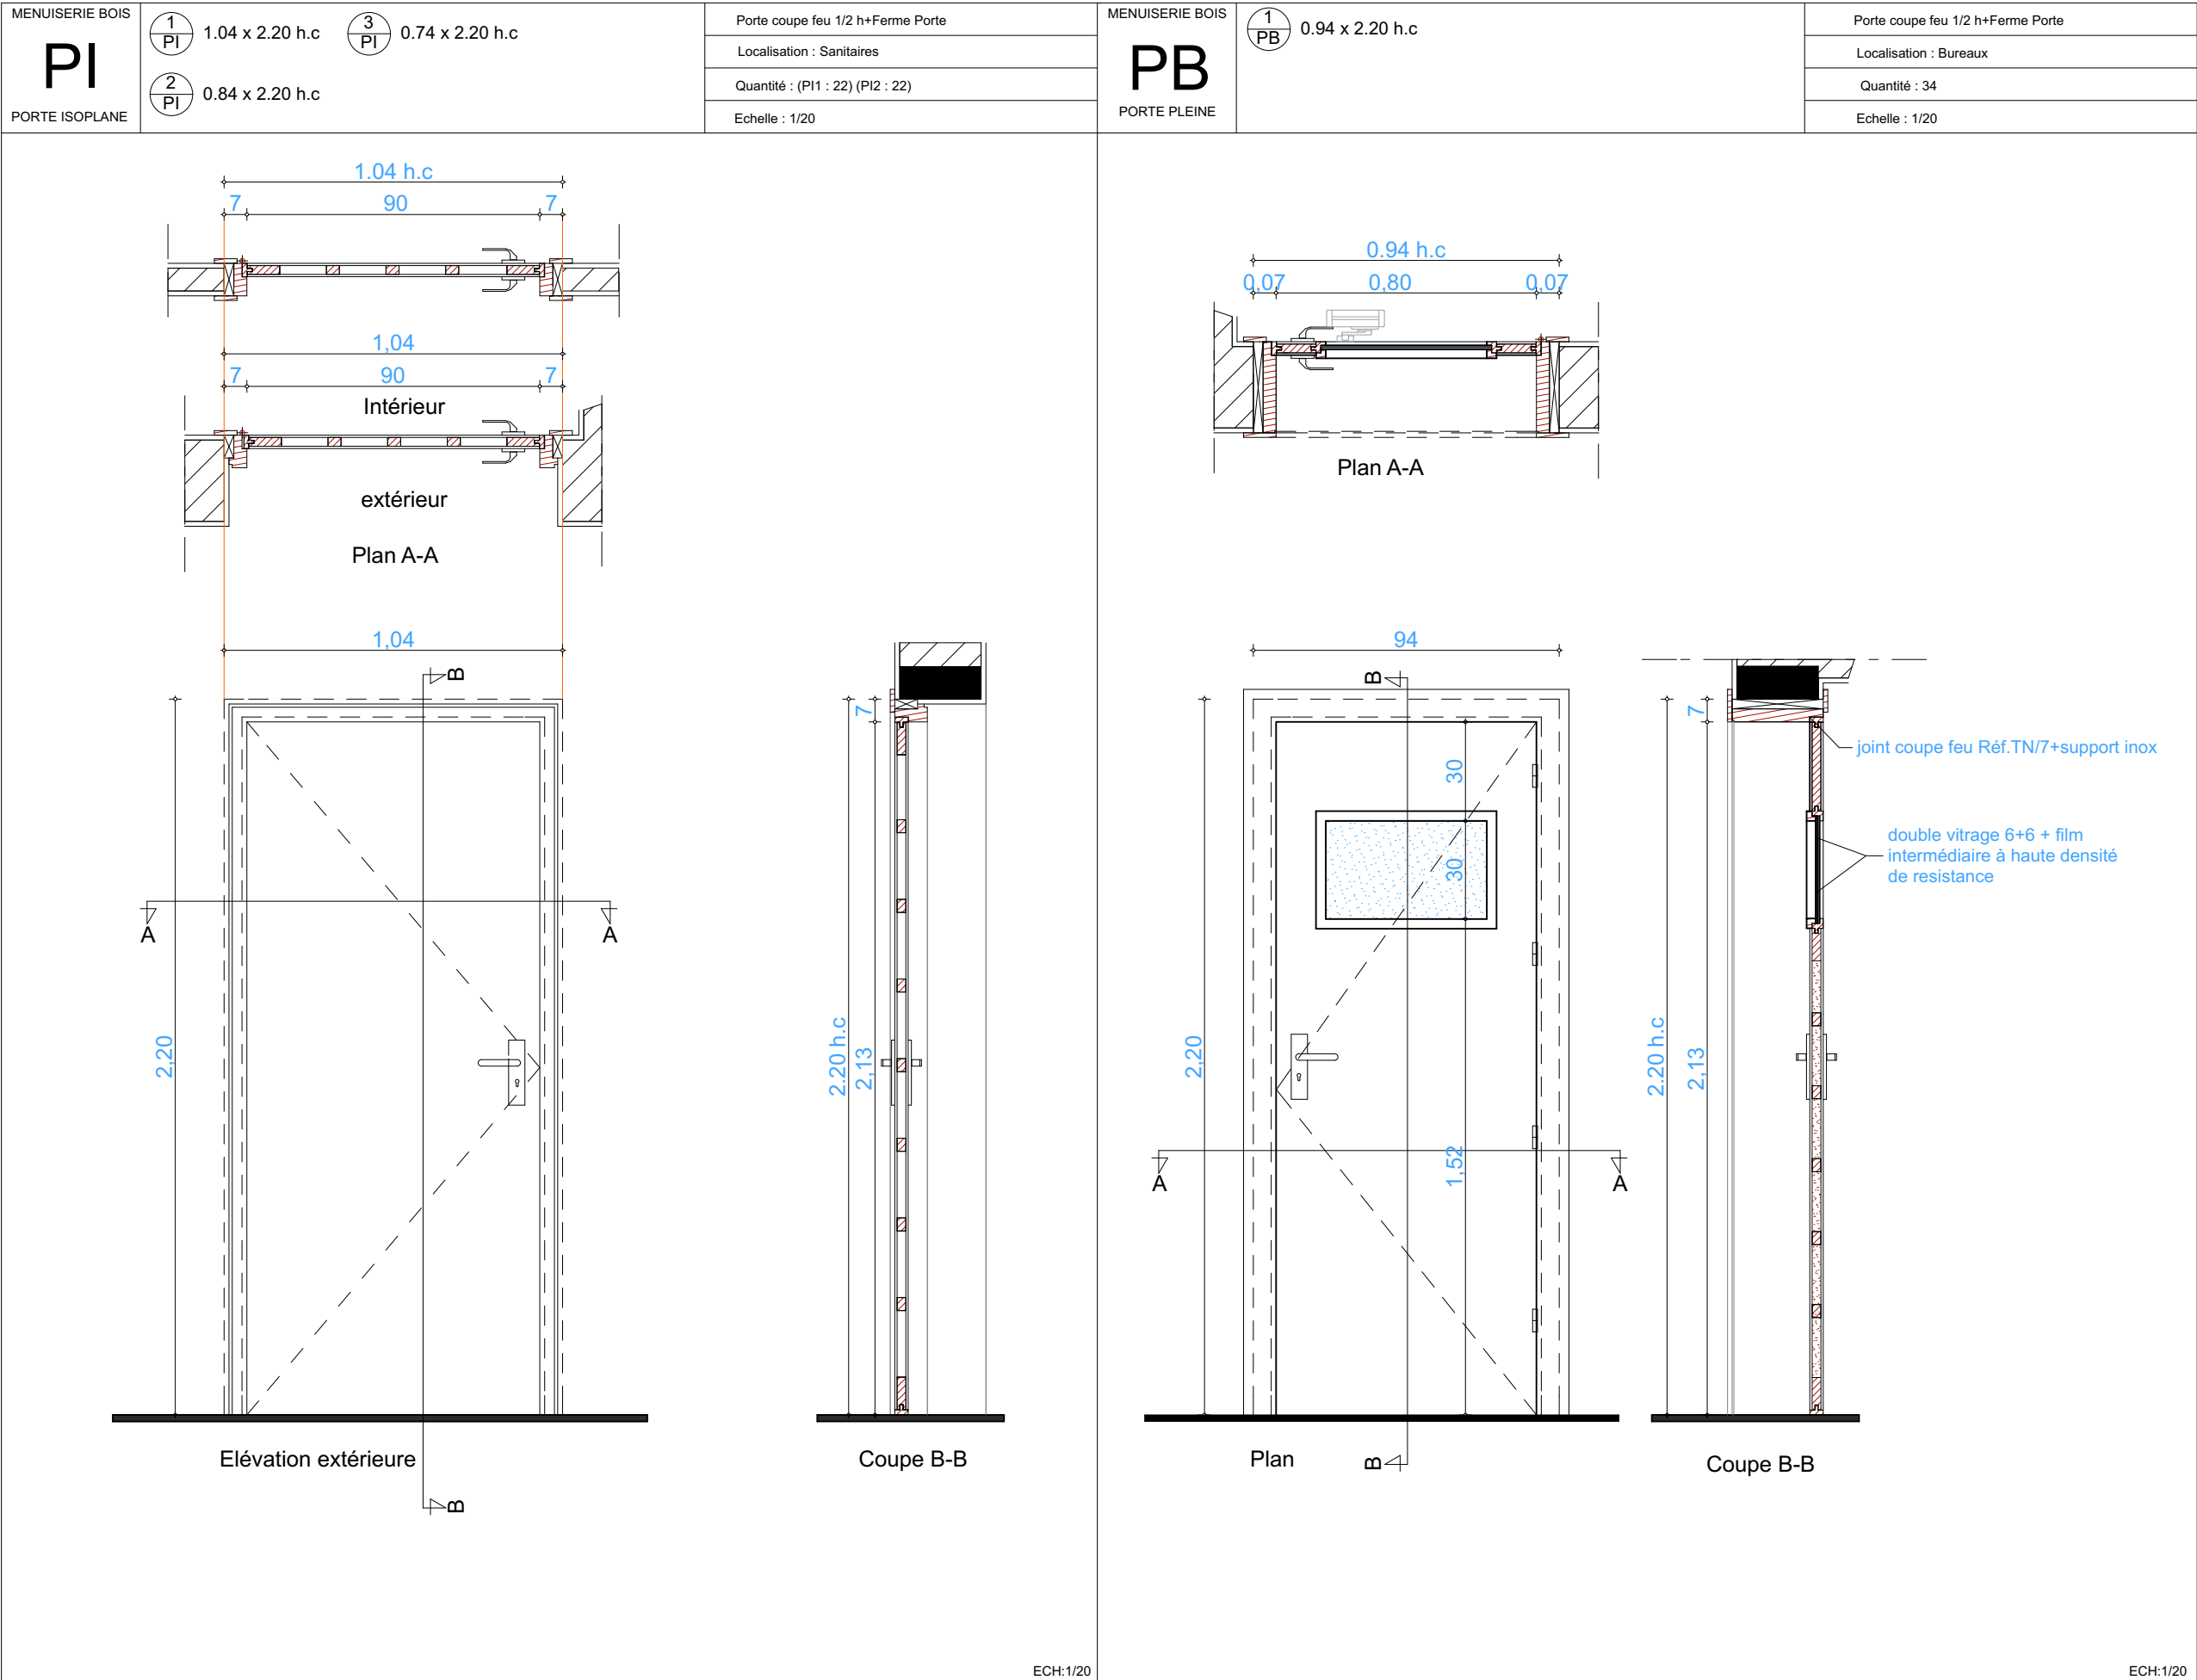


	PB2	Spécifications Bois PROJET DE CONSTRUCTION DE L'ENSEMBLE ARTISANAL DE LA VILLE D'OULMES	Date : 04/08/2016		FAV5-FAV6 FAV7-FAV8 FAV9-FAV10	Spécification Aluminium PROJET DE CONSTRUCTION DE L'ENSEMBLE ARTISANAL DE LA VILLE D'OULMES	Date : 04/08/2016
			Echelle : 1/20				Echelle : 1/20
			S.sol: ☐ RDC: ☒ Etage: ☒ Terrasse ☐				S.sol: ☐ RDC: ☒ Etage: ☒ Terrasse ☐
			Faux Cadre: 70x30 mm				Faux Cadre:
Porte type : PB3 = 84x220 hc - PB3 BIS = 84x180 hc - PB4 = 74x220 hc - idem au type PB2=3			Cadre : 100x55 mm	Fenêtre type : FAV5 - FAV6 - FAV7 - FAV8 - FAV9			Cadre :
Dimensions: 104 x220 hc			Chambranle: 100x20 mm	Dimensions: voir type ci dessous			Chambranle :
Type d'ouvrant : 1 vantail ouvrant à la française			Quantité: 19	Type d'ouvrant : coulissant - ouvrant à la française - fixe			Quantité: FAV5=17-FAV6=1-FAV7=14-FAV8=2 -FAV9=4-FAV10=4
Panneau d'ouvrant : isoplane sur 2 faces			Localisation : ensemble artisanal RDC: stockage PB2=1- sanitaires PB3=2-PB4=4-cafétiériat : PB3=4-PB4=2 débarras sous escalier administration PB3 BIS = 1 Etage Administration : sanitaires PB3=1-PB4=2-PB2=2	Panneau d'ouvrant : coulissant			Localisation:ensemble artisanal RDC: FAV5=4-FAV6=1-FAV9=4 RDC Administration : FAV5=6 Etage Administration : FAV5=7 RDC Administration : FAV7=7 Etage Administration : FAV7=7 Etage Administration : FAV8=2 - FAV10 = 4
Quincaillerie :				Quincaillerie :			

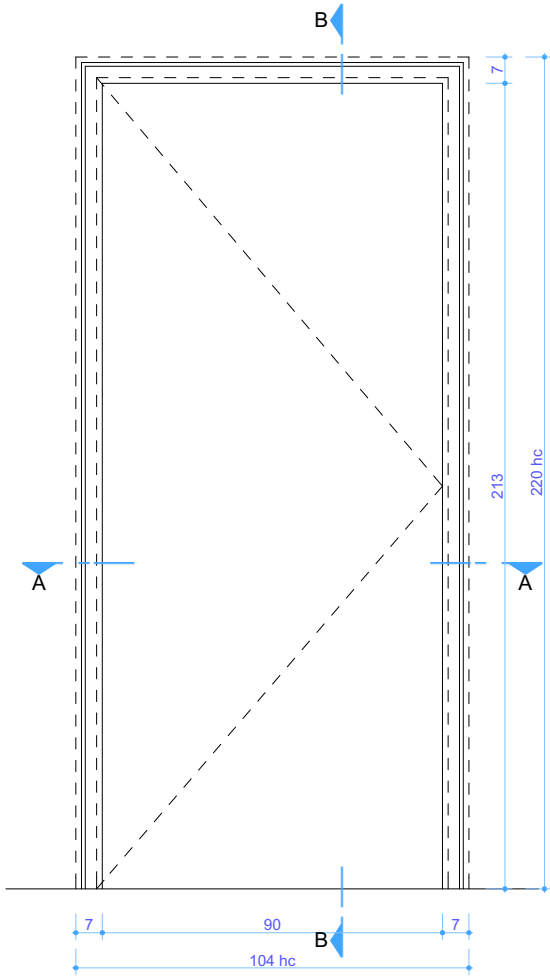

Vue Externe

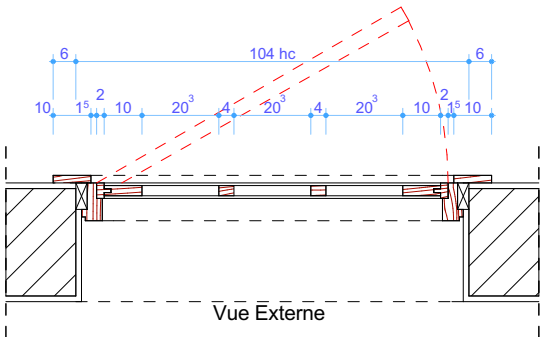


Coupe A-A

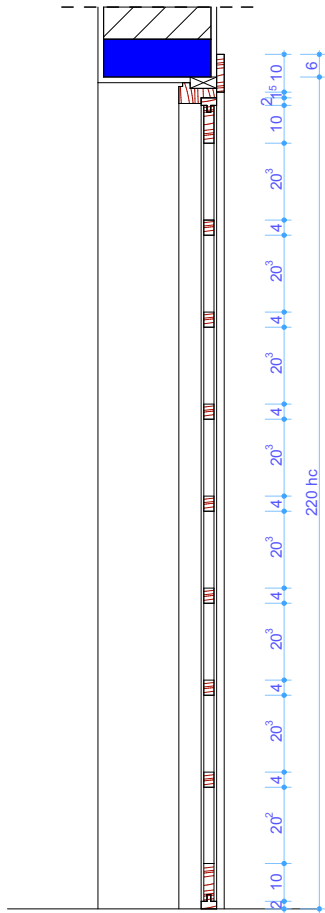


Coupe B-B


FAV5

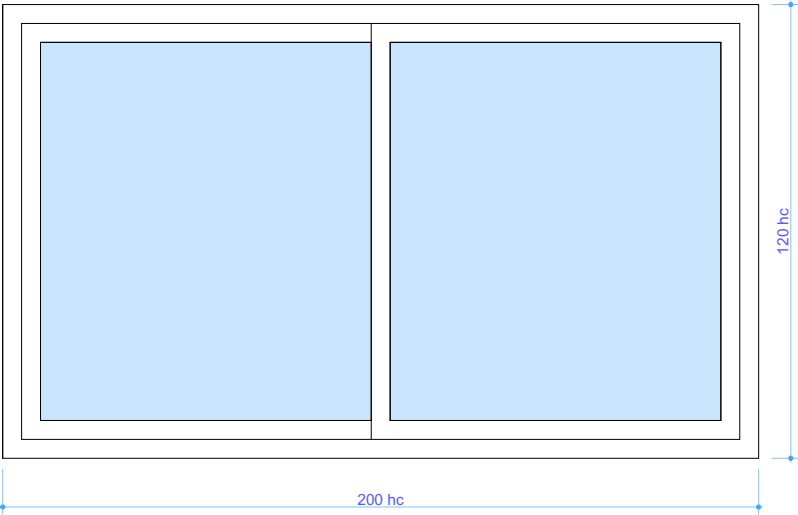


FAV6

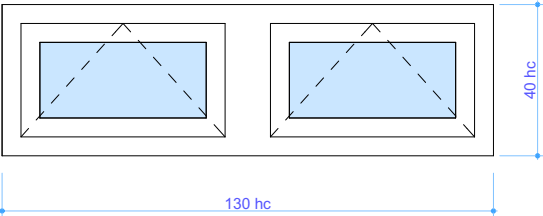


FAV7

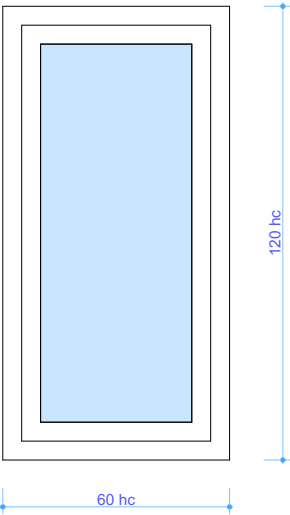


FAV8

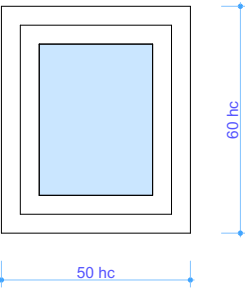

FAV9

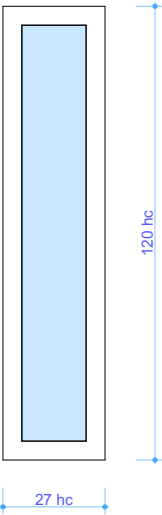


FAV10

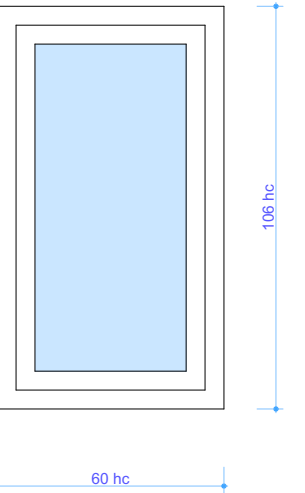


PAV1-PAV2 -ENSAV1	Spécification Aluminium PROJET DE CONSTRUCTION DE L'ENSEMBLE ARTISANAL DE LA VILLE D'OULMES	Date : 04/08/2016
		Echelle : 1/20
		S.sol: ☐ RDC: ☒ Etage: ☒ Terrasse ☐
		Faux Cadre:
Porte type : PAV1 200x220 hc - PAV2 160x220 hc - ENSAV1 500x220 hc		Cadre :
Dimensions: voir type ci dessous		Chambranle:
Type d'ouvrant : 2 vantaux ouvrant à la française		Quantité: PAV1 = 5 - PAV2 = 5 - ENSAV1 = 1
Panneau d'ouvrant :		Localisation : PAV2=2: accès RDC administration accès cafétéria=1- ensemble artisanal=1 PVA2: RDC ensemble artisanal ENSAV1: Etage administration
Quincaillerie :		


PAV1

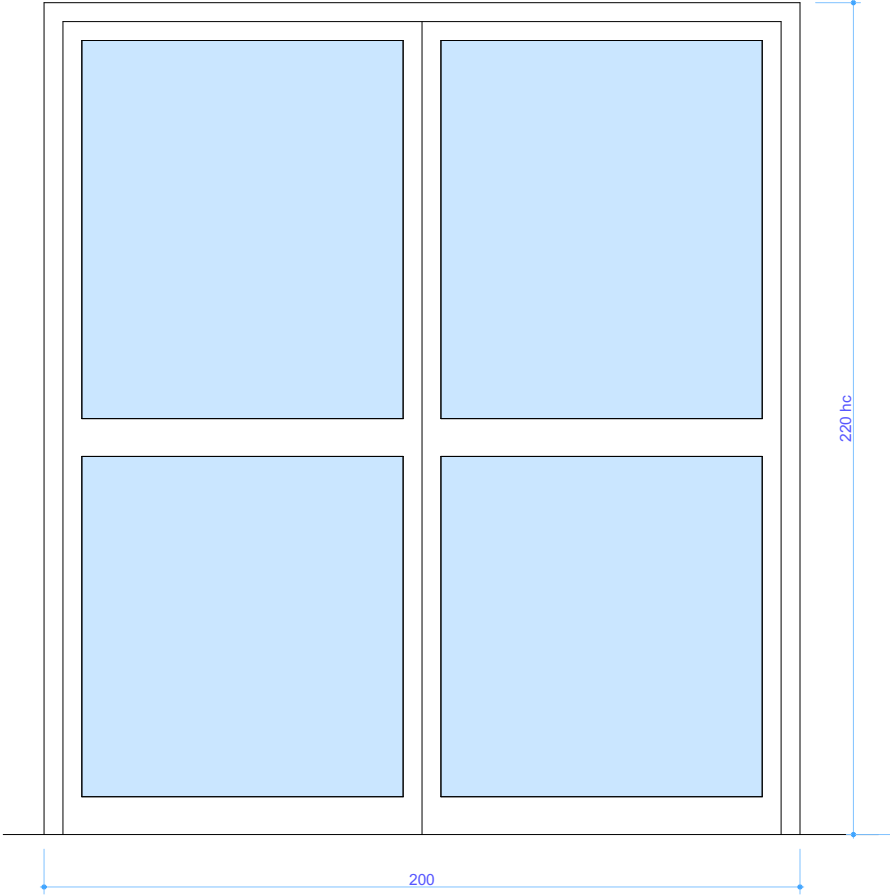

ENSAV1

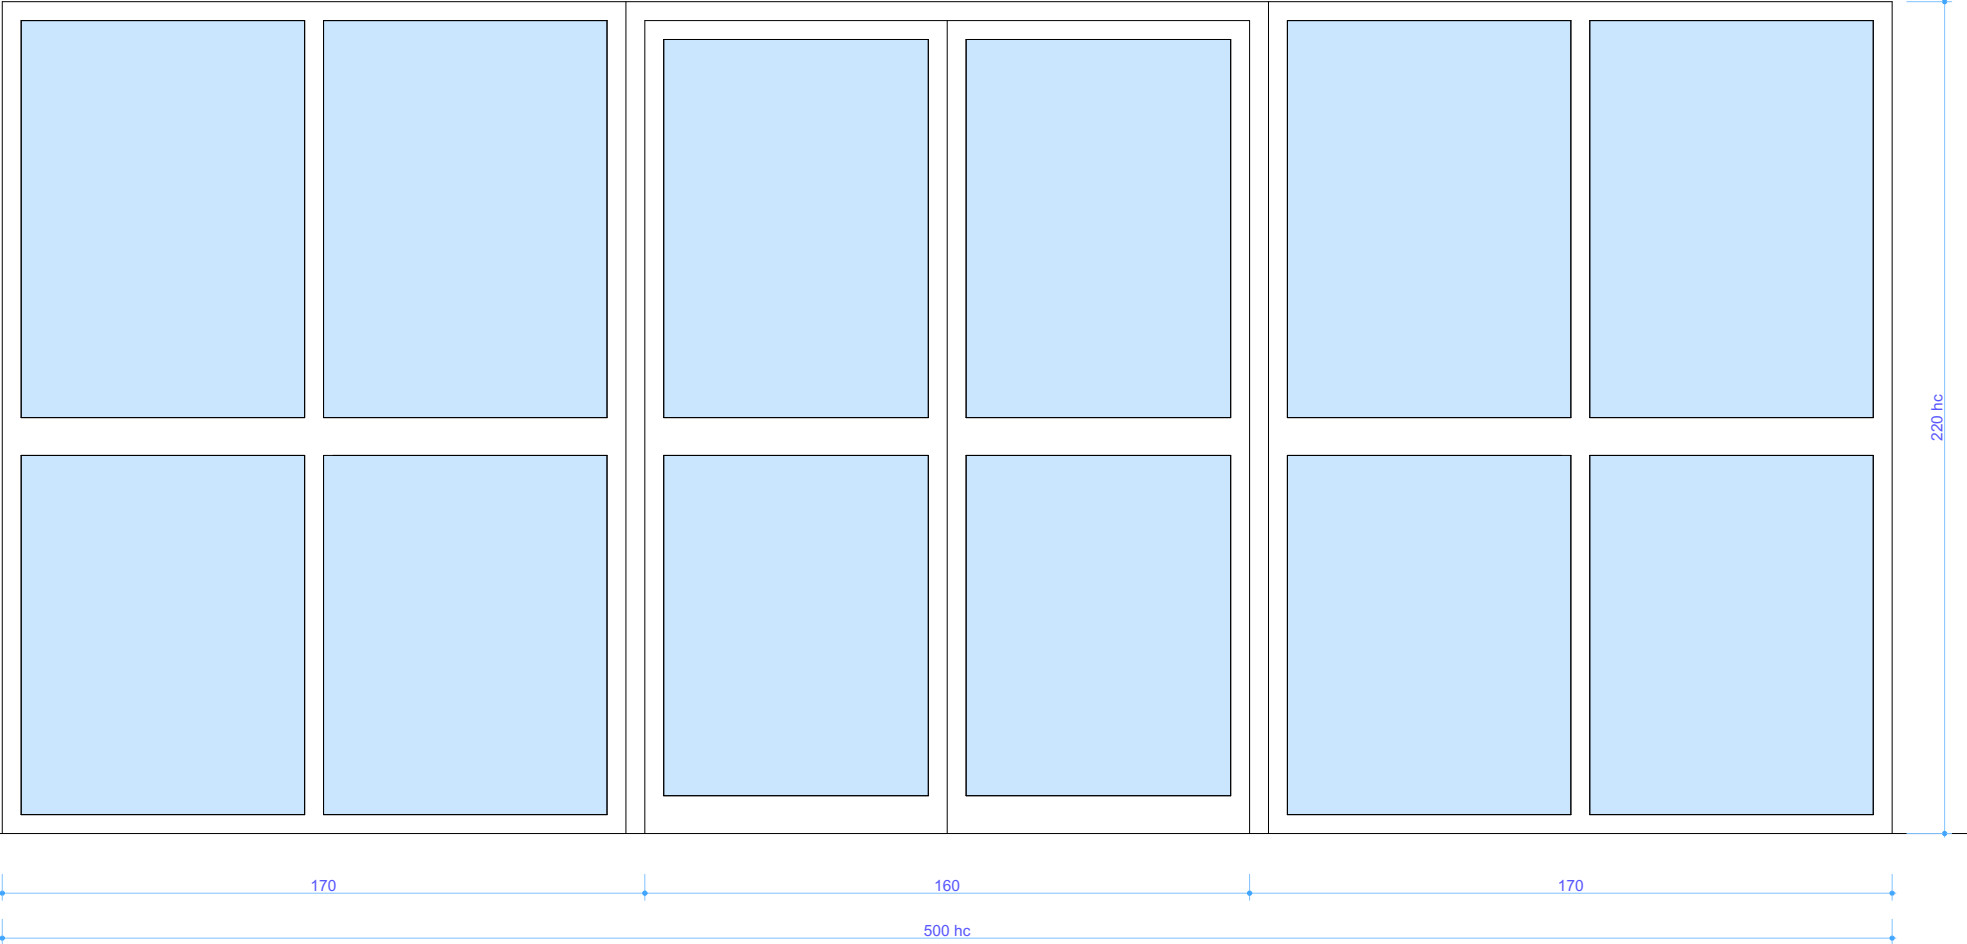


PAV2

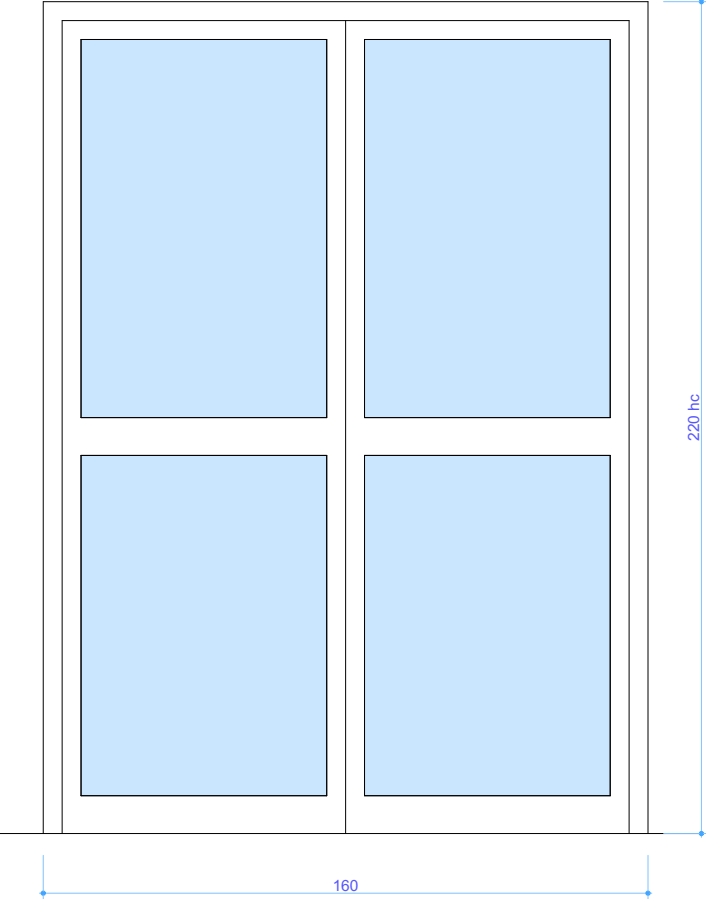


	FAV1-FAV2 FAV3-FAV4	Spécification Aluminium PROJET DE CONSTRUCTION DE L'ENSEMBLE ARTISANAL DE LA VILLE D'OULMES	Date : 04/08/2016
			Echelle : 1/20
			S.sol: ☐ RDC: ☒ Etage: ☐ Terrasse ☐
			Faux Cadre:
Fenêtre type : FAV1 - FAV2 - FAV3 - FAV4			Cadre :
Dimensions: voir type ci dessous			Chambranle:
Type d'ouvrant : coulissant			Quantité: FAV1=2 - FAV2=2 - FAV3=1- FAV4=1
Panneau d'ouvrant : coulissant			Localisation : RDC ensemble artisanal
Quincaillerie :			


FAV1

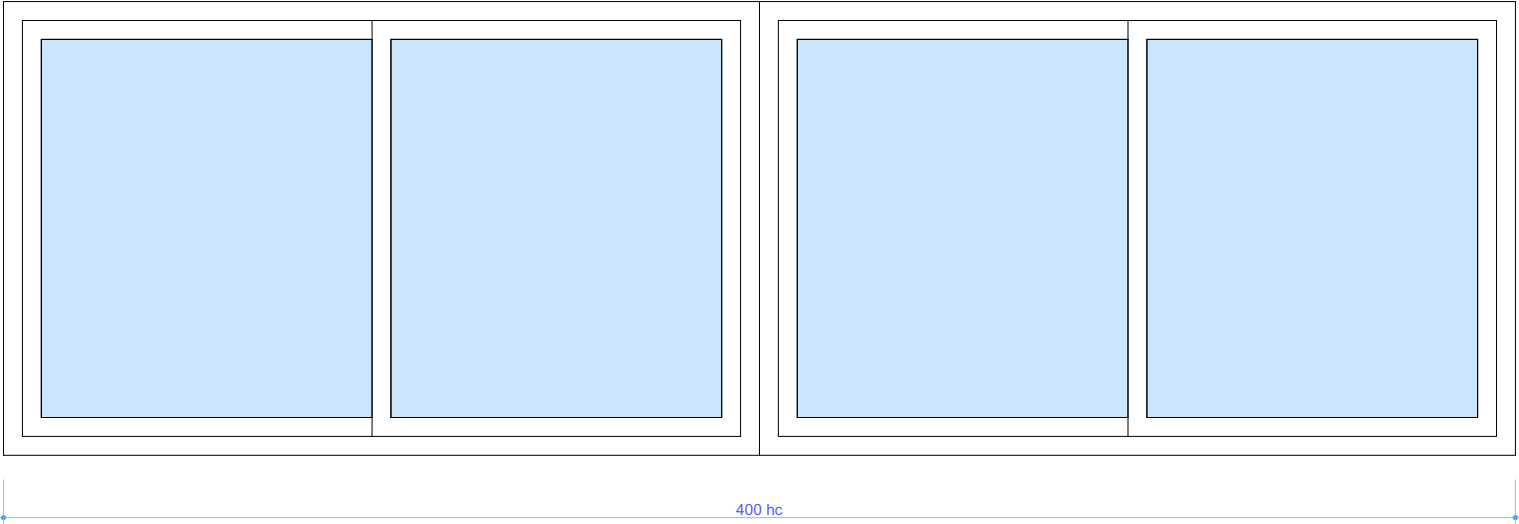


FAV2

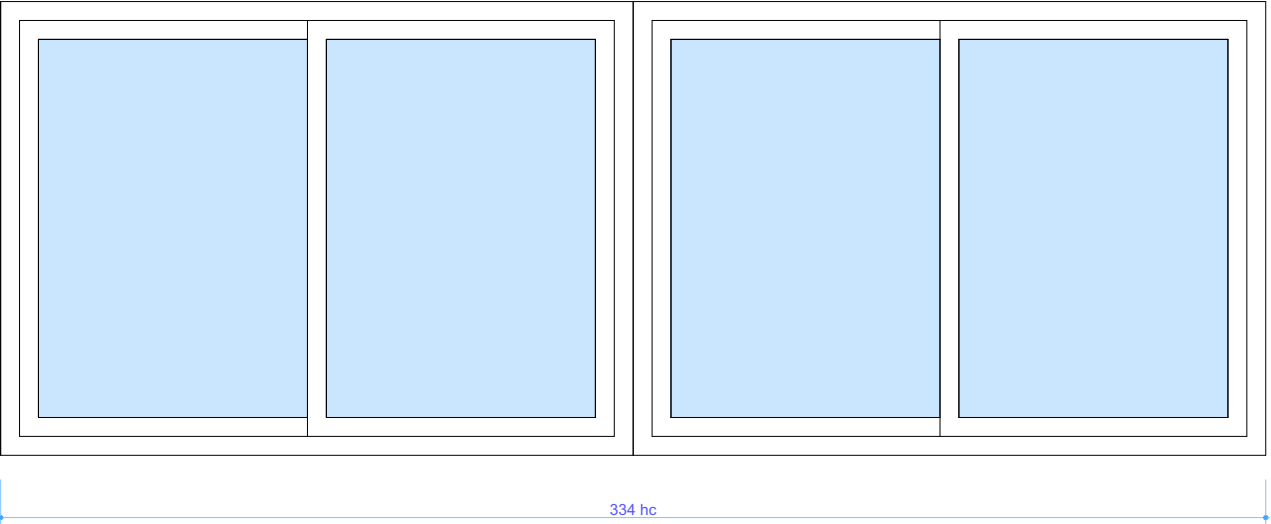

FAV3

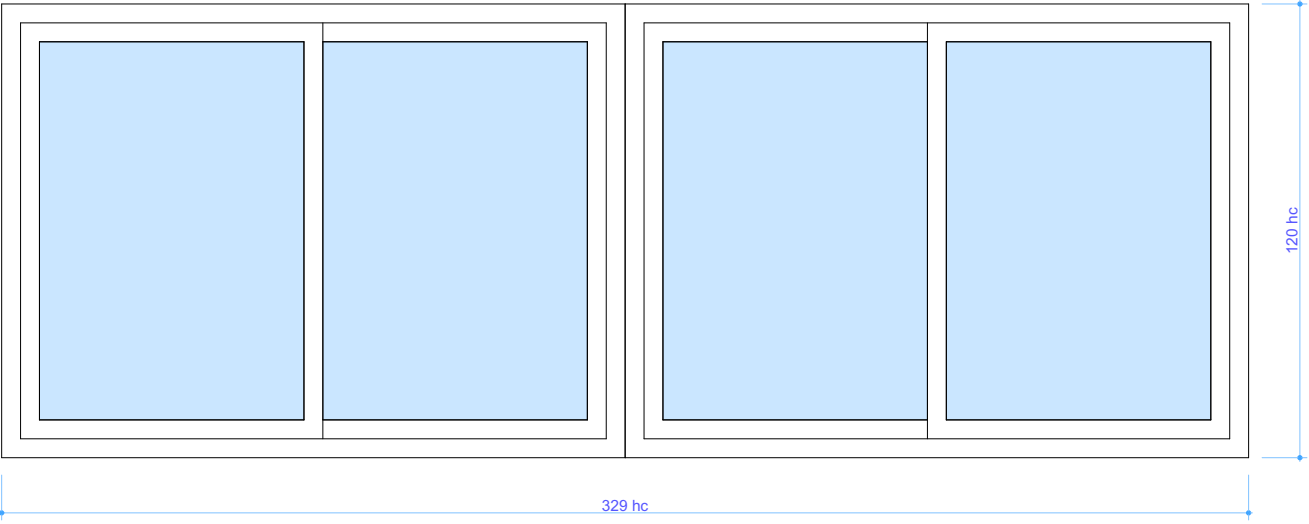


FAV4

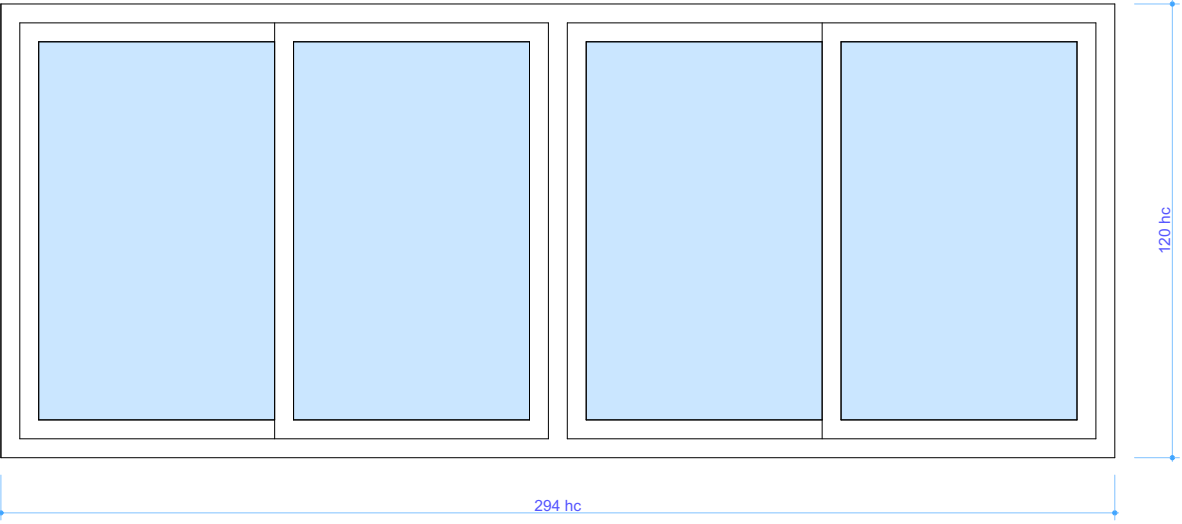


ENSAV1 PM1	Spécification Aluminium et Metallique PROJET DE CONSTRUCTION DE L'ENSEMBLE ARTISANAL DE LA VILLE D'OULMES	Date : 04/08/2016
		Echelle : 1/20
		S.sol: ☐ RDC: ☒ Etage: ☒ Terrasse ☐
		Faux Cadre:
		Cadre :
Fenêtre type :ENSAV2 - PM1		Chambranle :
Dimensions: voir type ci dessous		Quantité: ENSAV2=1-PM1=3
Type d'ouvrant : ensemble vitré comprenant 2 vantaux ouvrants à la française et 2 parties fixes porte métallique 2 vantaux ouvrants à la française		Localisation:ensemble artisanal RDC atelier : PM1=3
Panneau d'ouvrant : à la française		Etage administration : ENSAV2=1
Quincaillerie :		

ENSAV2

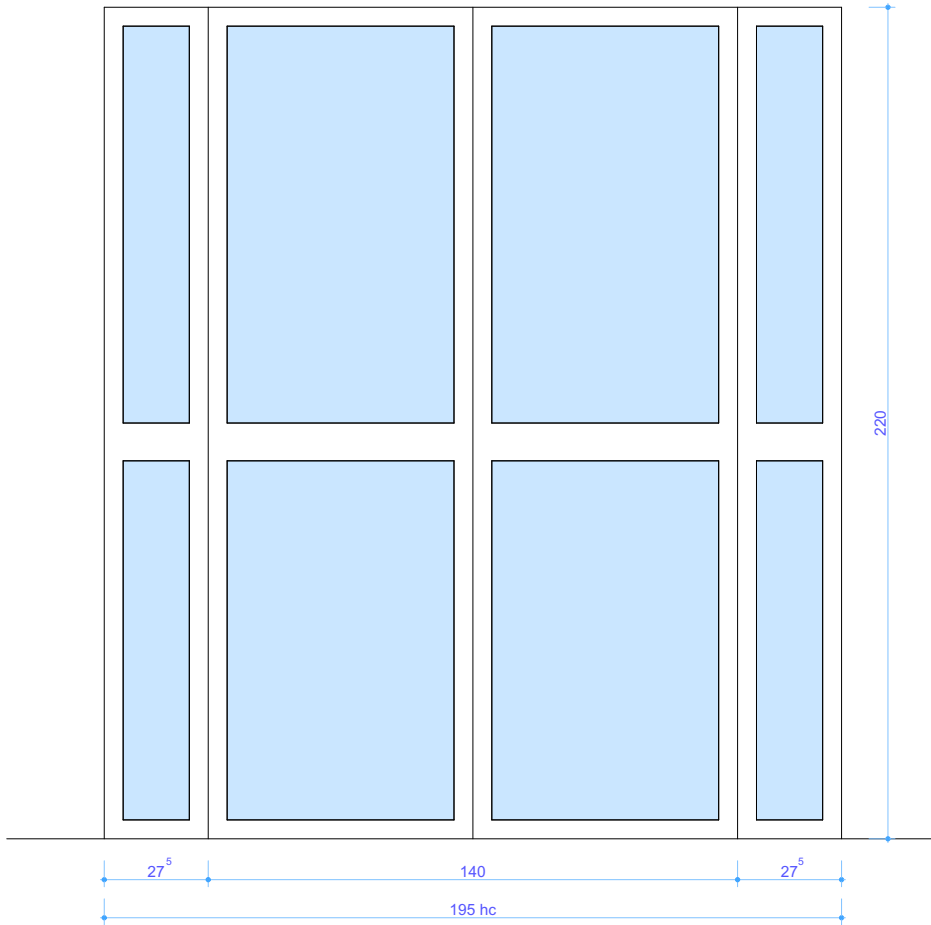


PM1

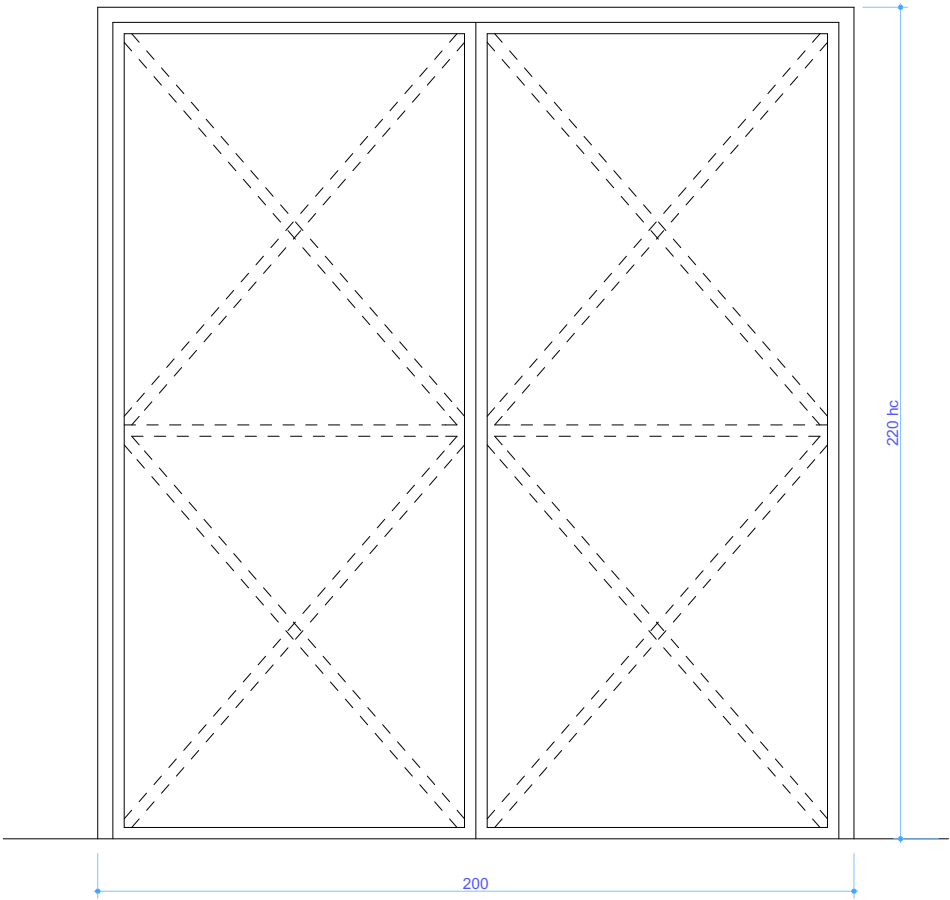


GP5-GP7 PG1	Spécification Metallique PROJET DE CONSTRUCTION DE L'ENSEMBLE ARTISANAL DE LA VILLE D'OULMES	Date : 04/08/2016
		Echelle : 1/20
		S.sol: ☐ RDC: ☒ Etage: ☒ Terrasse ☐
		Faux Cadre:
		Cadre :
Grille de défence type : PG1- GP5-GP7		Chambranle :
Dimensions: voir type ci dessous		Quantité: PG1=5 - GP5=12 -GP7=14
PG1 : porte grille à 2 vantaux ouvrant à la française		RDC administration : PG1=2 - GP5=6 - GP7=7
GP5-GP7 : grille de défence pour fenêtres		Etage administration : GP5=7 - GP7=7
Quincaillerie :		

GP7

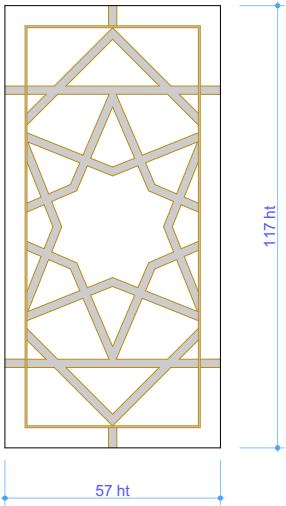

GP5

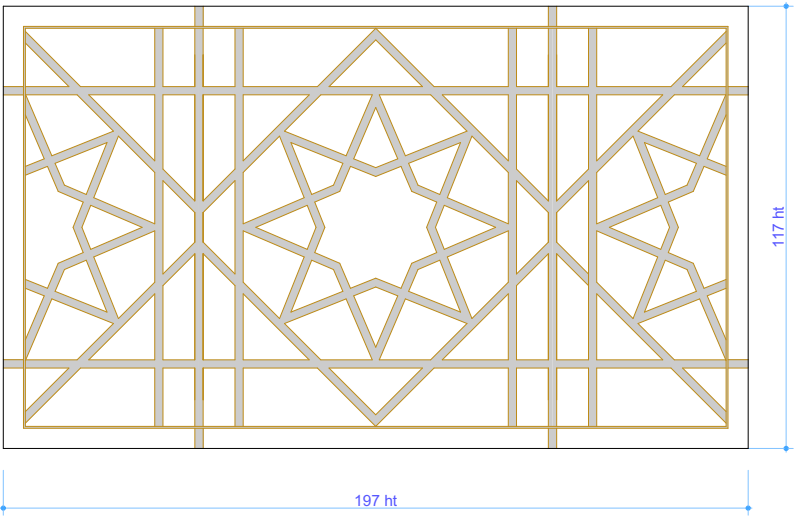

PG1

